



Продольный разрез 1-1 Мз 1:2000, Мв 1:100

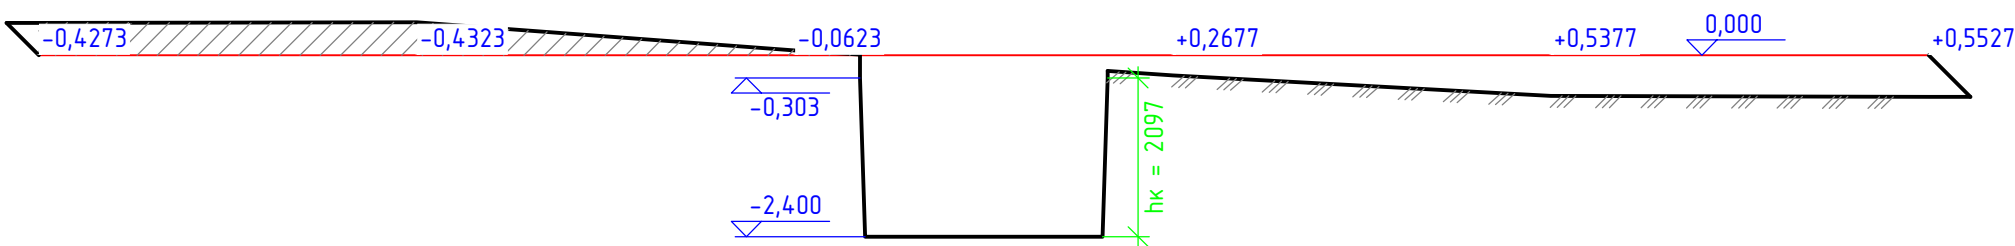

Поперечный разрез 2-2 Мз 1:2000, Мв 1:100

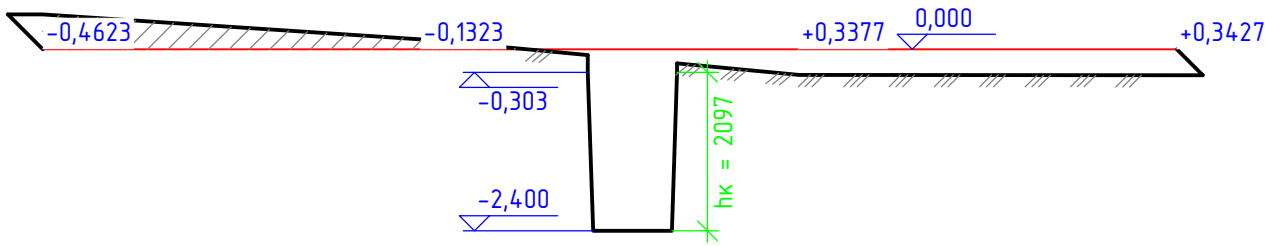

						НИУ МГСУ 08.05.01 – КР – 2026		
						Разработка технологической карты на производство земляных работ. Вариант 2, грунт – супесь		
Изм.	Кол.уч.	Лист	№ док.	Подп.	Дата	Графическая часть курсовой работы	Стадия	Лист
Разработал	Буев Д.Р.						У	3
Проверил	Забелина О.Б.					Продольный и поперечный разрезы площадки по котловану Мз 1:2000, Мв 1:100	Кафедра технологий и организации строительного производства	
Т. контр.								
Н. контр.								
Утв.								