


План строительной площадки с рабочими отметками и линией нулевых работ М 1:2000

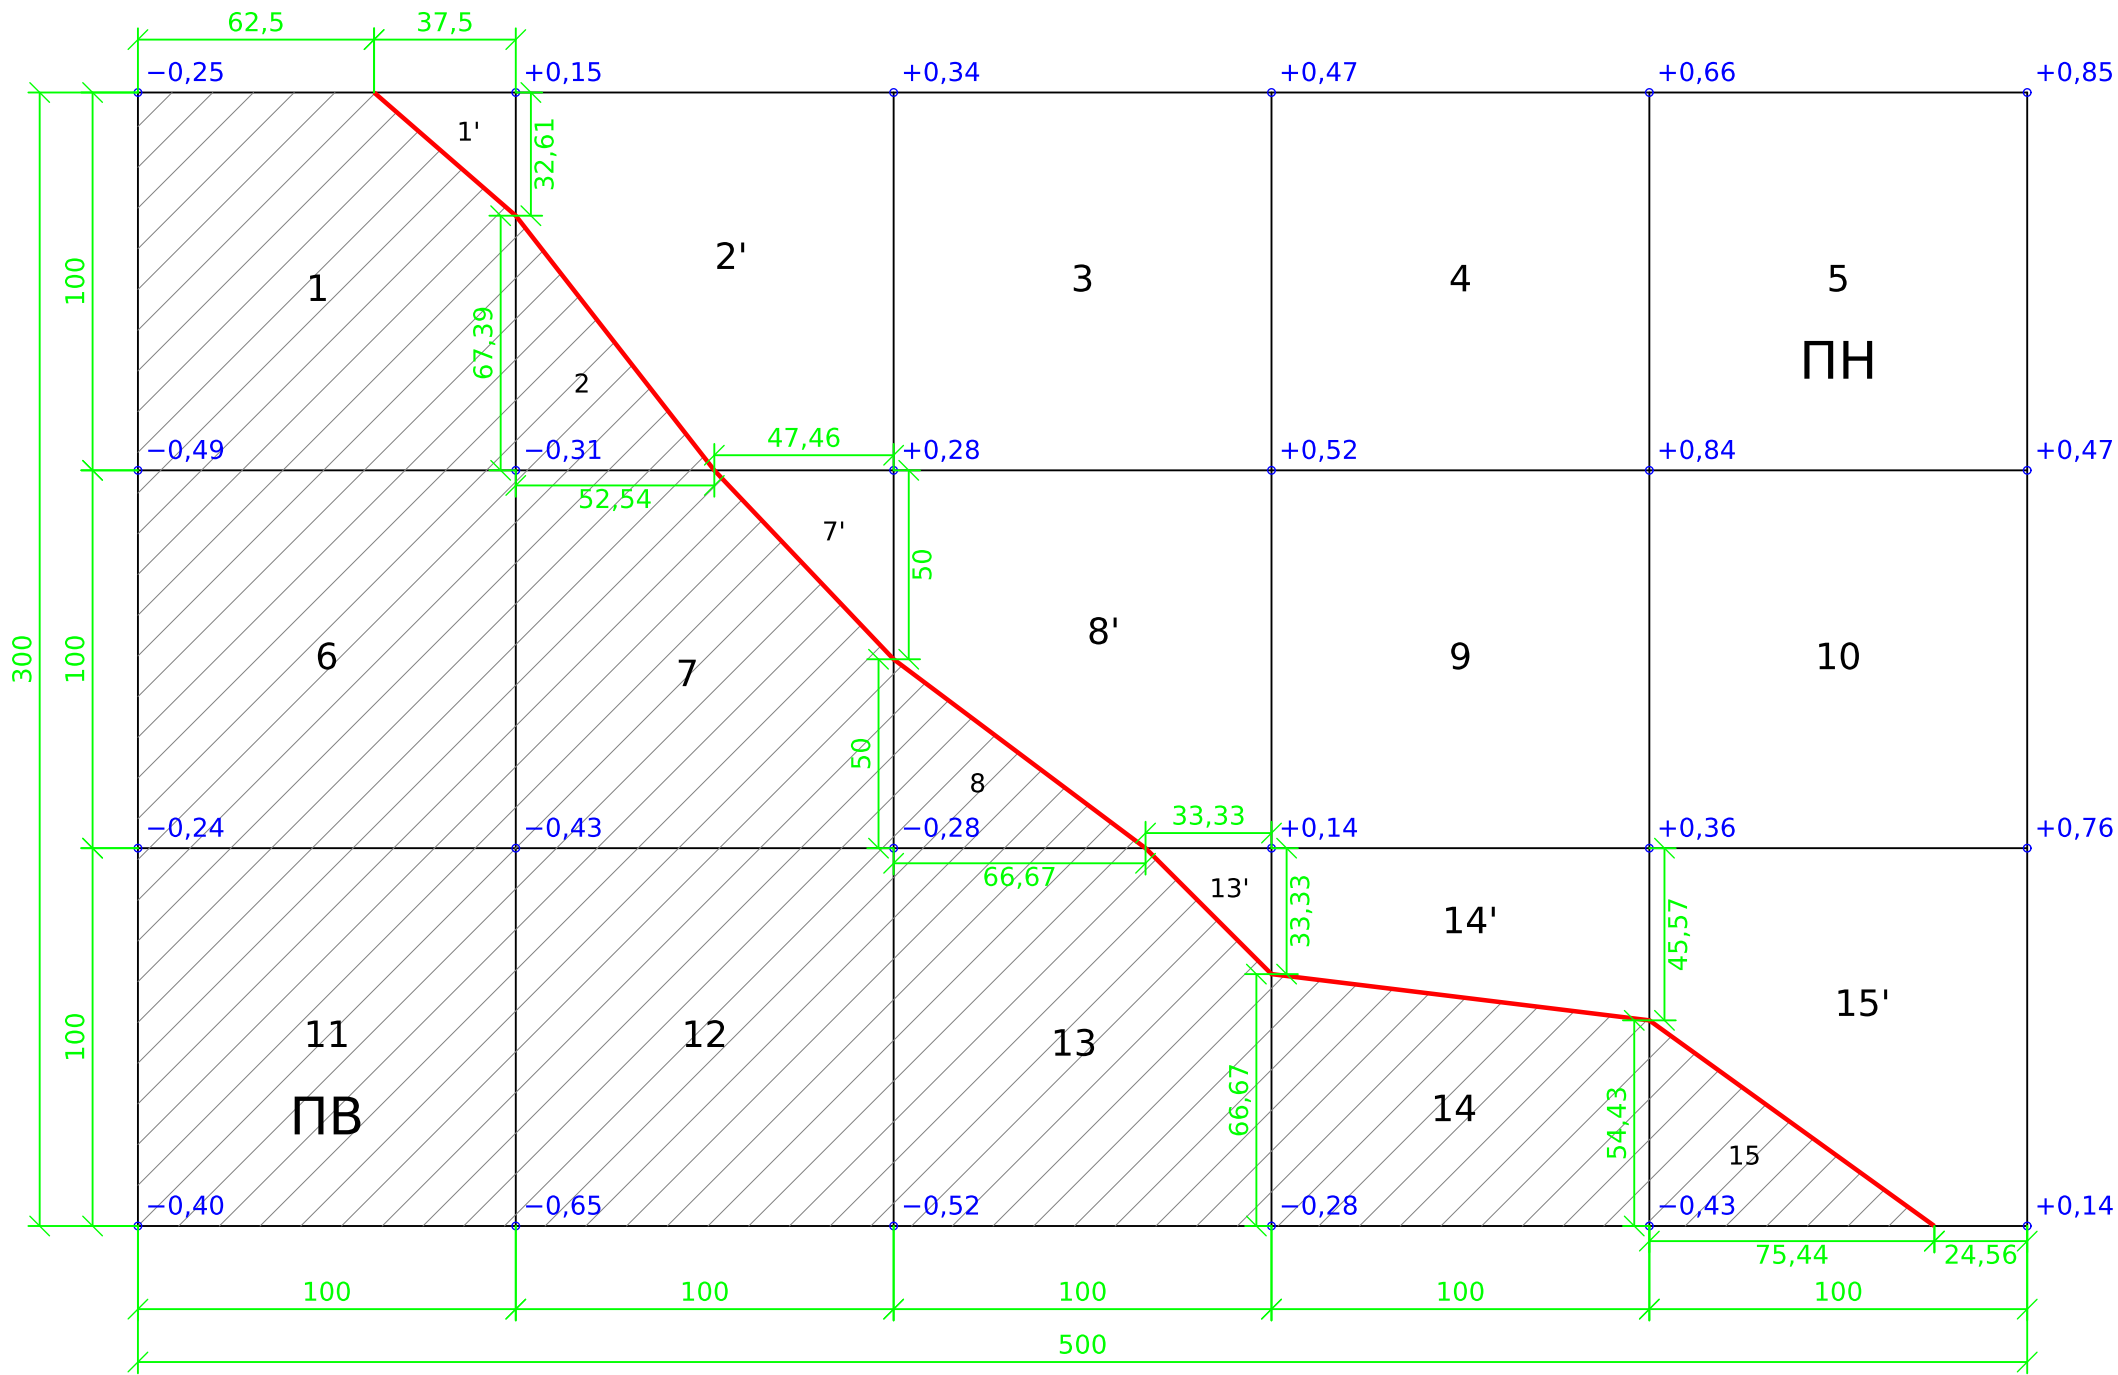

Условные обозначения

- линия нулевых работ (ЛНР)
- ПВ — планировочная выемка
- ПН — планировочная насыпь
- +0,15 — рабочая отметка, м: «+» насыпь, «-» выемка
- 7' — номер фигуры; штрих — насыпная часть квадрата
- 37,5 — расстояние до точки нулевых работ, м

Объёмы планировочных работ

	Ф, м²	V, м³
Выемка ПВ	69 191,63	20 192,08
Насыпь ПН	80 808,37	33 522,02
ПН / Кор, Кор = 1,04		32 232,71

						НИУ МГСУ 08.05.01 – КР – 2026			
						Разработка технологической карты на производство земляных работ. Вариант 2, грунт — супесь			
Изм.	Кол.уч.	Лист	№ док.	Подп.	Дата	Графическая часть курсовой работы	Стадия	Лист	Листов
Разработал	Був Д.Р.						У	1	
Проверил	Забелина О.Б.								
Т. контр.									
Н. контр.						План строительной площадки с рабочими отметками и ЛНР М 1:2000	Кафедра технологий и организации строительного производства		
Утв.									