# План строительной площадки с рабочими отметками и линией нулевых работ М 1:2000

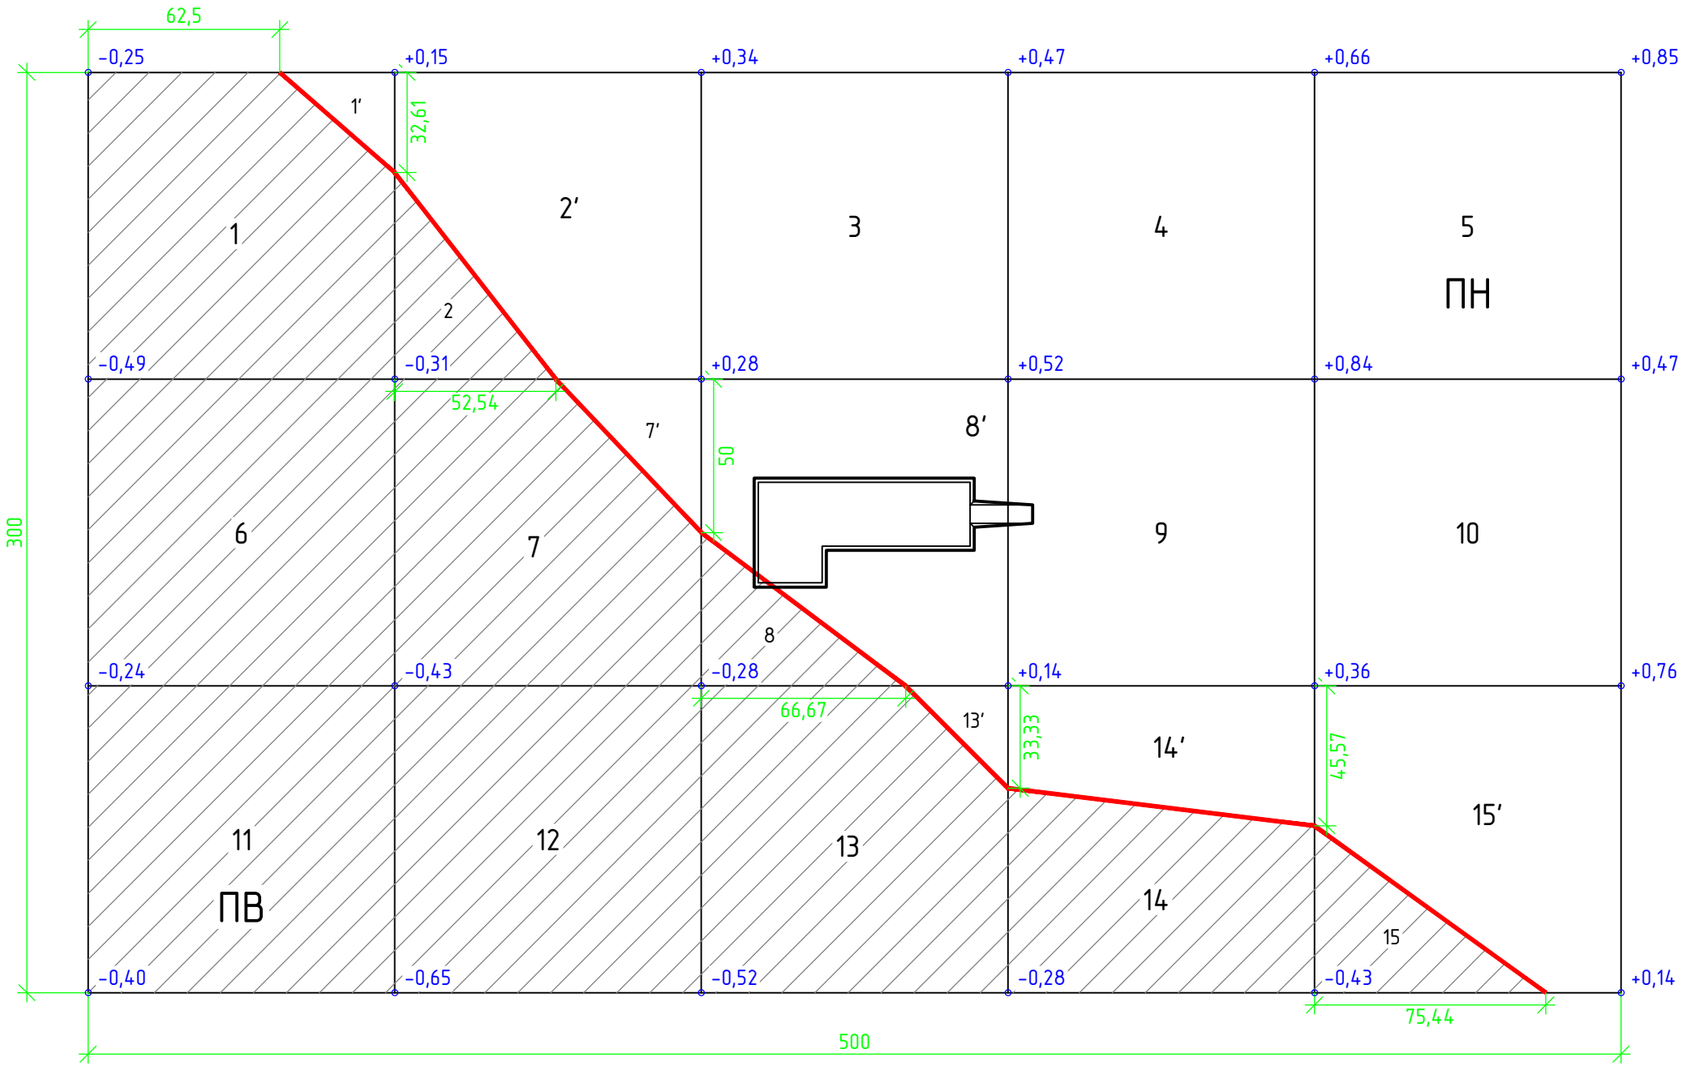


## Условные обозначения

- линия нулевых работ (ЛНР)
- ПВ – планировочная выемка
- ПН – планировочная насыпь
- +0,15 – рабочая отметка, м (+ насыпь, – выемка)
- 7′ – номер фигуры; со штрихом – насыпная часть квадрата
- 37,5 – расстояние до точки нулевых работ, м
- контур котлована

## Объемы планировочных работ

| | F, м² | V, м³ |
|---|---|---|
| Выемка ПВ | 69 191,63 | 20 209,47 |
| Насыпь ПН | 80 808,37 | 33 543,96 |
| ПН / Кор, Кор = 1,04 | | 32 253,81 |

| Изм. | Кол.уч. | Лист | №док. | Подп. | Дата |
|---|---|---|---|---|---|
| Разработал | | Буев Д.Р. | | | |
| Проверил | | Забелина О.Б. | | | |
| Т. контр. | | | | | |
| | | | | | |
| Н. контр. | | | | | |
| Утв. | | | | | |

НИУ МГСУ 08.05.01 – КР – 2026

Разработка технологической карты на производство земляных работ. Вариант 2, грунт – супесь

| Графическая часть курсовой работы | Стадия | Лист | Листов |
|---|---|---|---|
| | У | 1 | 8 |

План строительной площадки с рабочими отметками и ЛНР М 1:2000

Кафедра технологии и организации строительного производства