Продольный разрез 1-1 Мг 1:2000, Мв 1:100

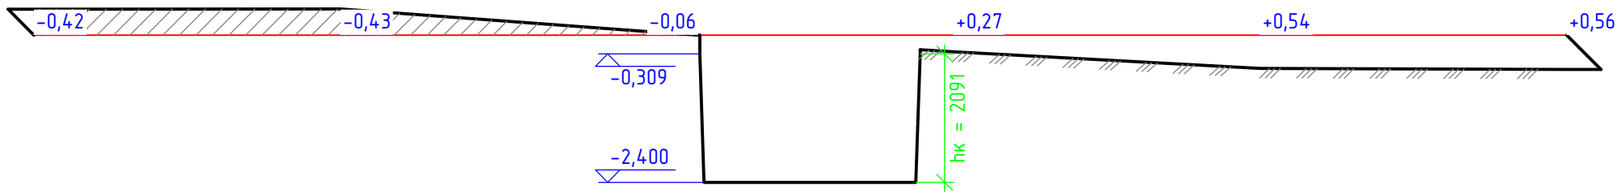

Поперечный разрез 2-2 Мг 1:2000, Мв 1:100

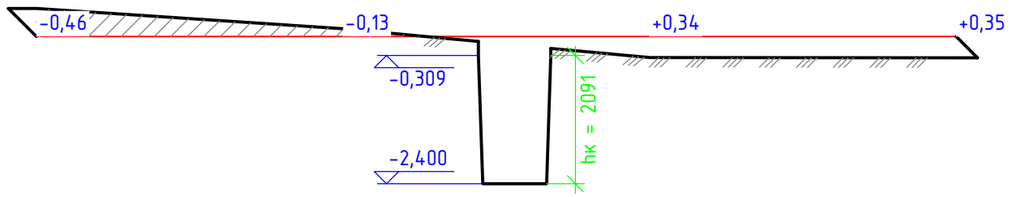

Изм.	Кол.уч.	Лист	№док.	Подп.	Дата
Разработал		Буев Д.Р.			
Проверил		Забелина О.Б.			
Т. контр.					
Н. контр.					
Утв.					

НИУ МГСУ 08.05.01 – КР – 2026

Разработка технологической карты на производство земляных работ. Вариант 2, грунт – супесь

Графическая часть курсовой работы	Стадия	Лист	Листов
	У	3	

Продольный и поперечный разрезы площадки по котловану Мг 1:2000, Мв 1:100	Кафедра технологии и организации строительного производства