


План строительной площадки с рабочими отметками и линией нулевых работ М 1:2000

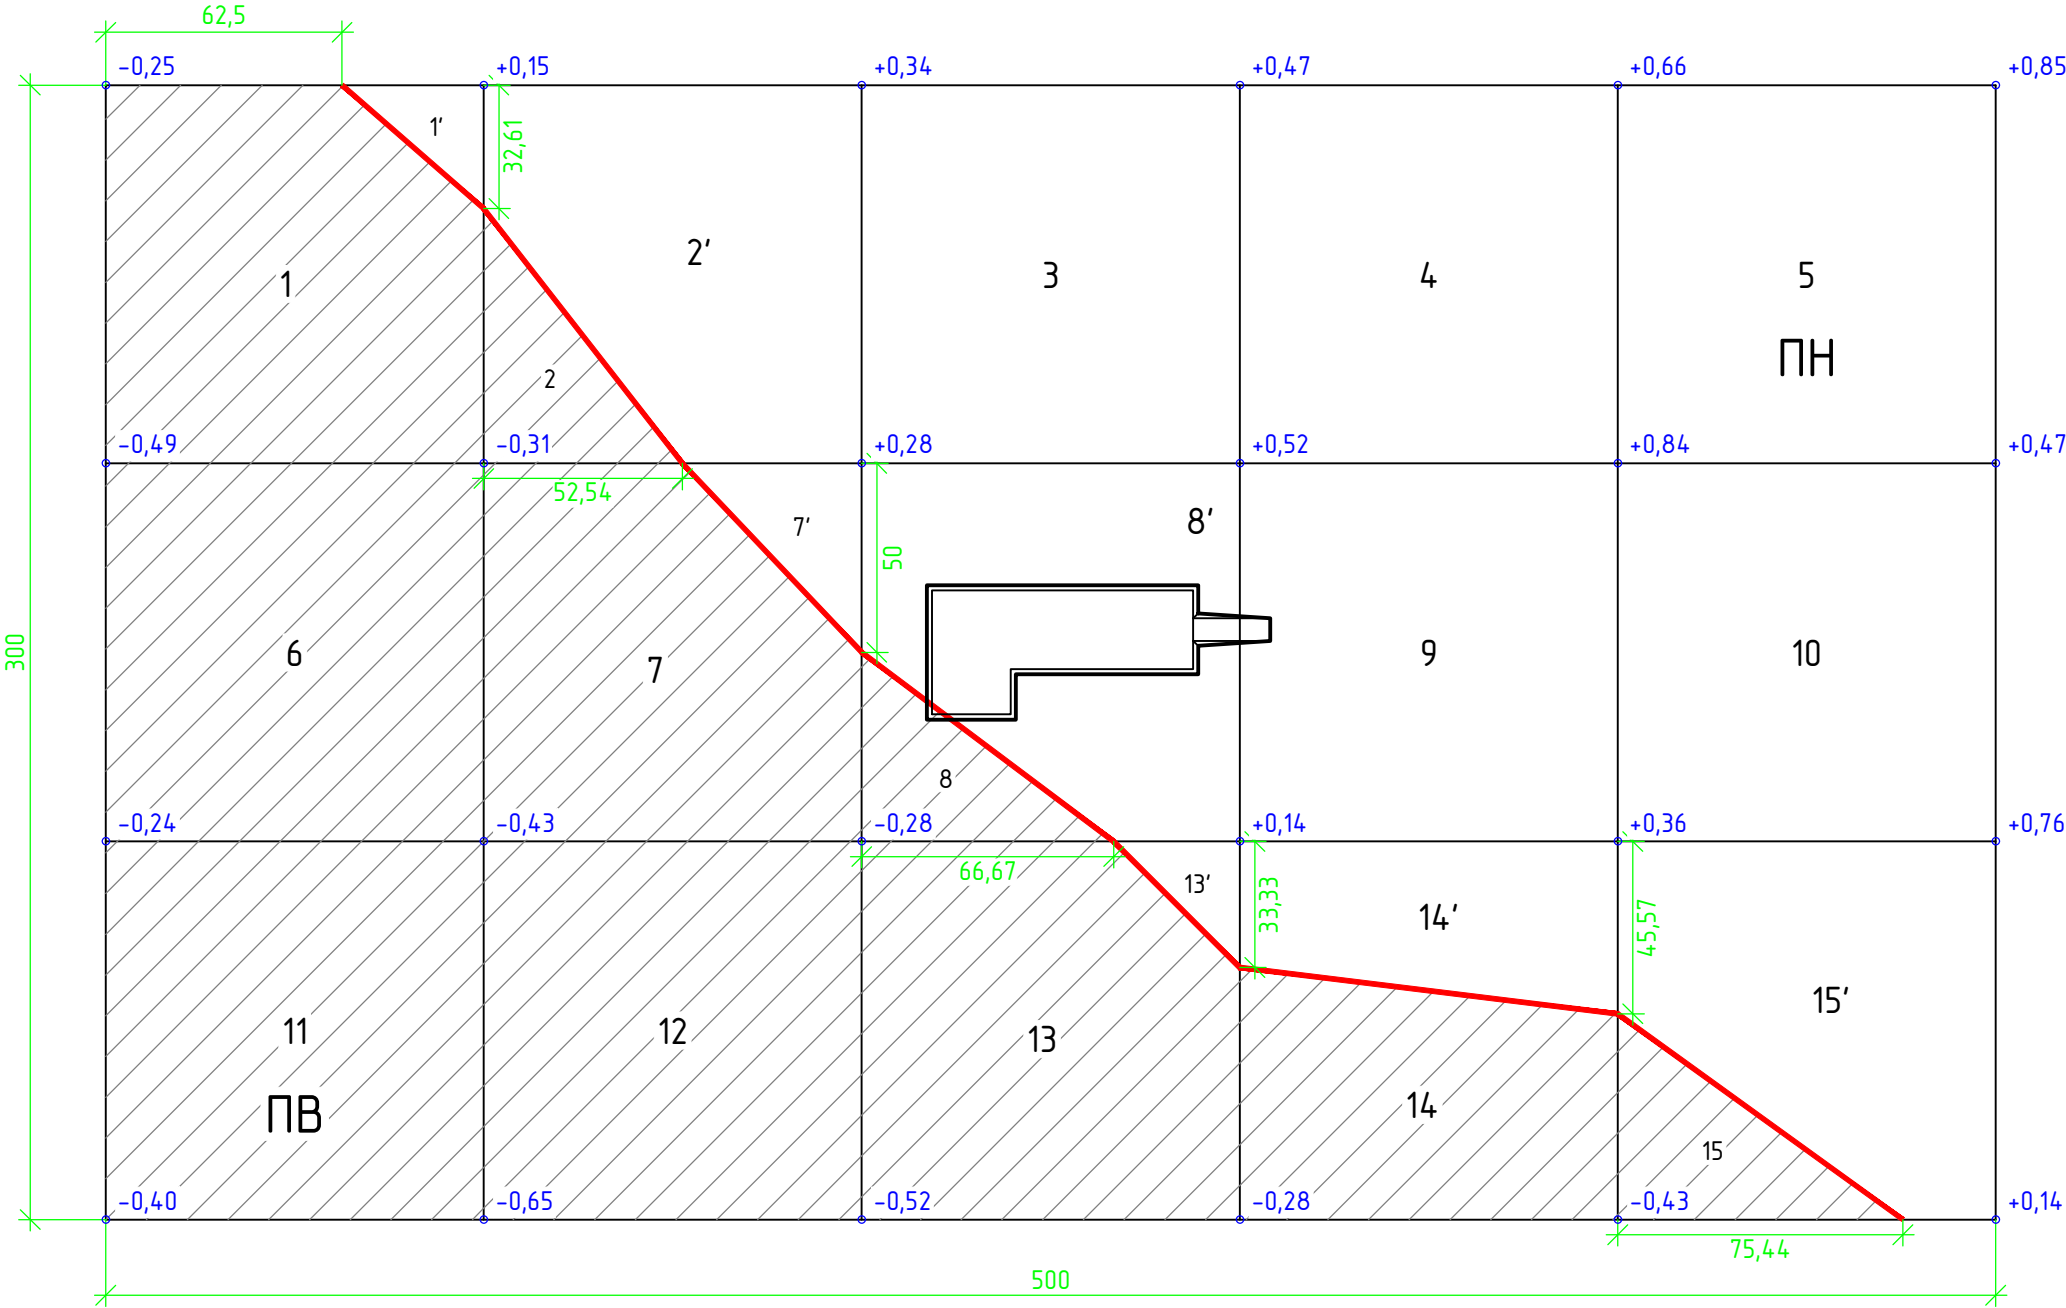

Условные обозначения

- линия нулевых работ (ЛНР)
- ▨ - ПВ - планировочная выемка
- - ПН - планировочная насыпь
- +0,15 - рабочая отметка, м (+ насыпь, - выемка)
- 7' - номер фигуры; со штрихом - насыпная часть квадрата
- 37,5 - расстояние до точки нулевых работ, м
- - контур котлована

Объемы планировочных работ

|                      | Ф, м²     | V, м³     |
|----------------------|-----------|-----------|
| Выемка ПВ            | 69 191,63 | 20 209,47 |
| Насыпь ПН            | 80 808,37 | 33 543,96 |
| ПН / Кор, Кор = 1,04 |           | 32 253,81 |

|            |               |      |        |       |      |                                                                                            |                                                                   |      |
|------------|---------------|------|--------|-------|------|--------------------------------------------------------------------------------------------|-------------------------------------------------------------------|------|
|            |               |      |        |       |      | НИУ МГСУ 08.05.01 - КР - 2026                                                              |                                                                   |      |
|            |               |      |        |       |      | Разработка технологической карты на производство земляных работ. Вариант 2, грунт - супесь |                                                                   |      |
| Изм.       | Кол.уч.       | Лист | № док. | Подп. | Дата | Графическая часть<br>курсовой работы                                                       | Стадия                                                            | Лист |
| Разработал | Буев Д.Р.     |      |        |       |      |                                                                                            | У                                                                 | 1    |
| Проверил   | Забелина О.Б. |      |        |       |      |                                                                                            |                                                                   | 5    |
| Т. контр.  |               |      |        |       |      | План строительной площадки<br>с рабочими отметками и ЛНР<br>М 1:2000                       | Кафедра технологий<br>и организации строительного<br>производства |      |
| Н. контр.  |               |      |        |       |      |                                                                                            |                                                                   |      |
| Утв.       |               |      |        |       |      |                                                                                            |                                                                   |      |