Генеральный план. Системы В1, К1 (1 : 500)

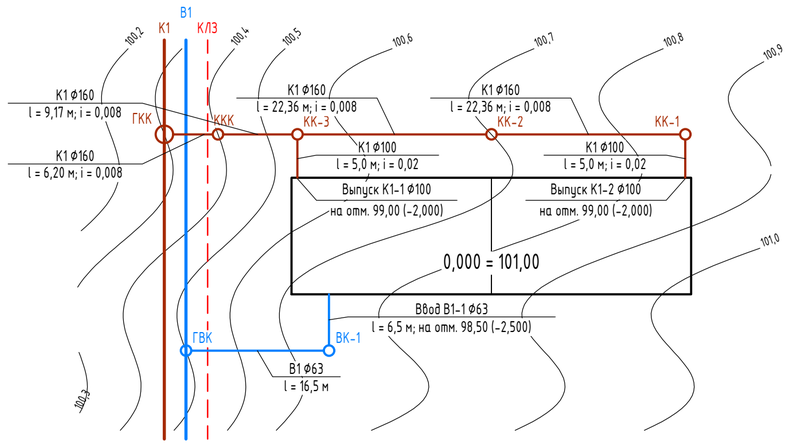

						НИУ МГСУ 08.03.01*-КП-2026 - ВК			
						Системы холодного водоснабжения и водоотведения здания			
Изм.	Колуч.	Лист	№док.	Подп.	Дата				
Разраб.						Наименование здания. Жилой дом. Вариант 3	Стадия	Лист	Листов
Пров.							У	8	8
						Генеральный план. Системы В1, К1	НИУ МГСУ ИИЭСМ Кафедра «Водоснабжение и водоотведение»		

Согласовано

Взам. инв. №

Подп. и дата

Инв. № подл.

Формат А2 420 x 594