
# Аксонометрическая схема. Система В1

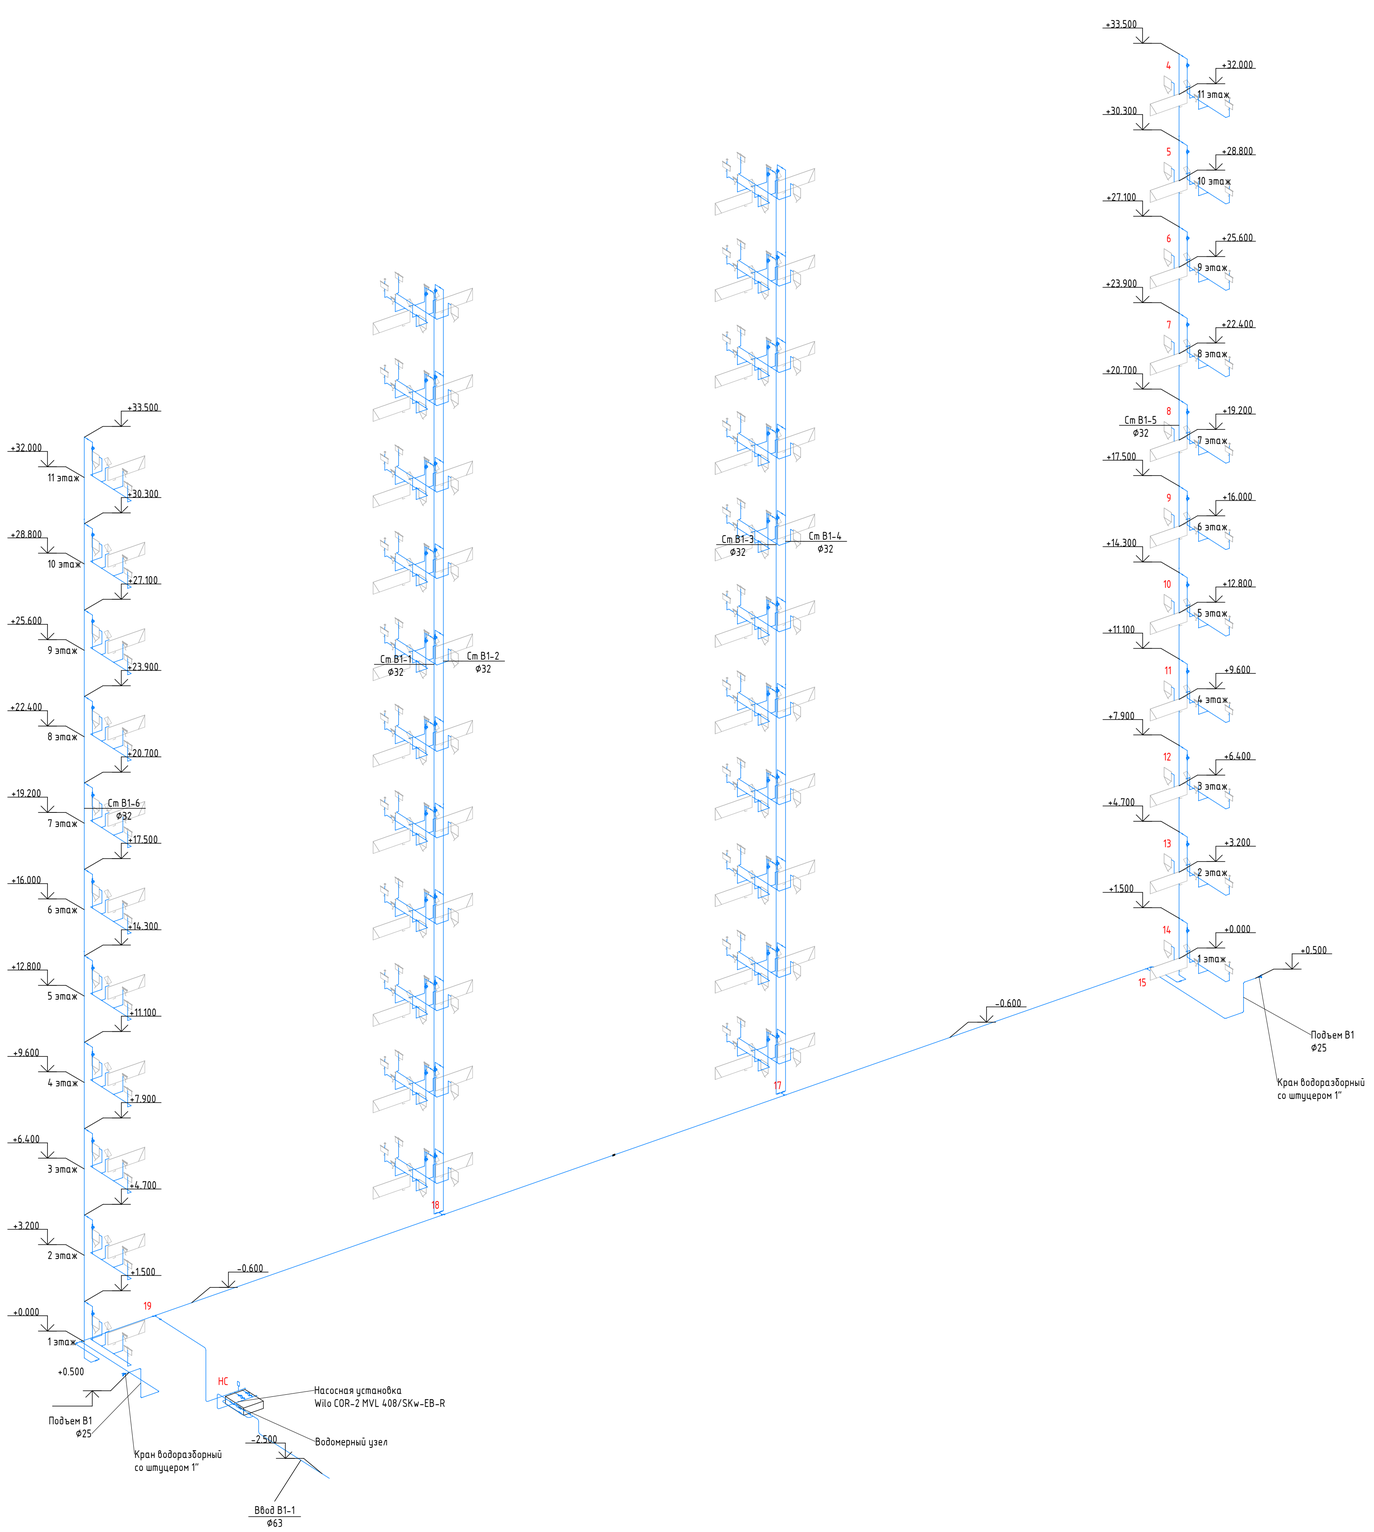


Примечания:
1. Планы и схемы систем рассматривать совместно.
2. Все трубопроводы систем водоснабжения, кроме подводок к санитарным приборам, покрываются теплоизоляцией во избежание теплопотерь и появления конденсата.
3. Трубопроводы прокладывать с уклоном 0,002 в сторону сливной арматуры или смесителей.
4. Монтаж трубопроводов производить с учетом прокладки смежных систем.
5. Отметки трубопроводов даны по оси трубы.
6. Отметки трубопроводов и оборудования даны относительно нуля здания.
7. Привязки и отметки трубопроводов уточнять по месту.

Согласовано

Взам. инв. №

Подп. и дата

Инв. № подл.

| Изм. | Кол.уч. | Лист | №док. | Подп. | Дата |
|---|---|---|---|---|---|
| Разраб. | | Буев | | | |
| Пров. | | | | | |

НИУ МГСУ 08.03.01*-КП-2026 - ВК

Системы холодного водоснабжения и водоотведения здания

| Наименование здания. Жилой дом. Вариант 3 | Стадия | Лист | Листов |
|---|---|---|---|
| | У | 3 | 7 |
| Аксонометрическая схема. Система В1 | НИУ МГСУ ИИЭСМ Кафедра "Водоснабжение и водоотведение" | | |

Формат А1 594 x 841