


План строительной площадки с рабочими отметками, линией нулевых работ и котлованом М 1:2000

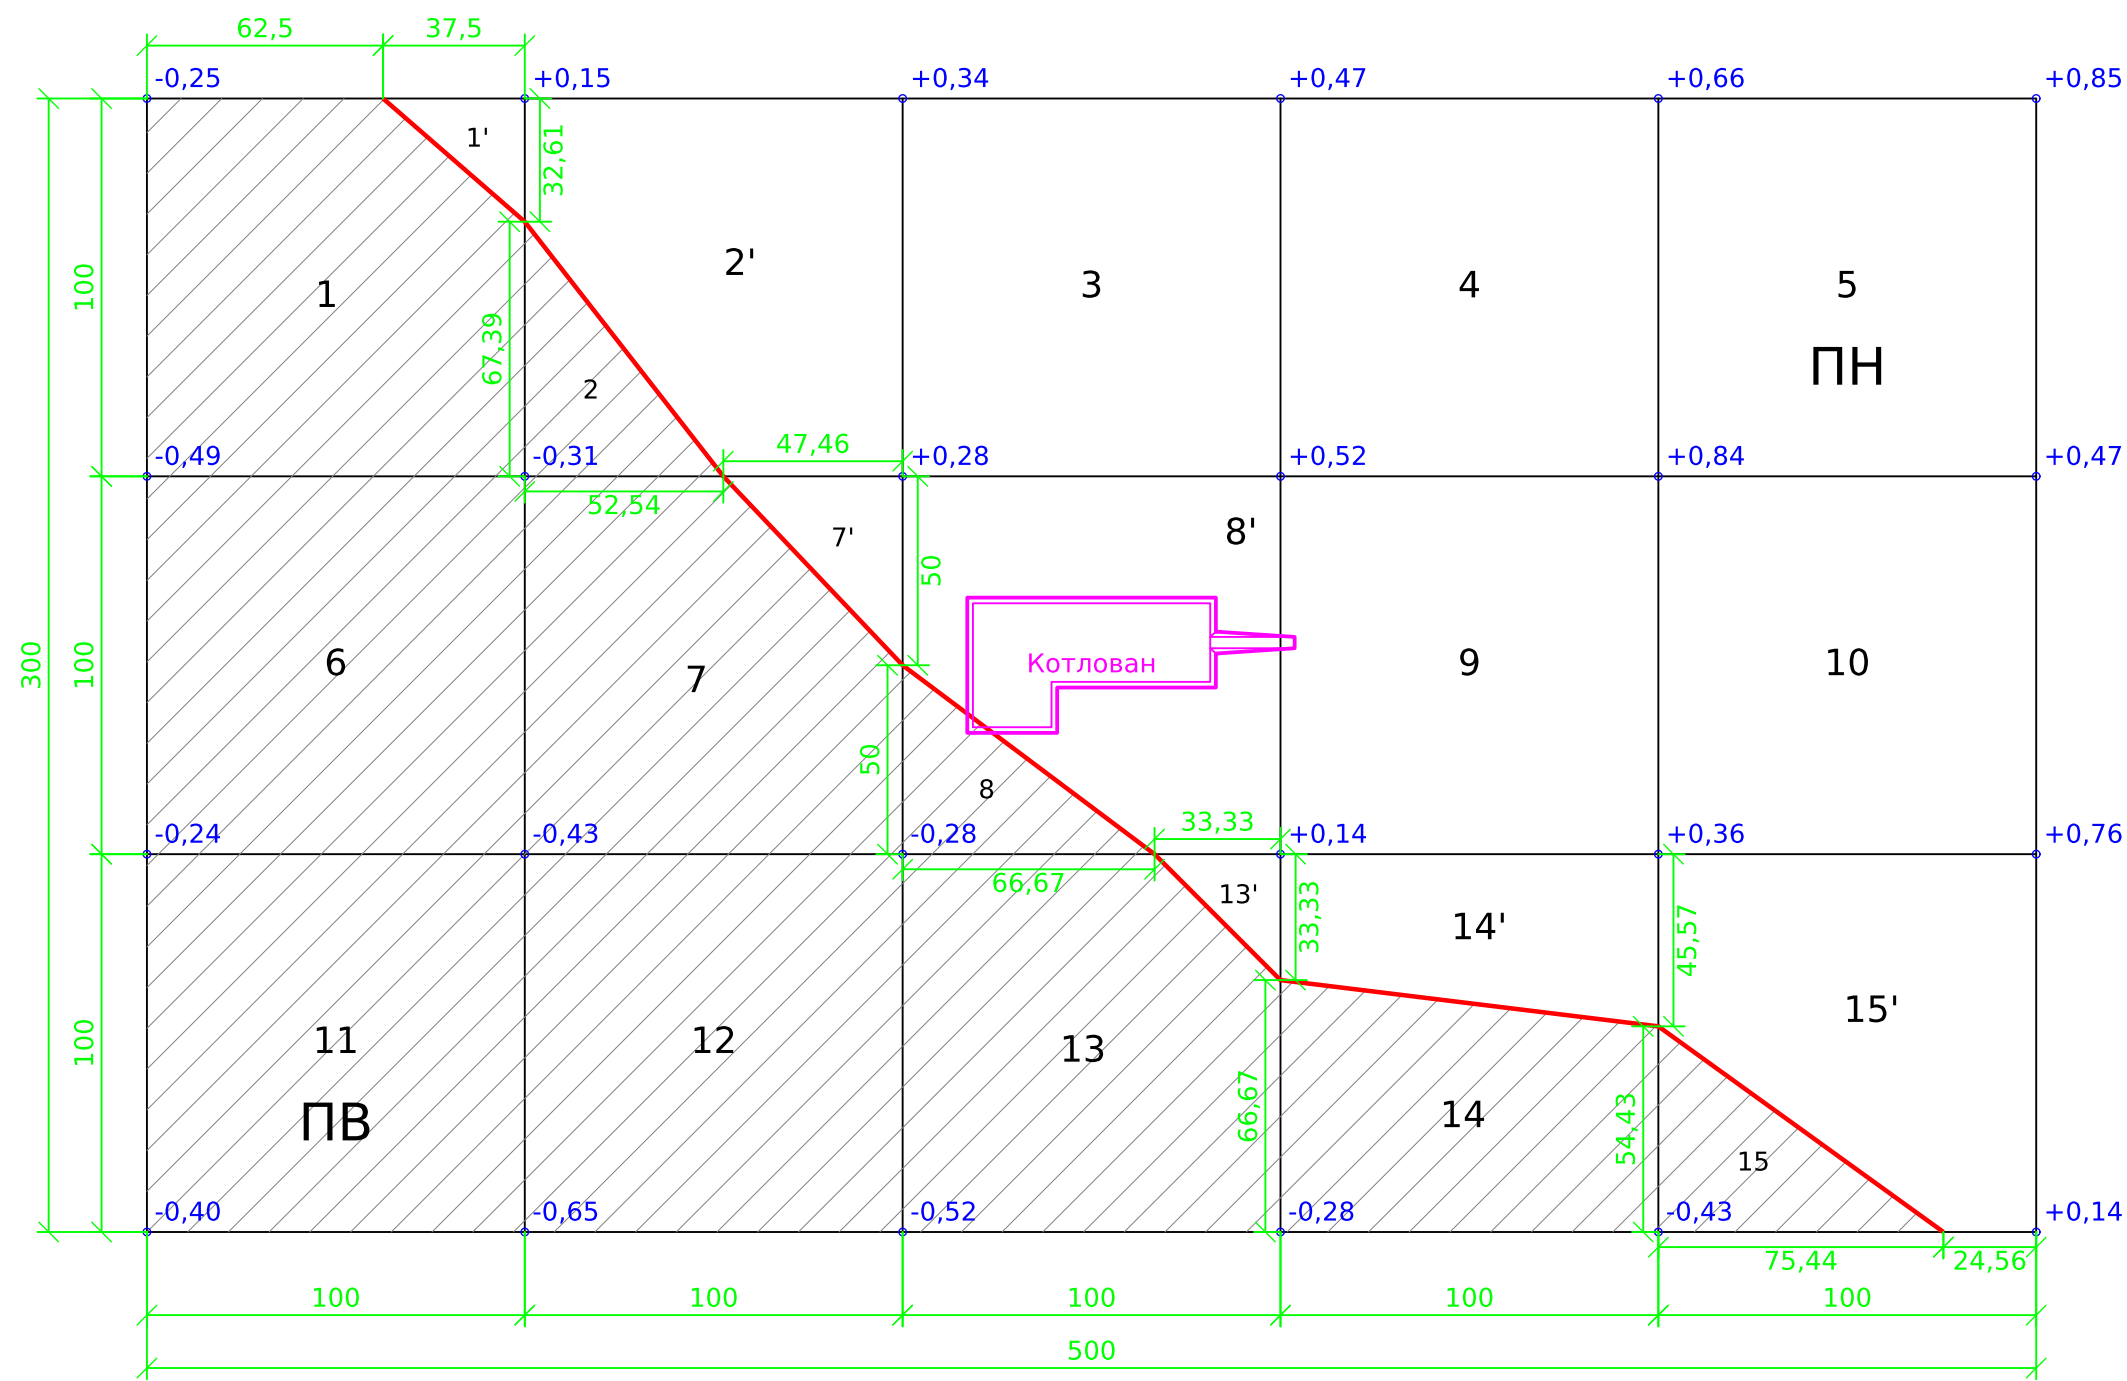

Условные обозначения

- линия нулевых работ (ЛНР)
- ▨ - ПВ - планировочная выемка
- - ПН - планировочная насыпь
- +0,15 - рабочая отметка, м (+ насыпь, - выемка)
- 7' - номер фигуры; со штрихом - насыпная часть квадрата
- 37,5 - расстояние до точки нулевых работ, м
- Котлован: бровка и подошва (с пандусом)

Объёмы планировочных работ

	Ф, м²	V, м³
Выемка ПВ	69 191,63	20 192,08
Насыпь ПН	80 808,37	33 522,02
ПН / Кор, Кор = 1,04		32 232,71

						НИУ МГСУ 08.05.01 - КР - 2026			
						Разработка технологической карты на производство земляных работ. Вариант 2, грунт - супесь			
Изм.	Кол.уч.	Лист	№ док.	Подп.	Дата	Графическая часть курсовой работы	Стадия	Лист	Листов
Разработал	Буев Д.Р.						У	1	2
Проверил	Забелина О.Б.								
Т. контр.									
Н. контр.						План строительной площадки с рабочими отметками, ЛНР и котлованом М 1:2000	Кафедра технологий и организации строительного производства		
Утв.									


План котлована М 1:500

Параметры котлована


Параметр	Обозн.	Значение
Глубина по заданию, м	Нк	2,4
Рабочая отметка в центре, м	hp	+0,165
Фактическая глубина, м	hk	2,235
Откос (супесь, hk до 3 м)	1:m	1:0,67
Заложение откоса, м	l	1,497
Низ котлована, м		62,8 x 32,8
Верх котлована, м		65,79 x 35,79
Площадь по низу, м²	Фк.н	1 555,84
Площадь по верху, м²	Фк.в	1 851,12
Пандус: ширина x длина, м	bp	3 x 22,35

Объёмы котлована

Объём	Обозн.	V, м³
Котлован без пандуса		3 802,50
Пандус	Vпан	99,86
Котлован всего	Vк	3 902,37
Подсыпка (щебень)	Vподс	155,58
Бетонная подготовка	Vб.п	219,19
Подземная часть здания	Vп.ч	2 681,06
Обратная засыпка	Vo.з	846,54

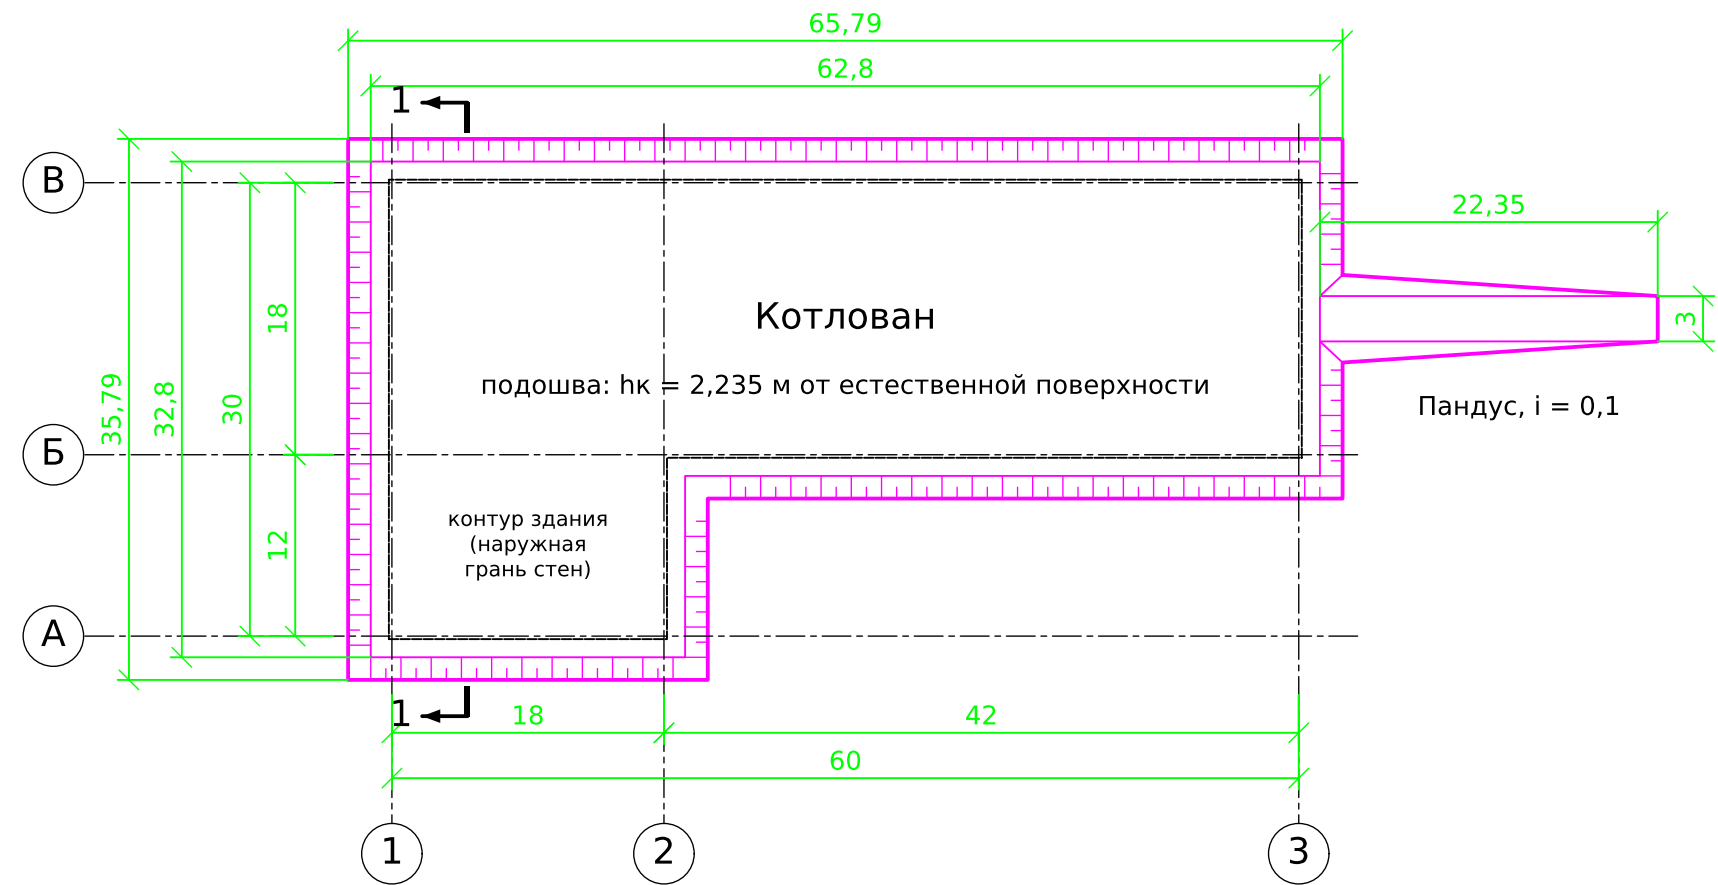

1-1 (фрагмент) М 1:50

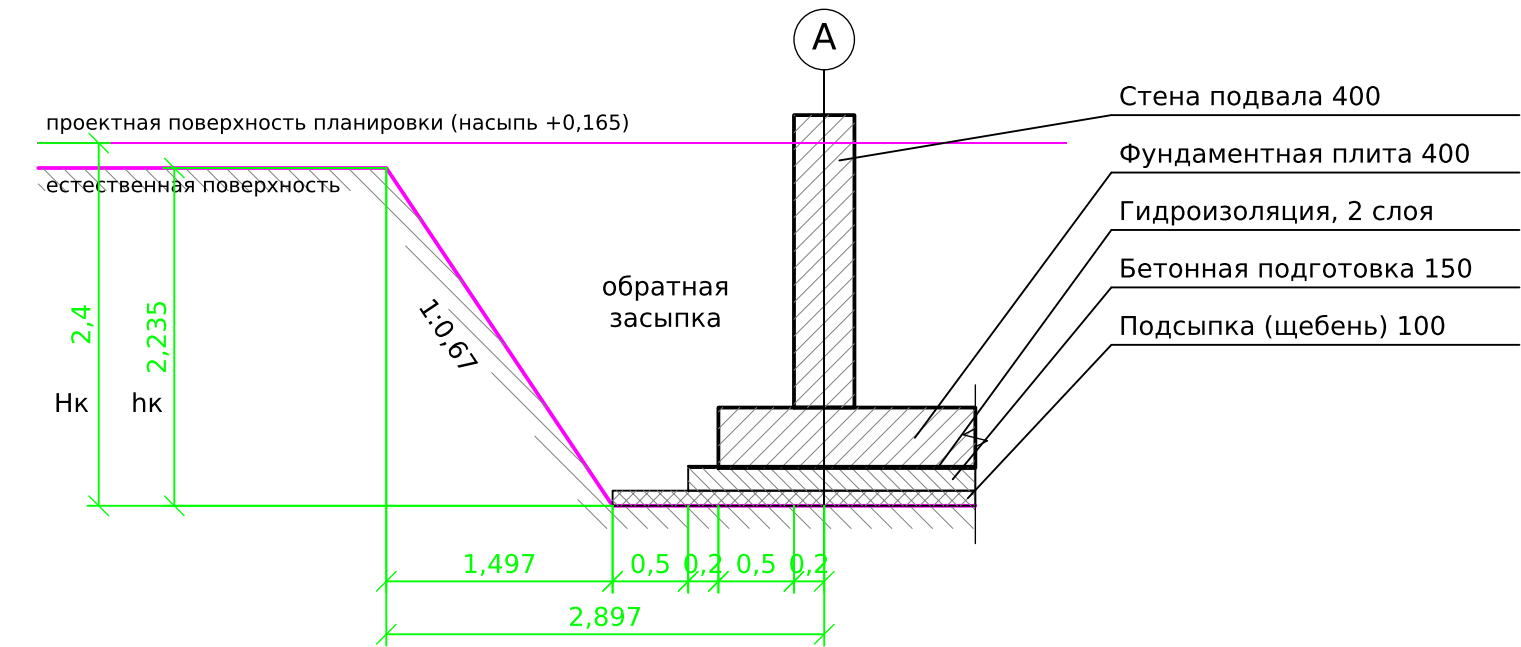

Примечания

- Размеры - в метрах. Грунт - супесь, откос по прил. 3 методички.
- Здание - вариант размещения 8: центр здания совпадает с центром квадрата 8.
- Котлован пересечён ЛНР; среднее рабочих отметок по углам +0,144 - котлован в зоне насыпи и разрабатывается от естественной поверхности: $hk = Нк - hp = 2,4 - 0,165 = 2,235$ м.
- Низ котлована - 1,4 м от осей: 0,2 до грани стены + 0,5 вылет плиты + 0,2 выход подготовки + 0,5 рабочая зона.
- Пандус принят однополосный: $bp = 3$ м, $i = 0,1$.

						НИУ МГСУ 08.05.01 - КР - 2026			
						Разработка технологической карты на производство земляных работ. Вариант 2, грунт - супесь			
Изм.	Кол.уч.	Лист	№ док.	Подп.	Дата	Графическая часть курсовой работы	Стадия	Лист	Листов
Разработал	Буев Д.Р.						У	2	
Проверил	Забелина О.Б.								
Т. контр.									
Н. контр.						Котлован. План М 1:500, разрез 1-1 (фрагмент) М 1:50	Кафедра технологий и организации строительного производства		
Утв.									