План строительной площадки с окончательными рабочими отметками, ЛНР и обводами Мг 1:2000, Мв 1:100

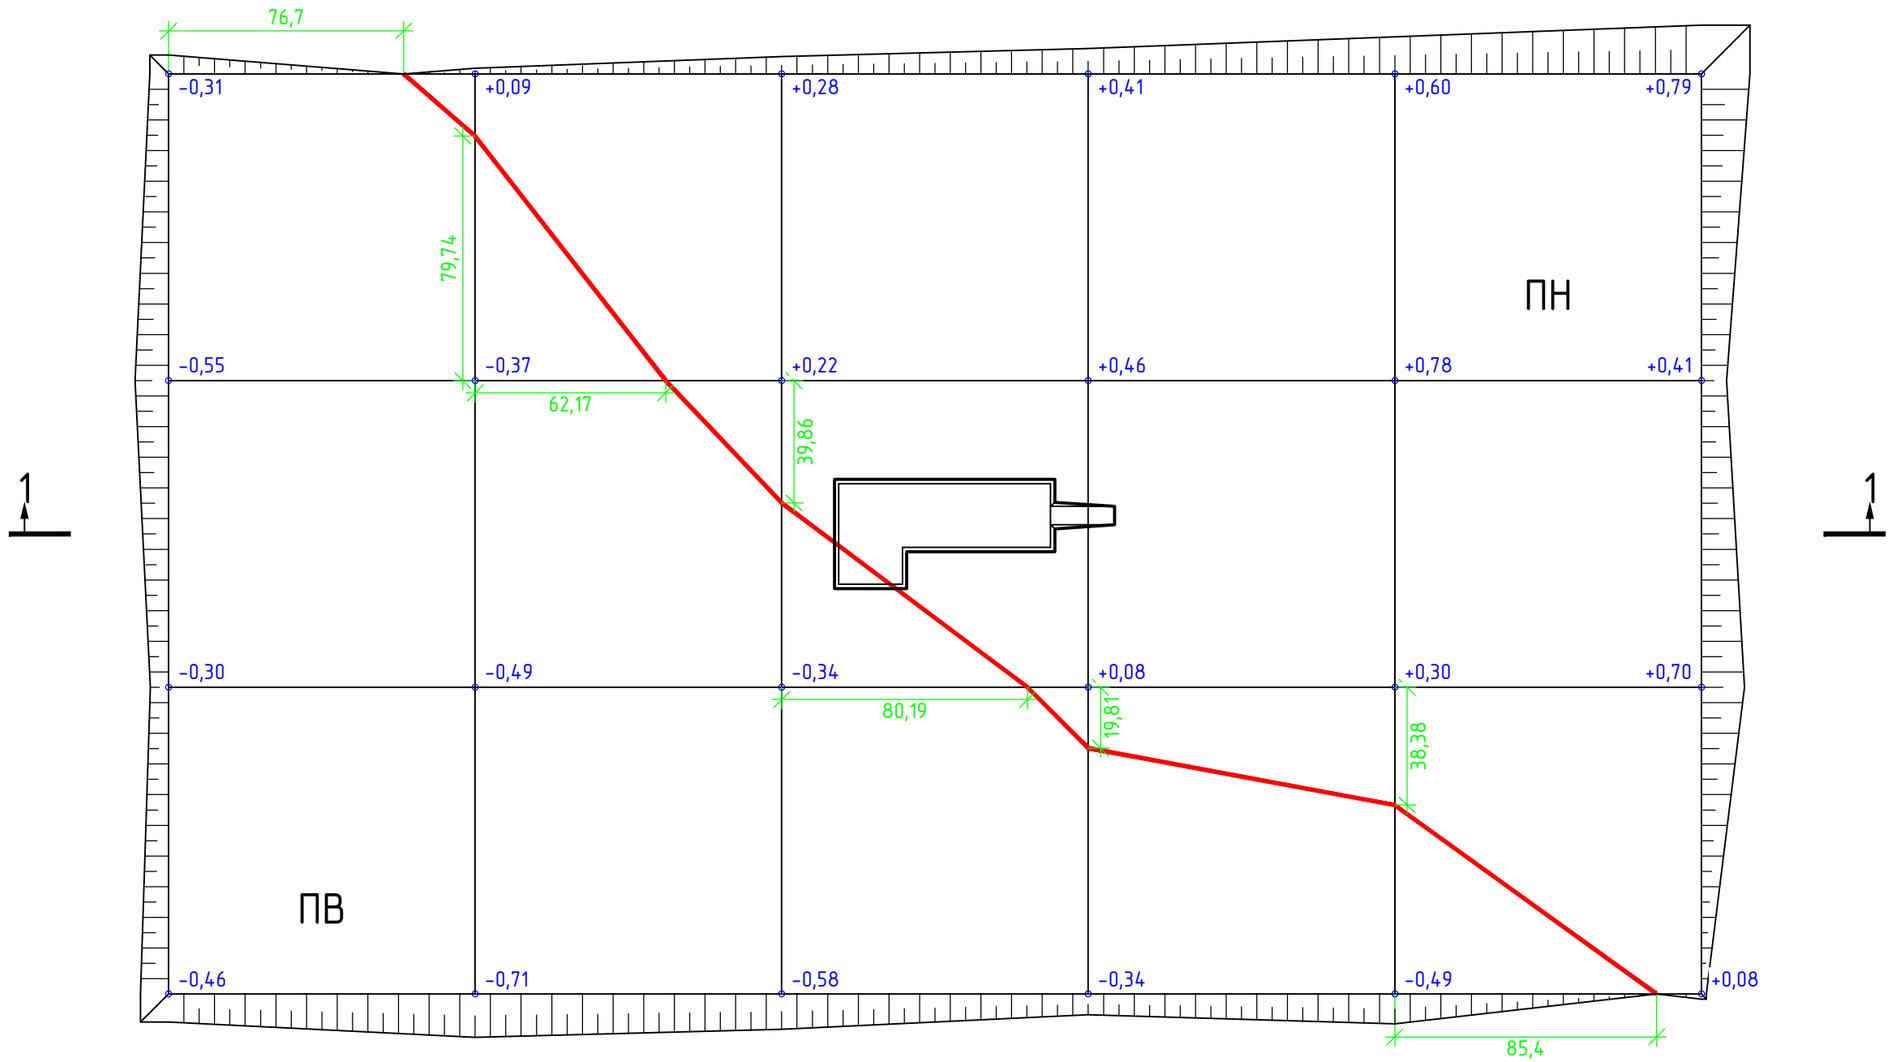

Изм.	Кол.уч.	Лист	№док.	Подп.	Дата
Разработал		Буев Д.Р.			
Проверил		Забелина О.Б.			
Т. контр.					
Н. контр.					
Утв.					

НИУ МГСУ 08.05.01 - КР - 2026

Разработка технологической карты на производство земляных работ. Вариант 2, грунт - супесь

Графическая часть курсовой работы	Стадия	Лист	Листов
	У	2	

План площадки с окончательными рабочими отметками и обводами Мг 1:2000, Мв 1:100	Кафедра технологии и организации строительного производства