Схема производства работ по вертикальной планировке строительной площадки М 1:2000

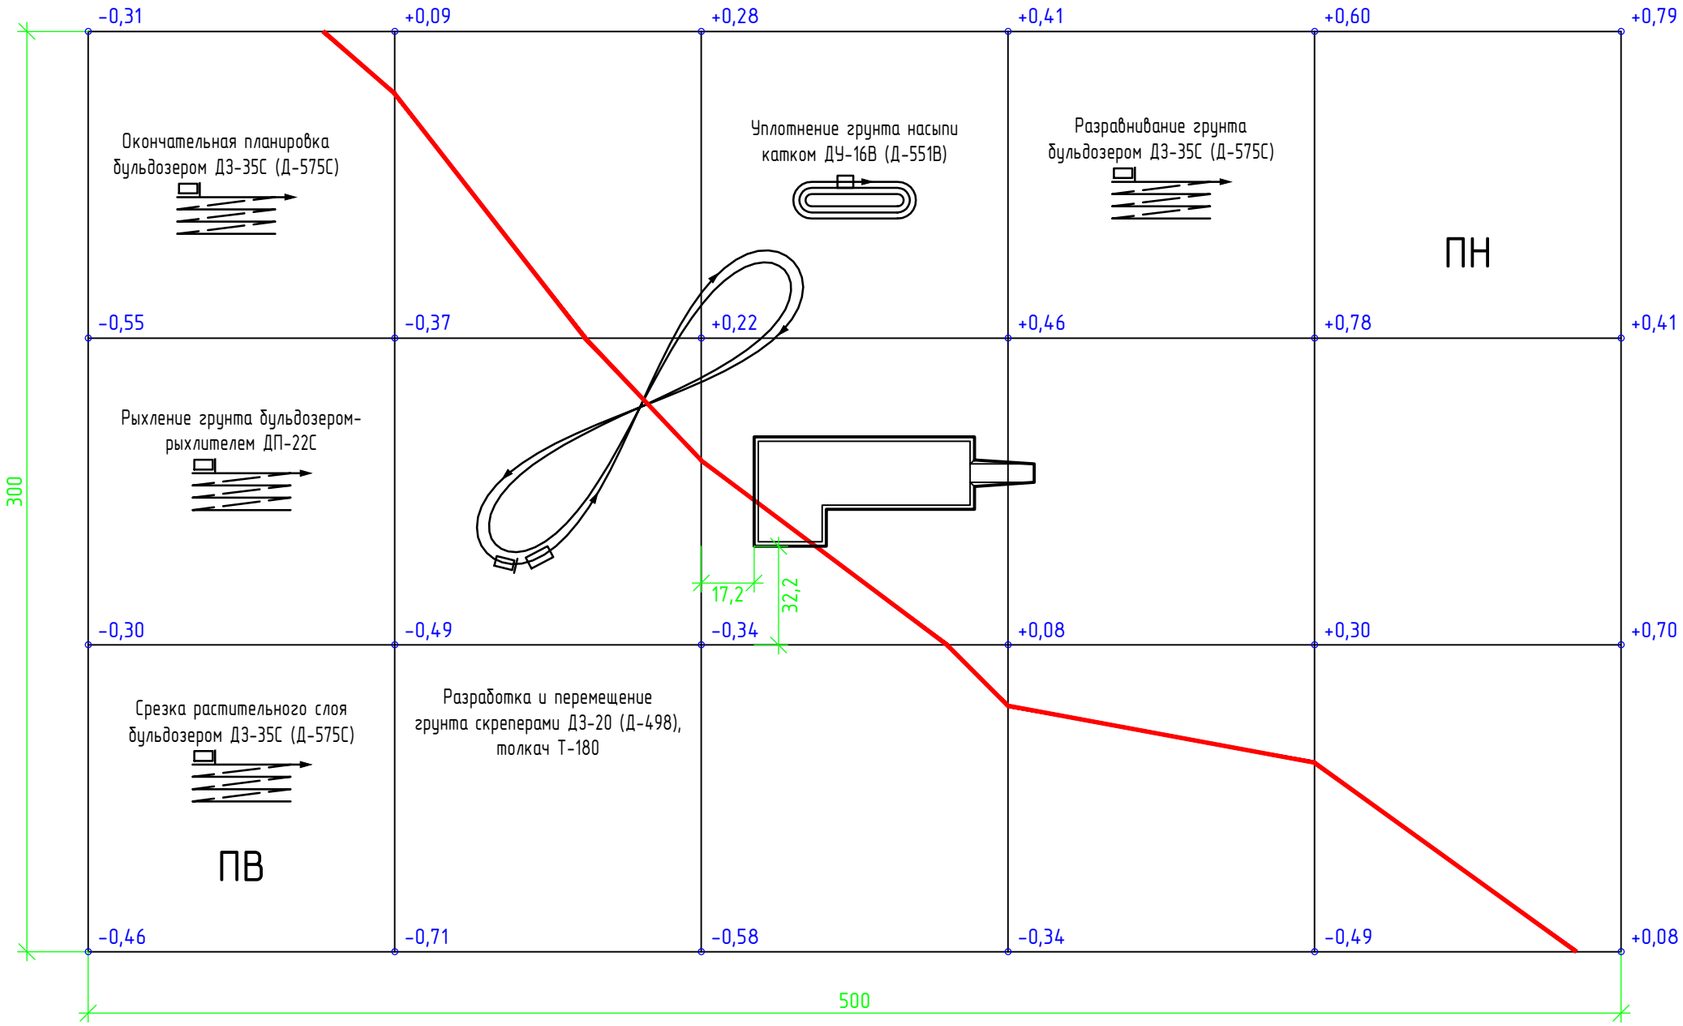

Ведомость применяемой техники

Наименование	Марка	Кол.	Технические характеристики
Скрепер прицепной	ДЗ-20 (Д-498), Т-100	3	ковш 6,7 м³, захват 2,59 м, резание 0,3 м, слой 0,35 м, 79 кВт, 7 т
Трактор-толкач	Т-180	1	мощность 132 кВт (180 л.с.)
Бульдозер-рыхлитель	ДП-22С на ДЗ-35С, Т-180	1	3 зуба, рыхление до 0,5 м, ширина 1,67 м, 132 кВт
Бульдозер	ДЗ-35С (Д-575С), Т-180	1	отвал неповоротный 3,64 х 1,29 м, 132 кВт, оборудование 3,4 т
Каток на пневмошинах	ДУ-16В (Д-551В)	1	полуприцепной, полоса 2,6 м, слой до 0,35 м, 177 кВт, 25 т

Изм.	Кол.уч.	Лист	№док.	Подп.	Дата
Разработал		Буев Д.Р.			
Проверил		Забелина О.Б.			
Т. контр.					
Н. контр.					
Утв.					

НИУ МГСУ 08.05.01 – КР – 2026

Разработка технологической карты на производство земляных работ. Вариант 2, грунт – супесь

Графическая часть курсовой работы	Стадия	Лист	Листов
	У	5	

Схема производства работ по вертикальной планировке М 1:2000

Кафедра технологии и организации строительного производства