


Схема обратной засыпки пазух котлована

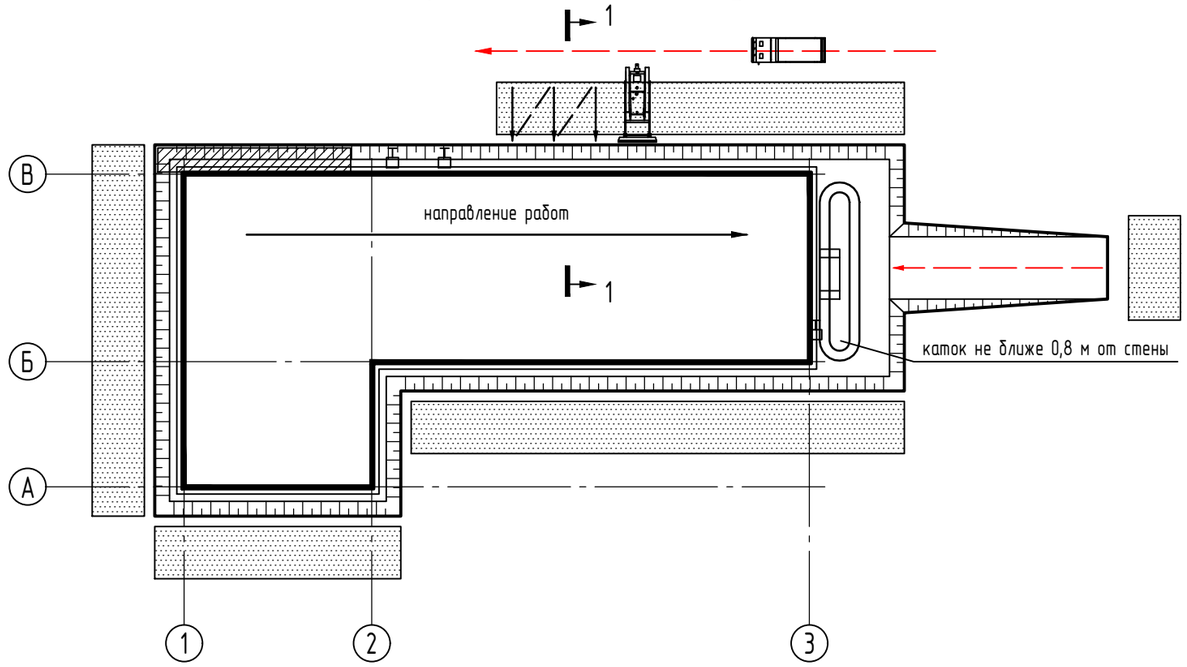


Разрез 1-1. Устройство резерва песка

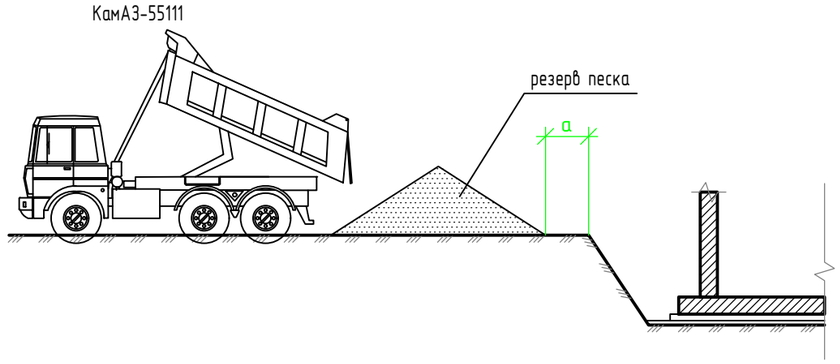

Разрез 1-1. Засыпка пазухи бульдозером

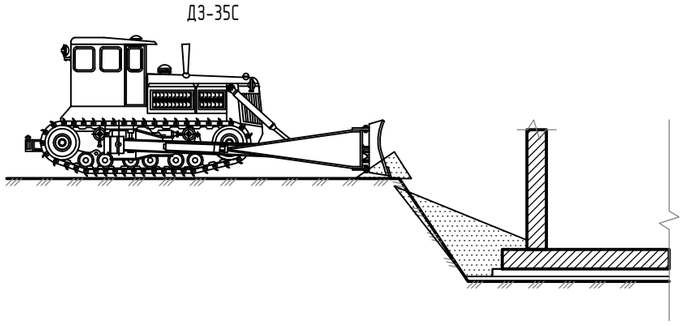

Разрез 1-1. Уплотнение слоев электротрамбовками

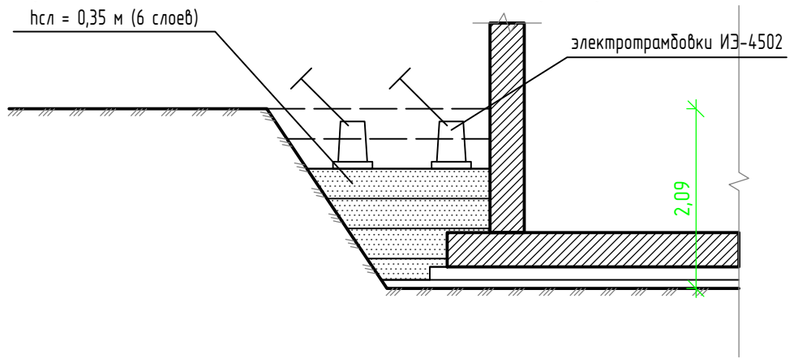

Условные обозначения

- резерв песка
- пазуха засыпана и уплотнена
- ось движения автосамосвалов
- рабочий и холостой ход бульдозера
- проходы катка
- уплотнение электротрамбовкой

Примечания

1. Обратная засыпка пазух ведется после устройства подземной части здания привозным песком: объем пазух 953,30 м³, песка в плотном теле 916,64 м³ (табл. 3).
2. Песок завозится автосамосвалами КамАЗ-55111 в резерв вдоль бровки котлована за призмой обрушения (а); в широкую зону у съезда - по съезду.
3. Песок сдвигается в пазуху бульдозером ДЗ-35С, разравнивается вручную и уплотняется электротрамбовками ИЗ-4502 слоями 0,35 м (6 слоев, глубина уплотнения ИЗ-4502 - 0,4 м); в зоне у съезда не ближе 0,8 м от стены - катком ДУ-31А.
4. Съезд засыпается последним тоже привозным песком (134,87 м³): автосамосвалы разгружаются на съезде, бульдозер разравнивает, каток ДУ-31А уплотняет послойно.

Ведомость машин и механизмов

Наименование	Марка	Кол.	Технические характеристики
Автосамосвал	КамАЗ-55111	5	кузов 6,6 м³, грузоподъемность 13 т
Бульдозер	ДЗ-35С (Д-575С), Т-180	1	отвал неповоротный 3,64 х 1,29 м, 132 кВт
Электротрамбовка	ИЗ-4502	2	уплотнение на 0,4 м за 2 прохода, башмак 350 х 450 мм, 0,4 кВт, 81,5 кг
Каток на пневмошинах	ДУ-31А (Д-627А)	1	самоходный, полоса 1,9 м, слой до 0,35 м, 66 кВт, 16 т

Изм.	Кол.уч.	Лист	№док.	Подп.	Дата
Разработал		Буев Д.Р.			
Проверил		Забелина О.Б.			
Т. контр.					
Н. контр.					
Утв.					

НИУ МГСУ 08.05.01 - КР - 2026

Разработка технологической карты на производство земляных работ. Вариант 2, грунт - супесь

Графическая часть курсовой работы	Стадия	Лист	Листов
	У	7	

Технологическая схема производства работ по обратной засыпке

Кафедра технологии и организации строительного производства