
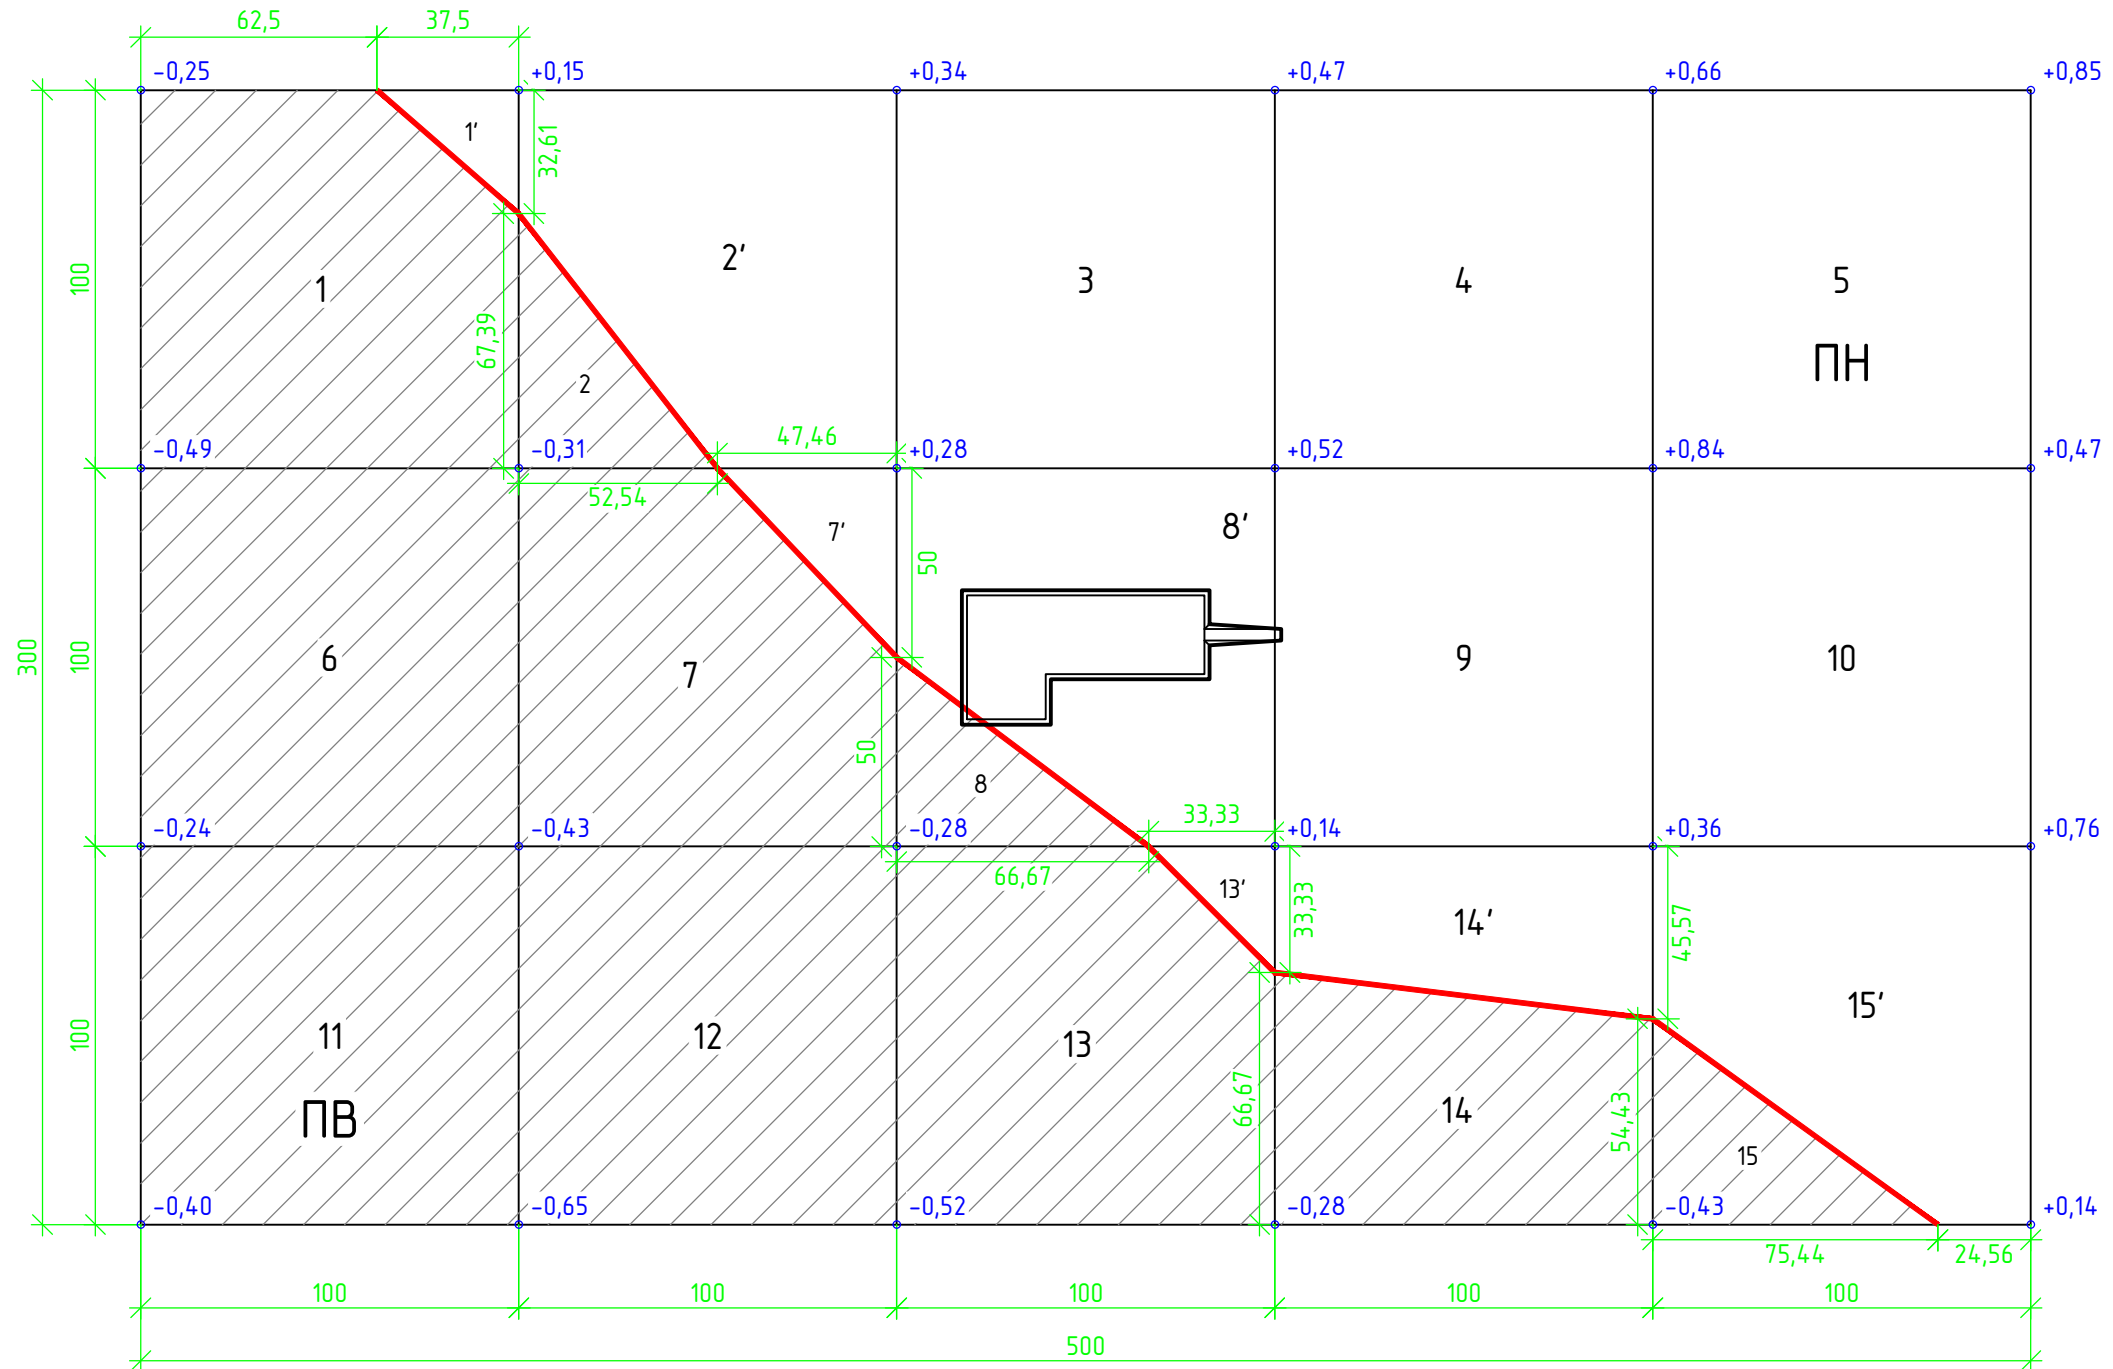
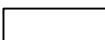


План строительной площадки с рабочими отметками и линией нулевых работ М 1:2000

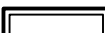

Условные обозначения

-  - линия нулевых работ (ЛНР)
-  - ПВ - планировочная выемка
-  - ПН - планировочная насыпь
-  - рабочая отметка, м (+ насыпь, - выемка)
-  - номер фигуры; со штрихом - насыпная часть квадрата
-  - расстояние до точки нулевых работ, м
-  - контур котлована

Объемы плановочных работ

	F, м ²	V, м ³
Выемка ПВ	69 191,63	20 209,47
Насыпь ПН	80 808,37	33 543,96
ПН / Кор, Кор = 1,04		32 253,81

						НИУ МГСУ 08.05.01 – КР – 2026				
						Разработка технологической карты на производство земляных работ. Вариант 2, грунт – супесь				
Изм.	Кол.уч.	Лист	№ док.	Подп.	Дата	Графическая часть курсовой работы		Стадия	Лист	Листов
Разработал	Бувёв Д.Р.				У			1	4	
Проверил	Забелина О.Б.									
Т. контр.										
						План строительной площадки с рабочими отметками и ЛНР М 1:2000		Кафедра технологий и организации строительного производства		
Н. контр.										
Умб.										