


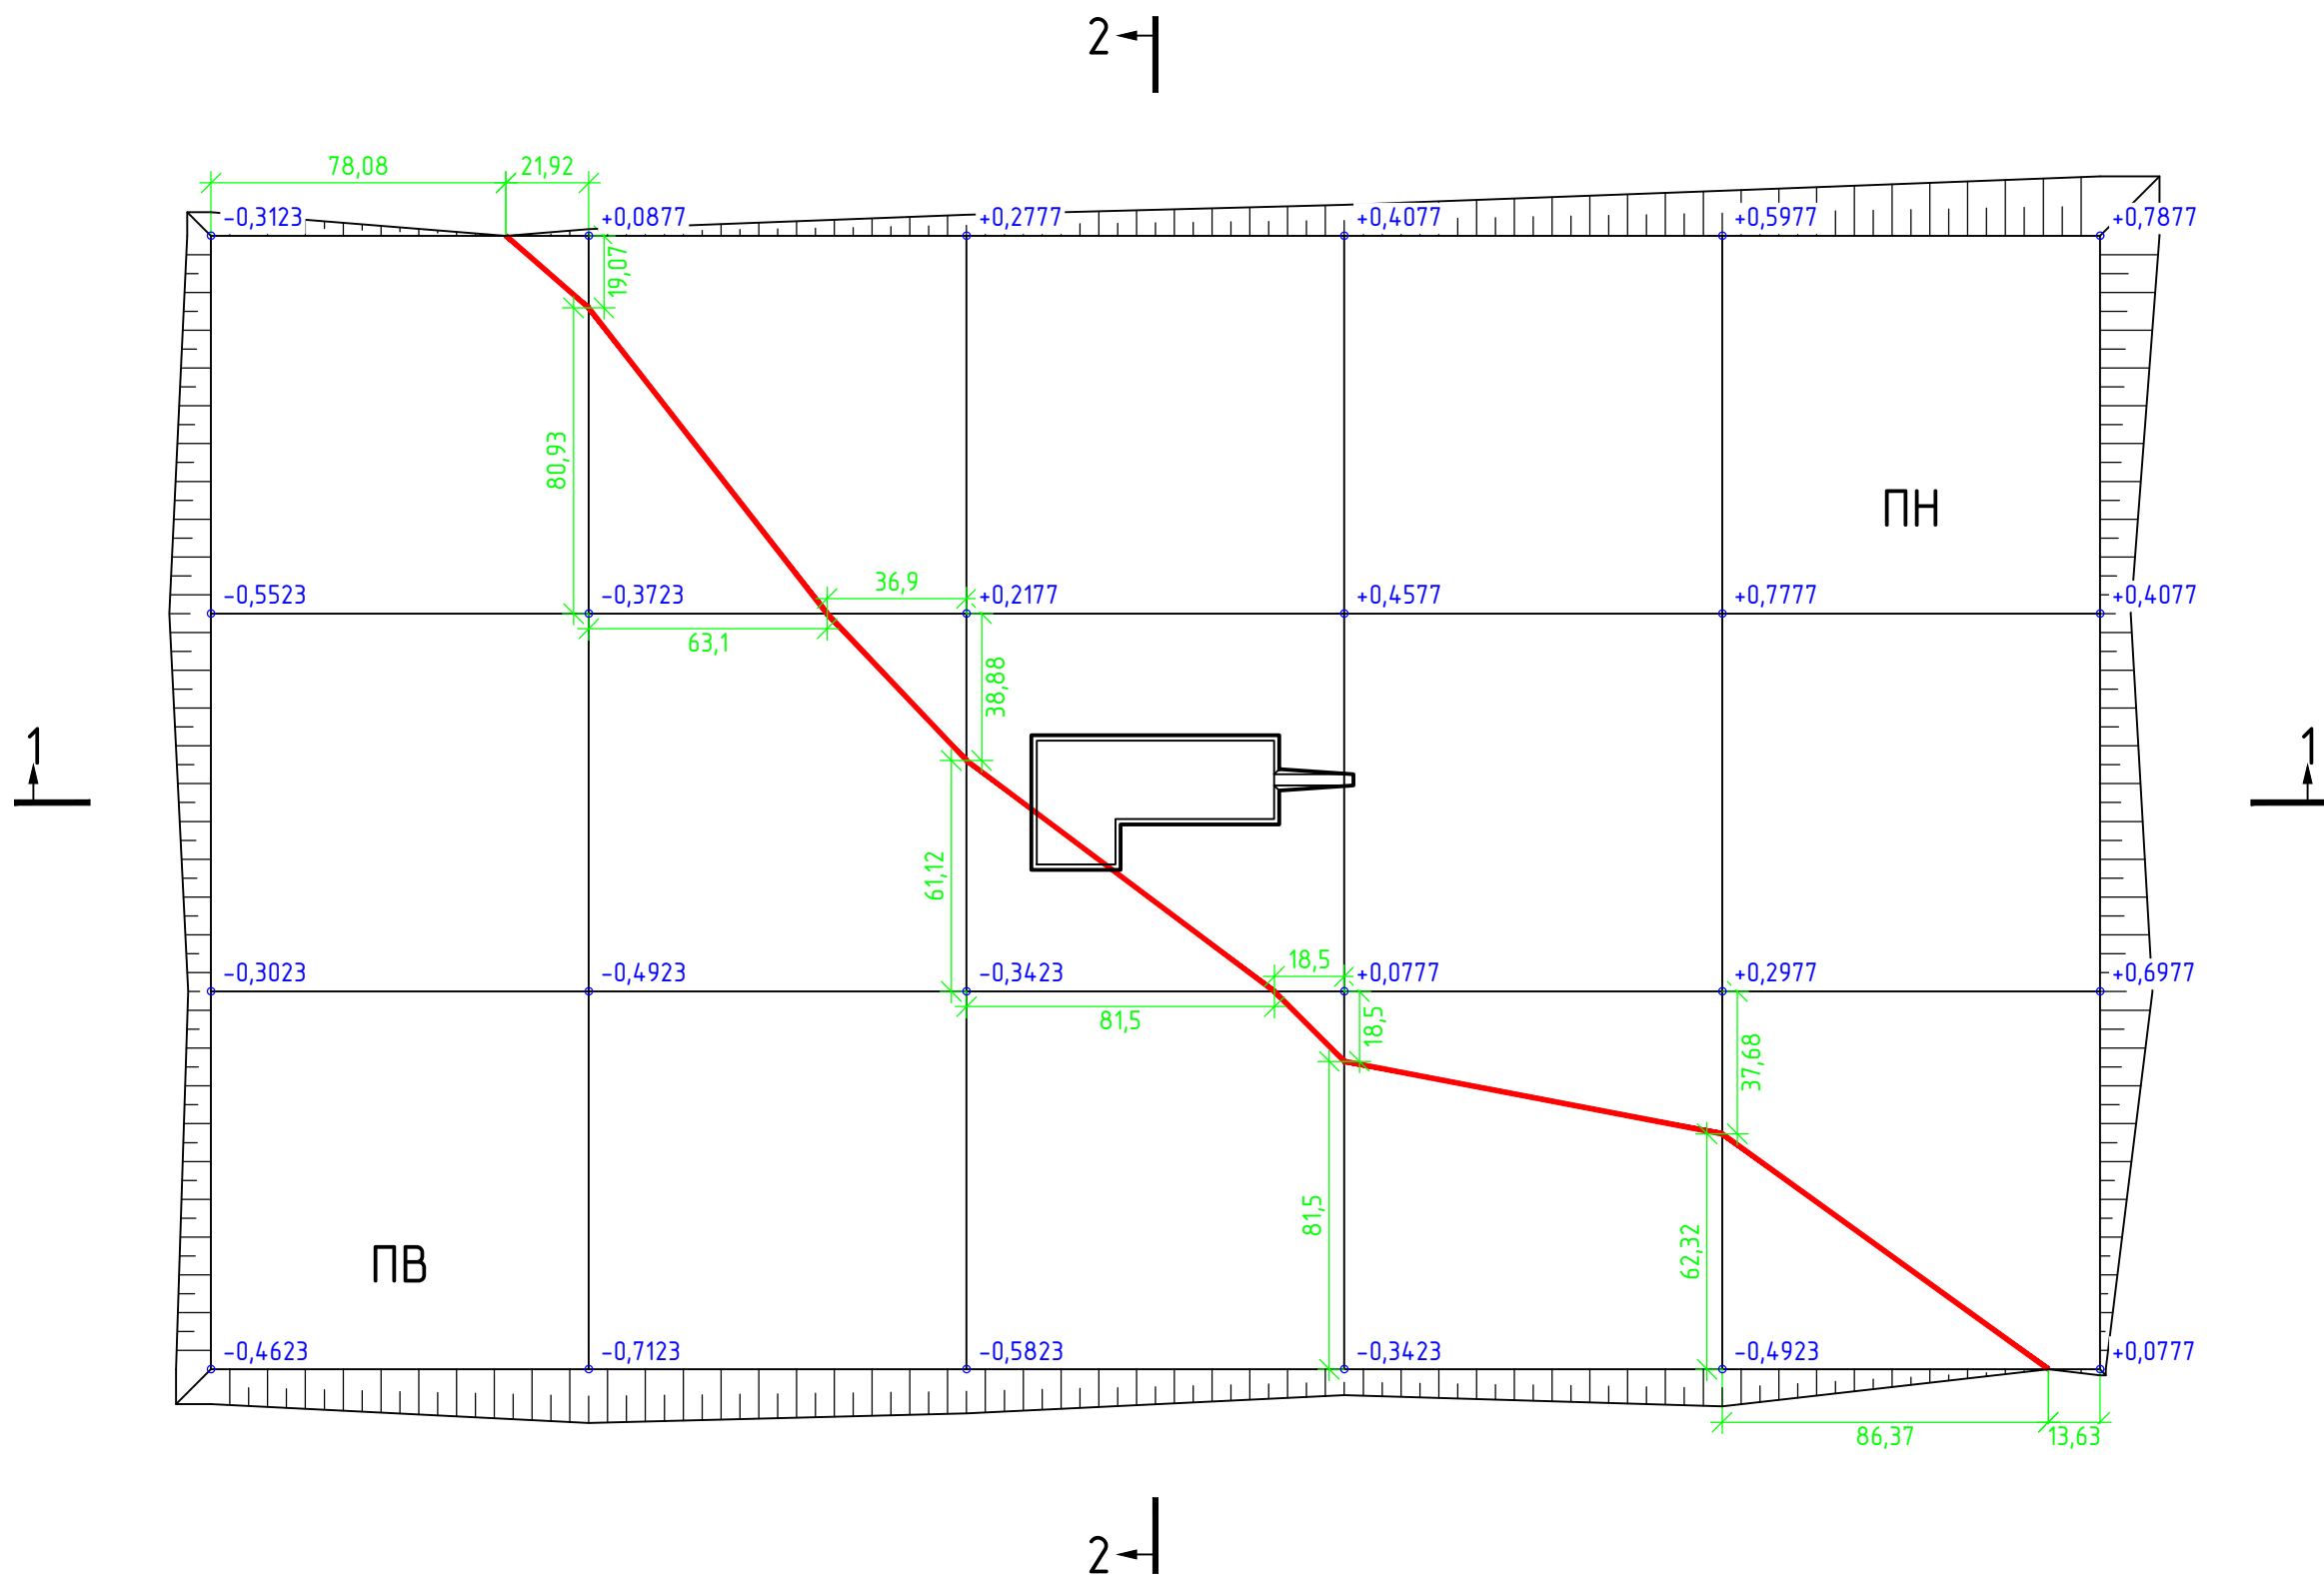

						НИУ МГСУ 08.05.01 – КР – 2026			
						Разработка технологической карты на производство земляных работ. Вариант 2, грунт – супесь			
Изм.	Кол.уч.	Лист	№ док.	Подп.	Дата	Графическая часть курсовой работы	Стадия	Лист	Листов
Разработал	Буев Д.Р.						У	2	
Проверил	Забелина О.Б.								
Т. контр.						План площадки с окончательными рабочими отметками и обводами Мз 1:2000, Мв 1:100	Кафедра технологий и организации строительного производства		
Н. контр.									
Утв.									