


Картограмма перемещения земляных масс М 1:2000

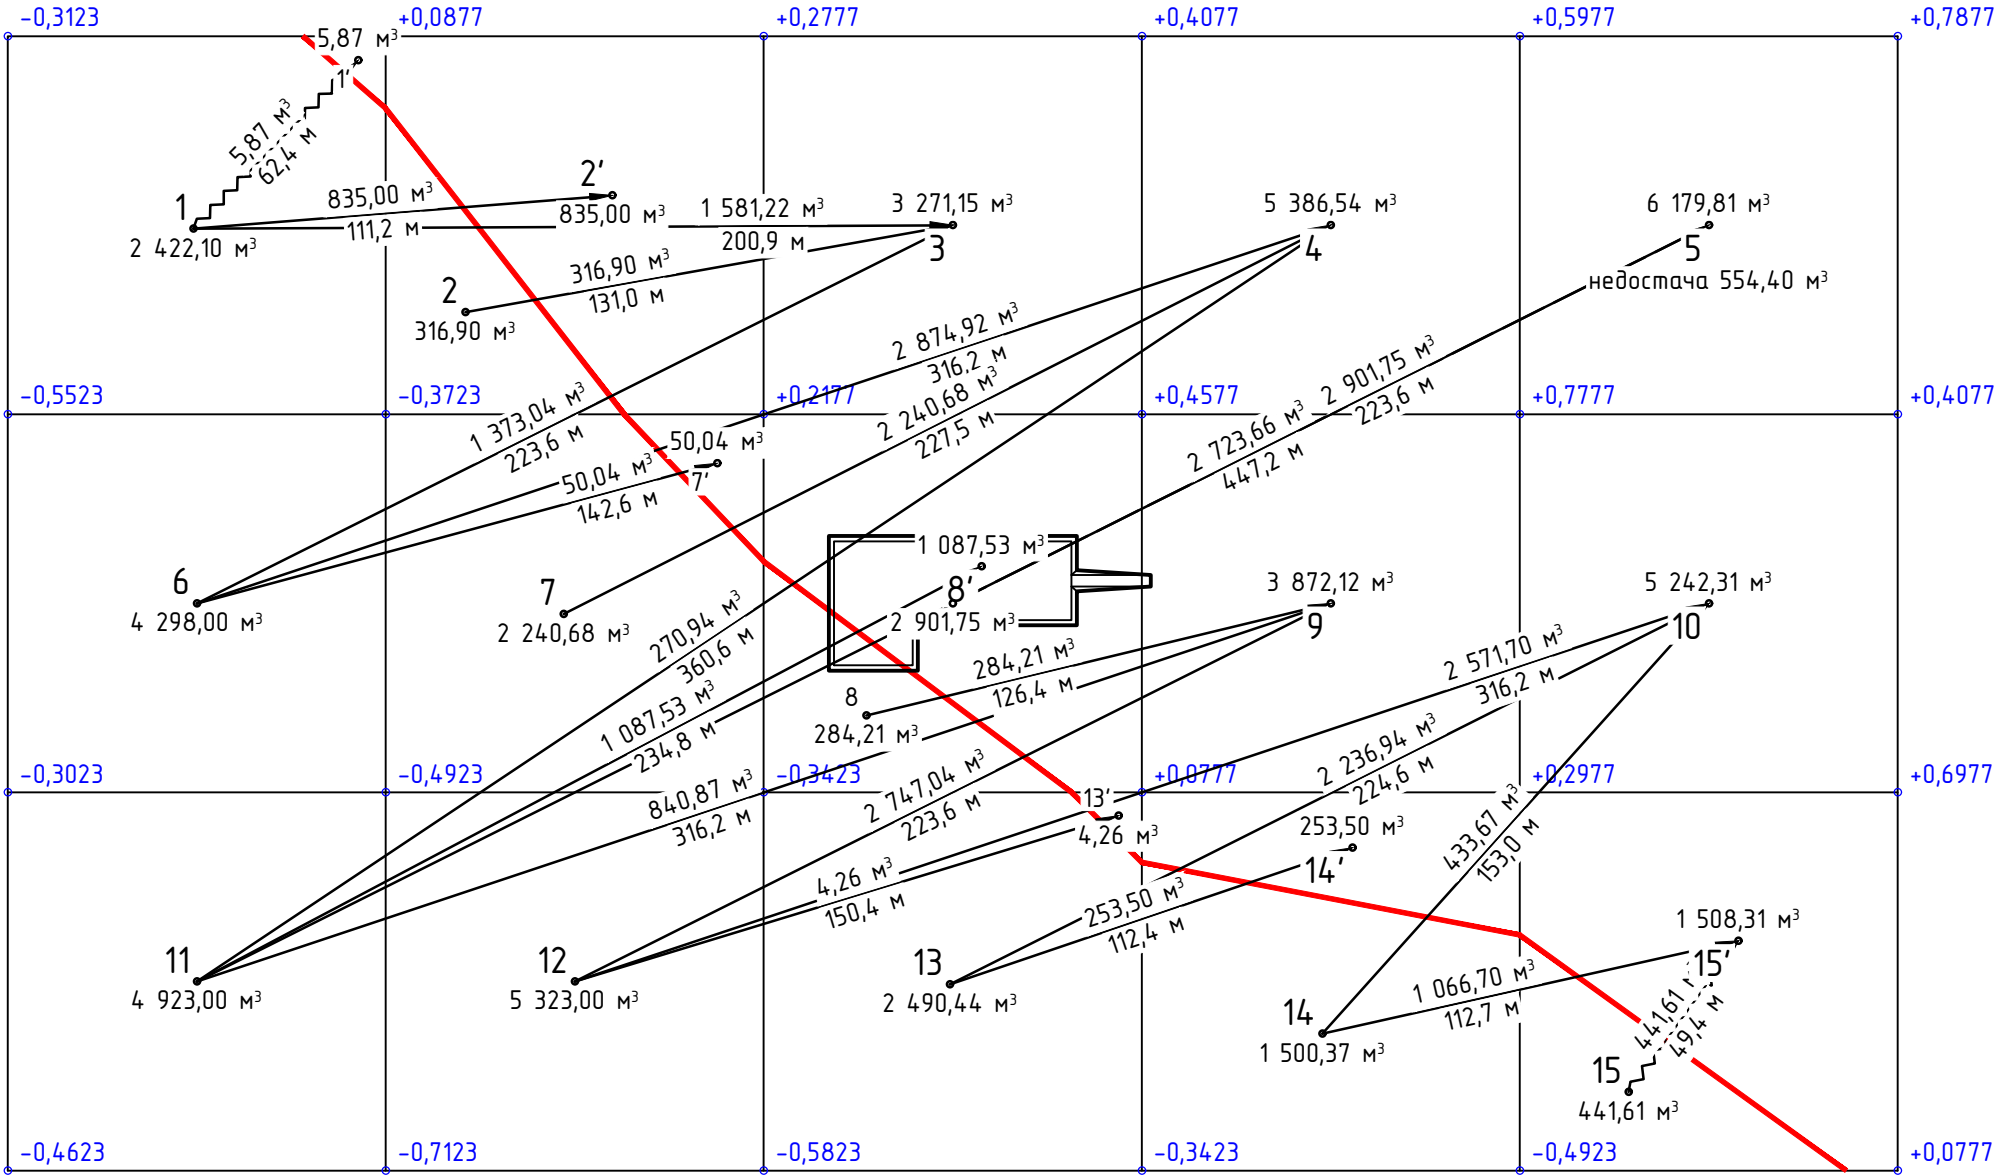

Условные обозначения

- Грунт перемещается:
- - скрепером
  - - бульдозером
  - - самосвалом

|            |               |      |        |       |      |                                                                                            |                                                             |      |
|------------|---------------|------|--------|-------|------|--------------------------------------------------------------------------------------------|-------------------------------------------------------------|------|
|            |               |      |        |       |      | НИУ МГСУ 08.05.01 – КР – 2026                                                              |                                                             |      |
|            |               |      |        |       |      | Разработка технологической карты на производство земляных работ. Вариант 2, грунт – супесь |                                                             |      |
| Изм.       | Кол.уч.       | Лист | № док. | Подп. | Дата | Графическая часть курсовой работы                                                          | Стадия                                                      | Лист |
| Разработал | Бувёв Д.Р.    |      |        |       |      |                                                                                            | У                                                           | 4    |
| Проверил   | Забелина О.Б. |      |        |       |      | Картограмма перемещения земляных масс М 1:2000                                             | Кафедра технологий и организации строительного производства |      |
| Т. контр.  |               |      |        |       |      |                                                                                            |                                                             |      |
| Н. контр.  |               |      |        |       |      |                                                                                            |                                                             |      |
| Утв.       |               |      |        |       |      |                                                                                            |                                                             |      |