План строительной площадки с рабочими отметками и линией нулевых работ М 1:2000

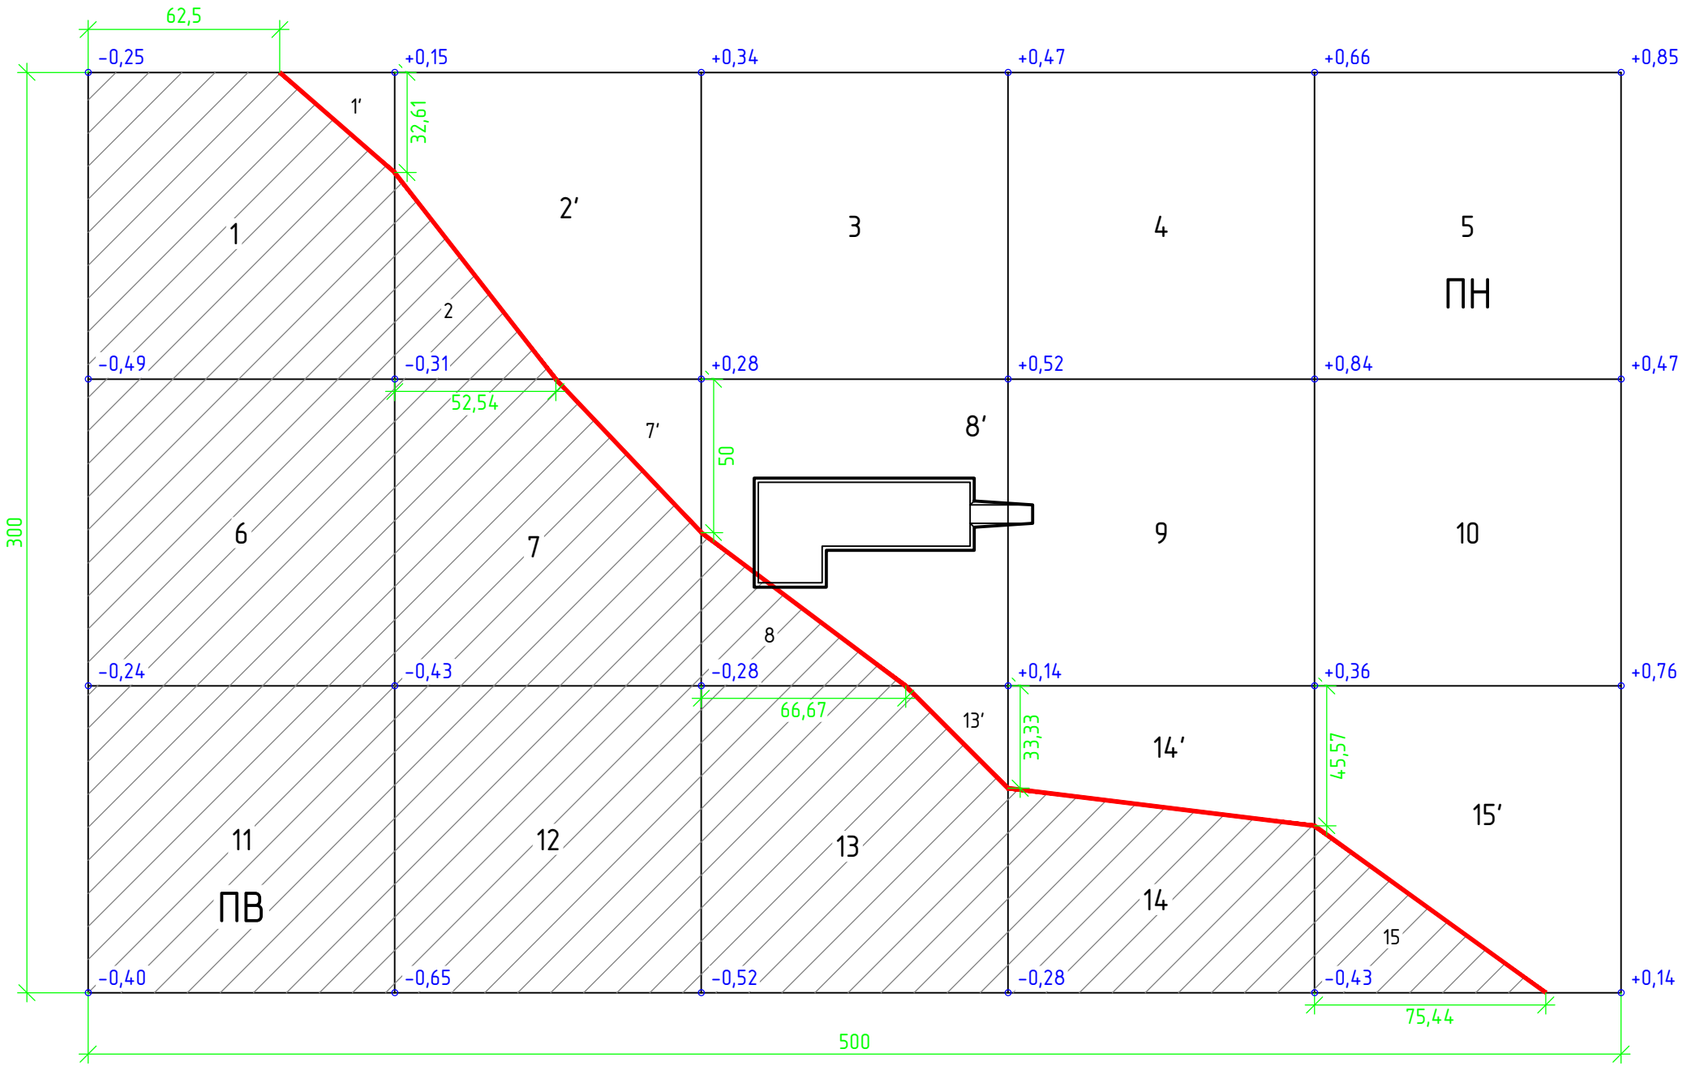

Условные обозначения

- линия нулевых работ (ЛНР)
- ПВ – планировочная выемка
- ПН – планировочная насыпь
- +0,15 – рабочая отметка, м (+ насыпь, – выемка)
- 7′ – номер фигуры; со штрихом – насыпная часть квадрата
- 37,5 – расстояние до точки нулевых работ, м
- контур котлована

Объемы планировочных работ

	F, м²	V, м³
Выемка ПВ	69 191,63	20 209,47
Насыпь ПН	80 808,37	33 543,96
ПН / Кор, Кор = 1,04		32 253,81

Изм.	Кол.уч.	Лист	№док.	Подп.	Дата
Разработал		Буев Д.Р.			
Проверил		Забелина О.Б.			
Т. контр.					
Н. контр.					
Утв.					

НИУ МГСУ 08.05.01 – КР – 2026

Разработка технологической карты на производство земляных работ. Вариант 2, грунт – супесь

Графическая часть курсовой работы	Стадия	Лист	Листов
	У	1	8

План строительной площадки с рабочими отметками и ЛНР М 1:2000

Кафедра технологии и организации строительного производства