

План типового этажа. Система К1 (1 : 100)

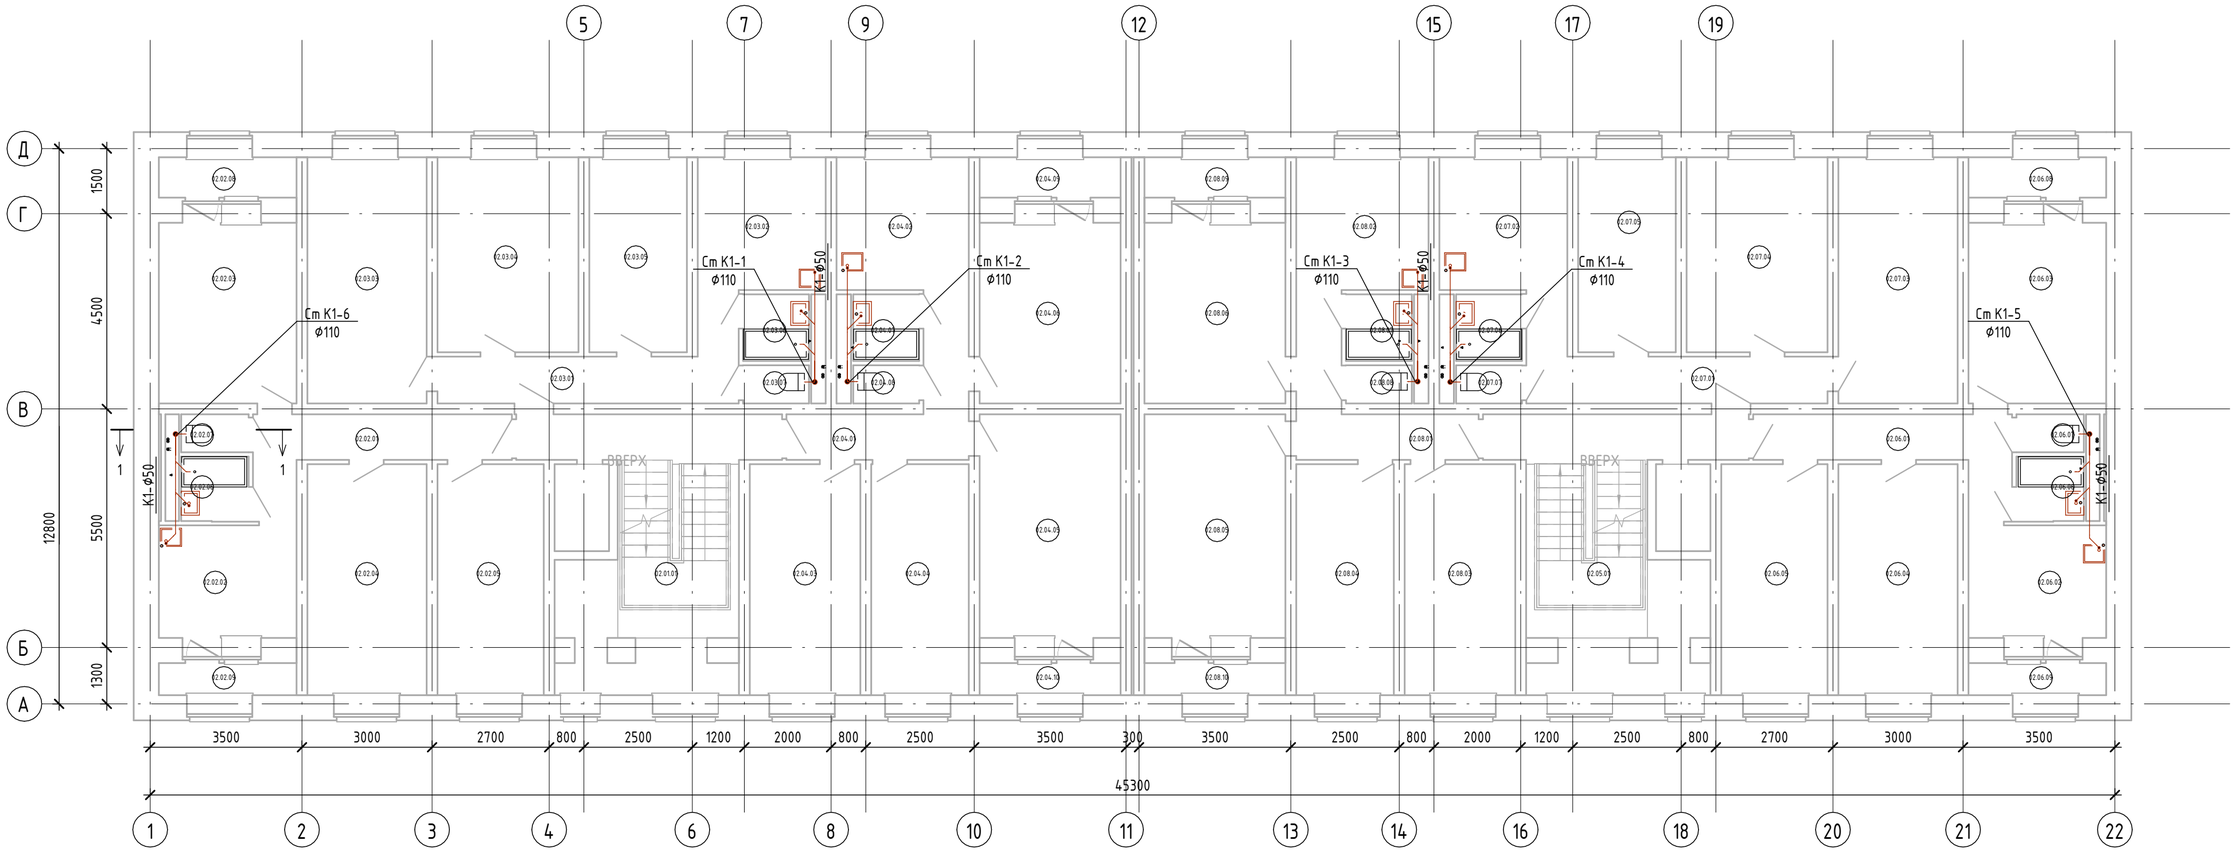

Разрез 1–1 по шахте кв. А (1 : 50)

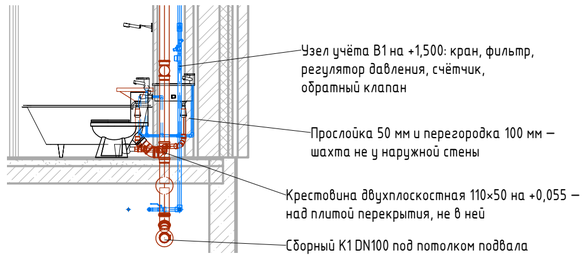

Примечания:
1. Планы и схемы систем рассматривать совместно.
2. Монтаж трубопроводов производить с учетом прокладки смежных систем.
3. Отметки трубопроводов даны по лотку трубы.
4. Отметки трубопроводов и оборудования даны относительно нуля здания.
5. Привязки и отметки трубопроводов уточнять по месту.

Изм.	Кол.уч.	Лист	№док.	Подп.	Дата
Разраб.		Буев			
Пров.					

НИУ МГСУ 08.03.01*-КП-2026 - ВК

Системы холодного водоснабжения и водоотведения здания

Наименование здания. Жилой дом. Вариант 3	Стадия	Лист	Листов
	У	4	7
План типового этажа. Система К1	НИУ МГСУ ИИЭСМ Кафедра ½Водоснабжение и водоотведение½		

Согласовано

Взам. инв. №

Подп. и дата

Инв. № подл.

Формат А2 420 x 594