

План типового этажа. Система К1 (1 : 100)

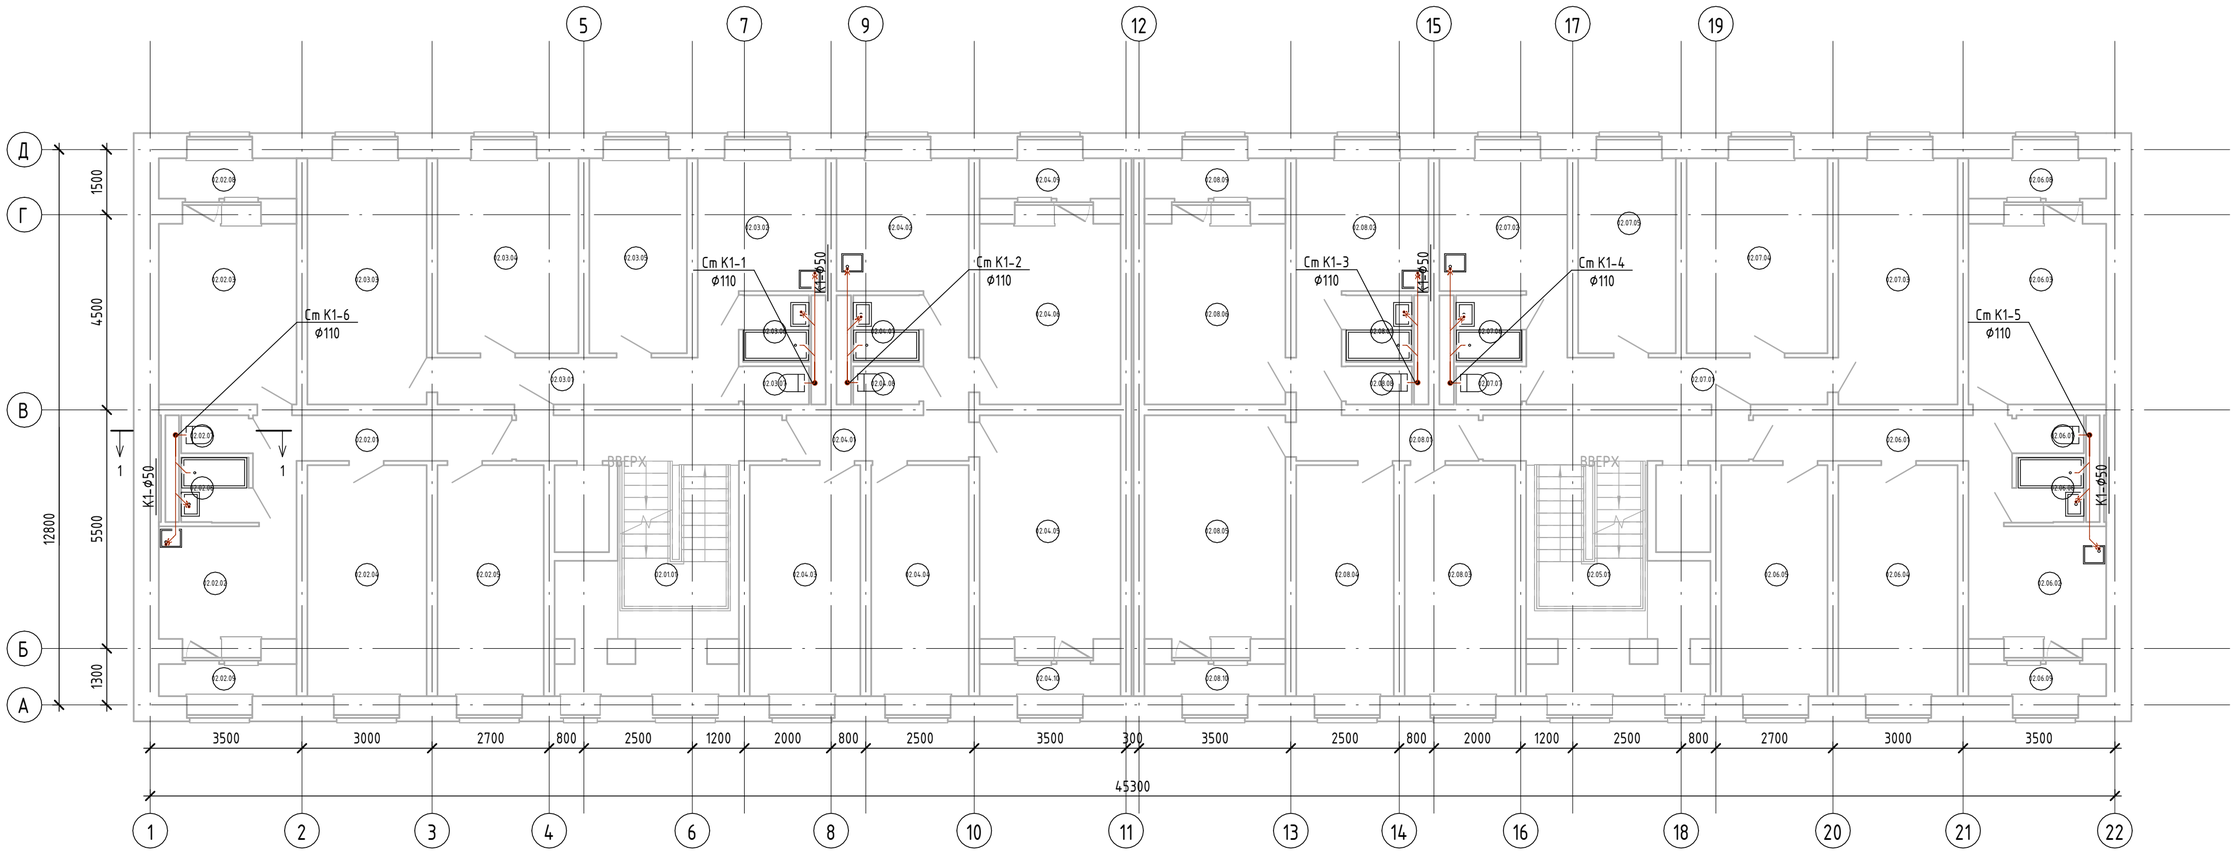

Разрез 1–1 по шахте кв. А (1 : 50)

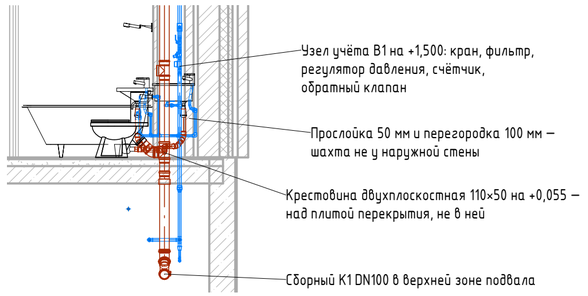

Примечания:
1. Планы и схемы систем рассматривать совместно.
2. Монтаж трубопроводов производить с учетом прокладки смежных систем.
3. Отметки трубопроводов даны по лотку трубы.
4. Отметки трубопроводов и оборудования даны относительно нуля здания.
5. Привязки и отметки трубопроводов уточнять по месту.
6. Напротив ревизий на стояках в коробах шахт предусмотреть люки не менее 0,3х0,4 м (СП 30.13330.2020, п. 18.9); ревизии ставить крышкой к люку.
7. В местах пересечения стен и перегородок трубопроводы прокладывать в гильзах; в перекрытиях – противопожарные муфты.
8. В подвале трубопроводы К1 – чугунные безраструбные SML (DIN EN 877), переход с полипропилена – муфтой HL у низа плиты; повороты – отводами не более 45^1, присоединения – косыми тройниками и двухплоскостными крестовинами (СП 30.13330.2020, п. 18.4, 18.5).

						НИУ МГСУ 08.03.01*-КП-2026 - ВК			
						Системы холодного водоснабжения и водоотведения здания			
Изм.	Кол.уч.	Лист	№док.	Подп.	Дата				
Разраб.		Буев				Наименование здания. Жилой дом. Вариант 3	Стадия	Лист	Листов
Пров.							У	4	7
						План типового этажа. Система К1	НИУ МГСУ ИИЭСМ Кафедра ½Водоснабжение и водоотведение½		

Согласовано

Взам. инв. №

Подп. и дата

Инв. № подл.

Формат А2 420 x 594