
# Аксонометрическая схема. Система В1

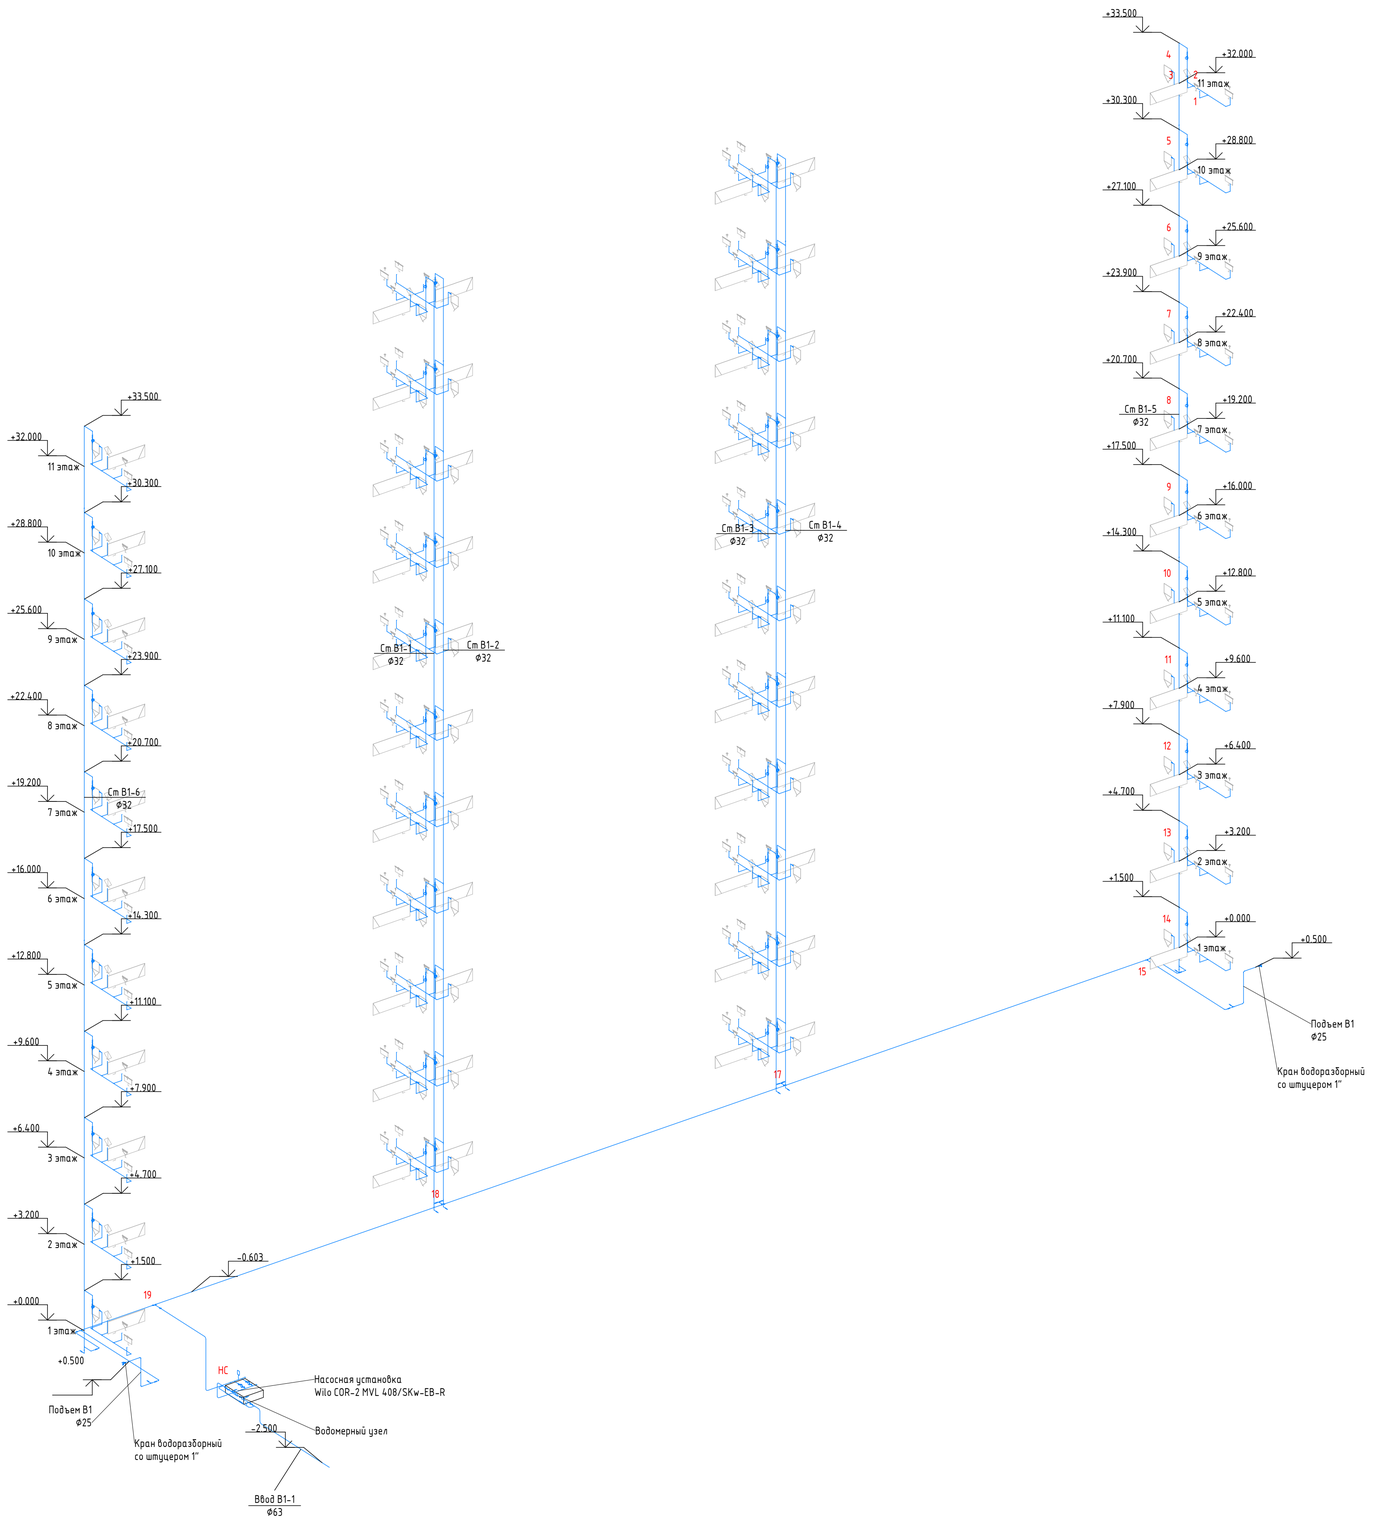


Примечания:
1. Планы и схемы систем рассматривать совместно.
2. Все трубопроводы систем водоснабжения, кроме подводок к санитарным приборам, покрываются теплоизоляцией во избежание теплопотерь и появления конденсата.
3. Трубопроводы прокладывать с уклоном 0,002 в сторону сливной арматуры или смесителей.
4. Монтаж трубопроводов производить с учетом прокладки смежных систем.
5. Отметки трубопроводов даны по оси трубы.
6. Отметки трубопроводов и оборудования даны относительно нуля здания.
7. Привязки и отметки трубопроводов уточнять по месту.
8. В местах пересечения стен, перегородок и перекрытий трубопроводы прокладывать в гильзах, зазор заполнить негорючим материалом (СП 30.13330.2020, п. 11.5).
9. Ввод пропустить через стену подвала под углом 90° с зазором 0,2 м вокруг трубы и заделкой эластичным водонепроницаемым материалом (СП 30.13330.2020, п. 8.8).

| | | | | | | | |
|---|---|---|---|---|---|---|---|
| | | | | | | НИУ МГСУ 08.03.01*-КП-2026 - ВК | |
| | | | | | | Системы холодного водоснабжения и водоотведения здания | |
| Изм. | Кол.уч. | Лист | №док. | Подп. | Дата | | |
| Разраб. | | Буев | | | | Наименование здания. Жилой дом. Вариант 3 | Стадия: У; Лист: 3; Листов: 7 |
| Пров. | | | | | | | |
| | | | | | | Аксонометрическая схема. Система В1 | НИУ МГСУ ИИЭСМ Кафедра "Водоснабжение и водоотведение" |

Согласовано

Взам. инв. №

Подп. и дата

Инв. № подл.

Формат А1 594 x 841