План подвала. Система В1 (1 : 100)

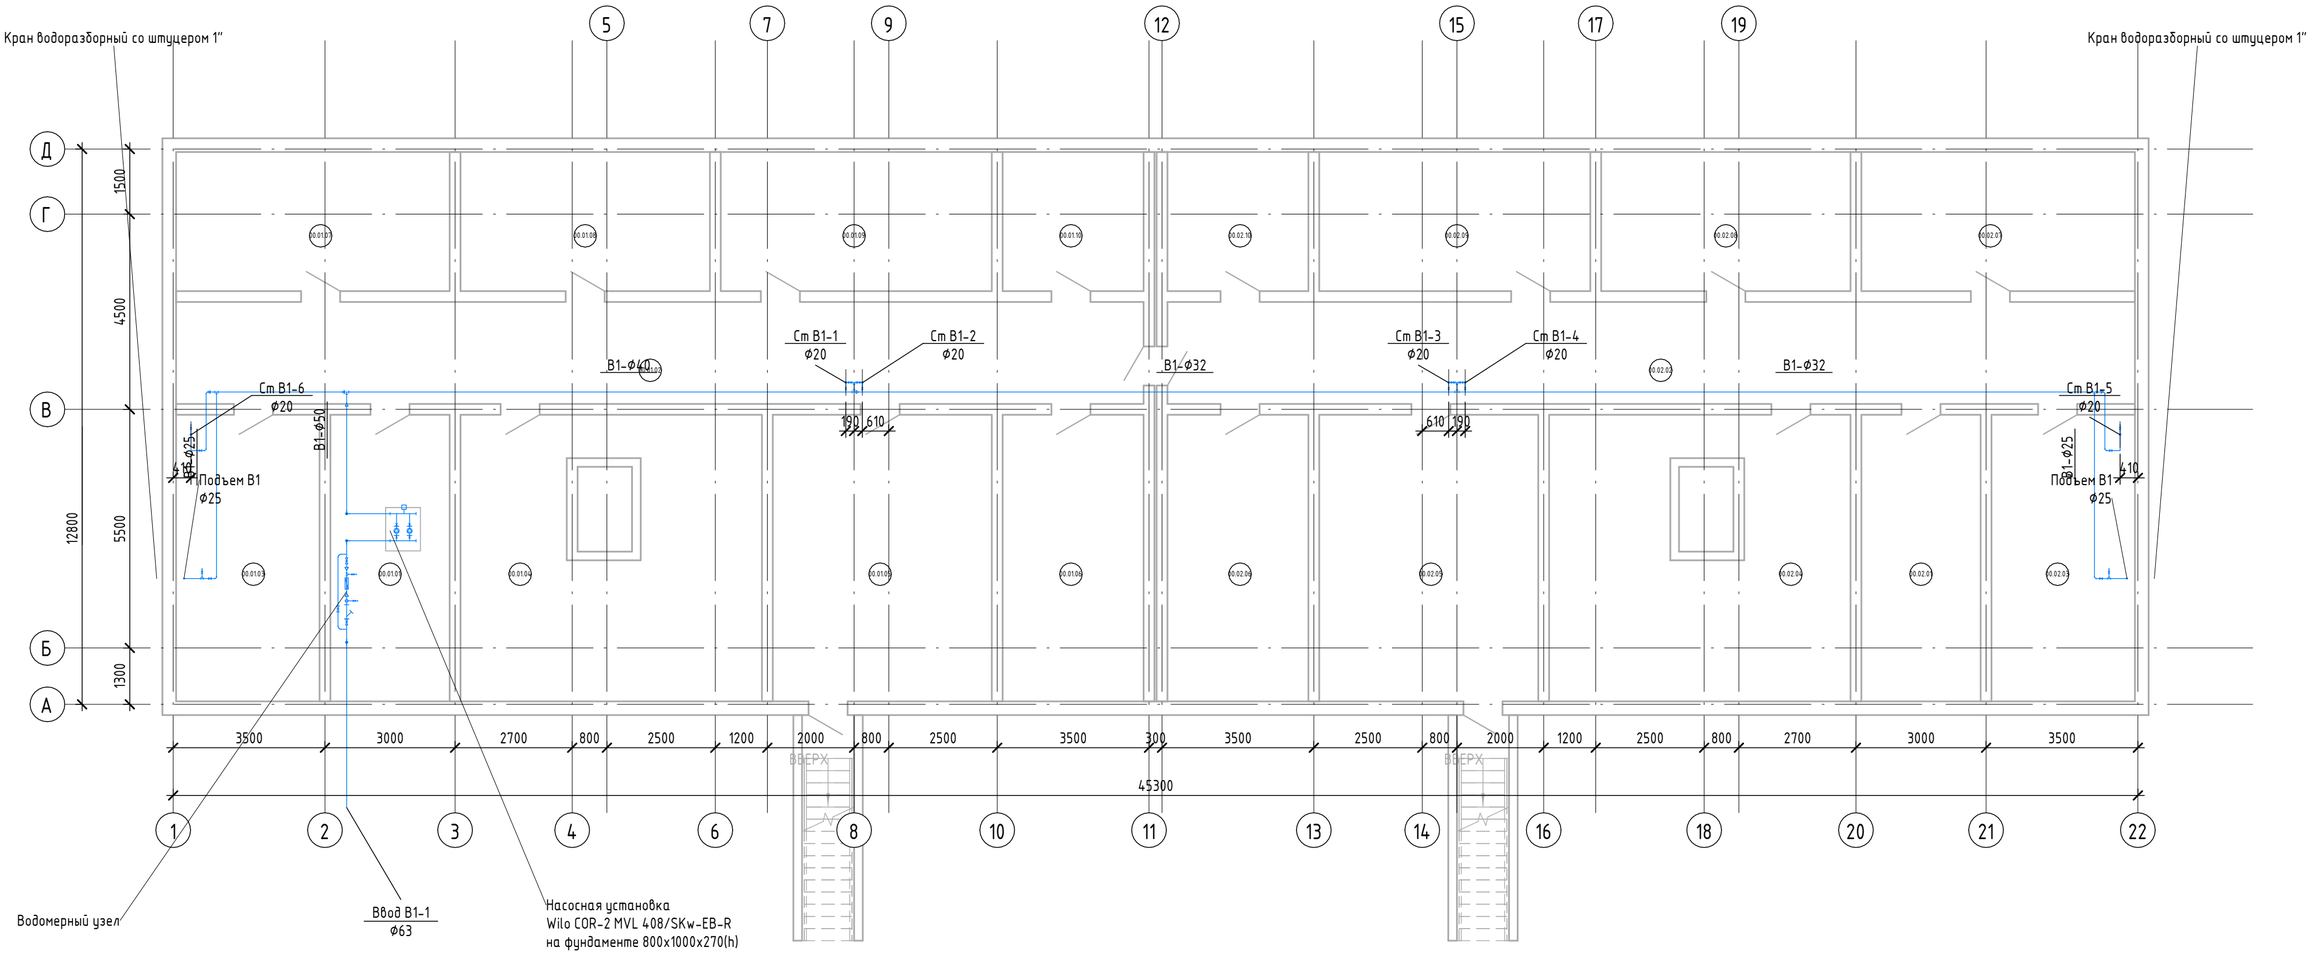

Примечания:
1. Планы и схемы систем рассматривать совместно.
2. Все трубопроводы систем водоснабжения, кроме подводок к санитарным приборам, покрываются теплоизоляцией во избежание теплопотерь и появления конденсата.
3. Трубопроводы прокладывать с уклоном 0,002 в сторону сливной арматуры или смесителей.
4. Монтаж трубопроводов производить с учетом прокладки смежных систем.
5. Отметки трубопроводов даны по оси трубы.
6. Отметки трубопроводов и оборудования даны относительно нуля здания.
7. Привязки и отметки трубопроводов уточнять по месту.
8. В местах пересечения стен, перегородок и перекрытий трубопроводы прокладывать в гильзах, зазор заполнить негорючим материалом (СП 30.13330.2020, п. 11.5).
9. Ввод пропустить через стену подвала под углом 90° с зазором 0,2 м вокруг трубы и заделкой эластичным водонепроницаемым материалом

Изм.	Кол.уч.	Лист	№док.	Подп.	Дата
Разраб.		Буев			
Пров.					

НИУ МГСУ 08.03.01*-КП-2026 - ВК

Системы холодного водоснабжения и водоотведения здания

Наименование здания. Жилой дом. Вариант 3	Стадия	Лист	Листов
	У	2	7
План подвала. Система В1	НИУ МГСУ ИИЭСМ Кафедра ¼Водоснабжение и водоотведение½		

Согласовано

Взам. инв. №

Подп. и дата

Инв. № подл.

Формат А2 420 x 594