Генеральный план. Системы В1, К1 (1 : 500)

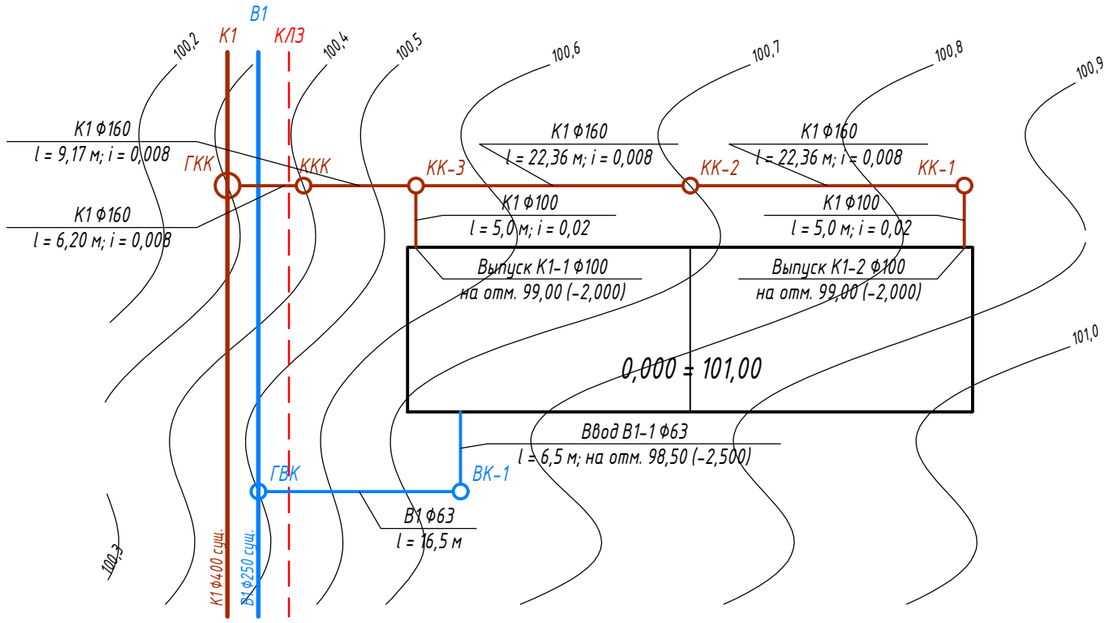

Примечания:

1. Отметки даны в метрах; 0,000 соответствует абсолютной отметке 101,00.

2. Горизонтали проведены через 0,1 м.

3. Дворовая сеть К1 — трубы гофрированные ПЭ ф160 SN8, колодцы — сборные железобетонные ф1000 мм.

4. Ввод В1 — ПЭ100 SDR17 ф63; глубина заложения не менее 2,2 м (промерзание 1,7 м + 0,5 м).

Изм.	Кол.уч.	Лист	№док.	Подп.	Дата	НИУ МГСУ 08.03.01*-КП-2026 - ВК		
						Системы холодного водоснабжения и водоотведения здания		
Разраб.						Наименование здания. Жилой дом. Вариант 3	Стадия: У	Лист: 8 / Листов: 8
Пров.								
						Генеральный план. Системы В1, К1	НИУ МГСУ ИИЭСМ Кафедра «Водоснабжение и водоотведение»	

Согласовано

Взам. инв. №

Подп. и дата

Инв. № подл.

Формат А3 297 x 420