


План строительной площадки с рабочими отметками и линией нулевых работ М 1:2000

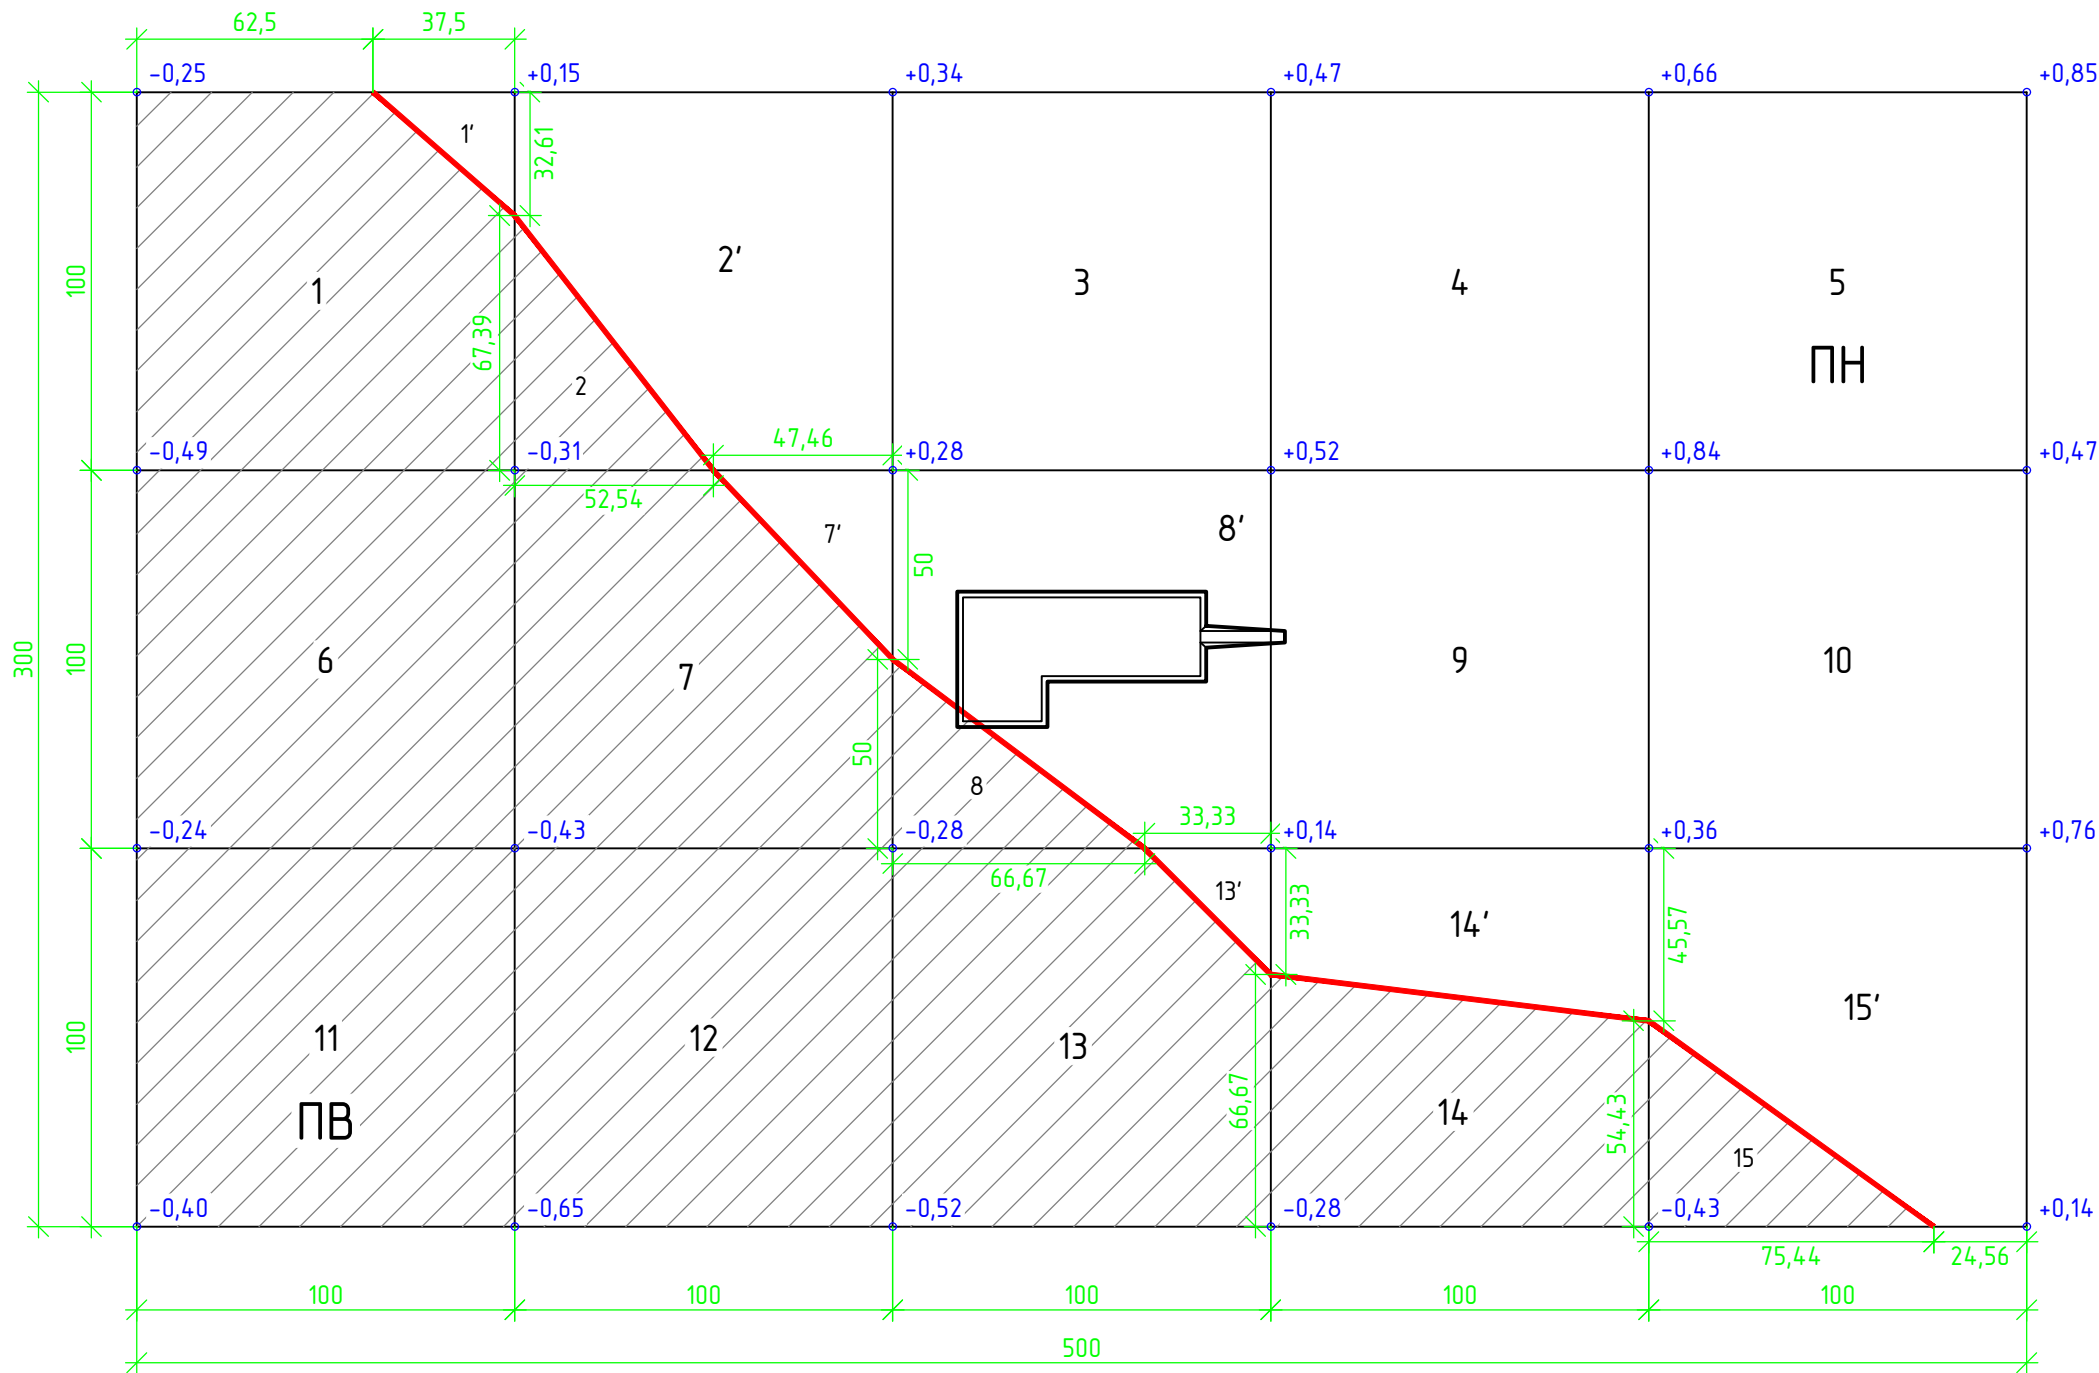

Условные обозначения

- линия нулевых работ (ЛНР)
- ▨ - ПВ - планировочная выемка
- - ПН - планировочная насыпь
- +0,15 - рабочая отметка, м (+ насыпь, - выемка)
- 7' - номер фигуры; со штрихом - насыпная часть квадрата
- 37,5 - расстояние до точки нулевых работ, м
- - контур котлована

Объемы планировочных работ


	Ф, м²	V, м³
Выемка ПВ	69 191,63	20 192,08
Насыпь ПН	80 808,37	33 522,02
ПН / Кор, Кор = 1,04		32 232,71

						НИУ МГСУ 08.05.01 - КР - 2026		
						Разработка технологической карты на производство земляных работ. Вариант 2, грунт - супесь		
Изм.	Кол.уч.	Лист	№ док.	Подп.	Дата	Графическая часть курсовой работы	Стадия	Лист
Разработал	Бувв Д.Р.						У	1
Проверил	Забелина О.Б.							2
Т. контр.						План строительной площадки с рабочими отметками и ЛНР М 1:2000	Кафедра технологий и организации строительного производства	
Н. контр.								
Утв.								

1 ←



A

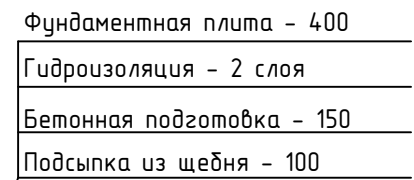

1. Размеры даны в миллиметрах, отметки - в метрах.
2. За отметку 0,000 принята проектная отметка планировки площадки.

						НИУ МГСУ 08.05.01 – КР – 2026					
						Разработка технологической карты на производство земляных работ. Вариант 2, грунт – супесь					
Изм.	Кол.уч.	Лист	№ док.	Подп.	Дата	Графическая часть курсовой работы			Стадия	Лист	Листов
Разработал	Бувф Д.Р.								У	2	
Проверил	Забелина О.Б.										
Т. контр.											
						План котлована М 1:500. Разрез 1-1 М 1:50			Кафедра технологий и организации строительного производства		
Н. контр.											
Утв.											