


План строительной площадки с рабочими отметками и линией нулевых работ М 1:2000

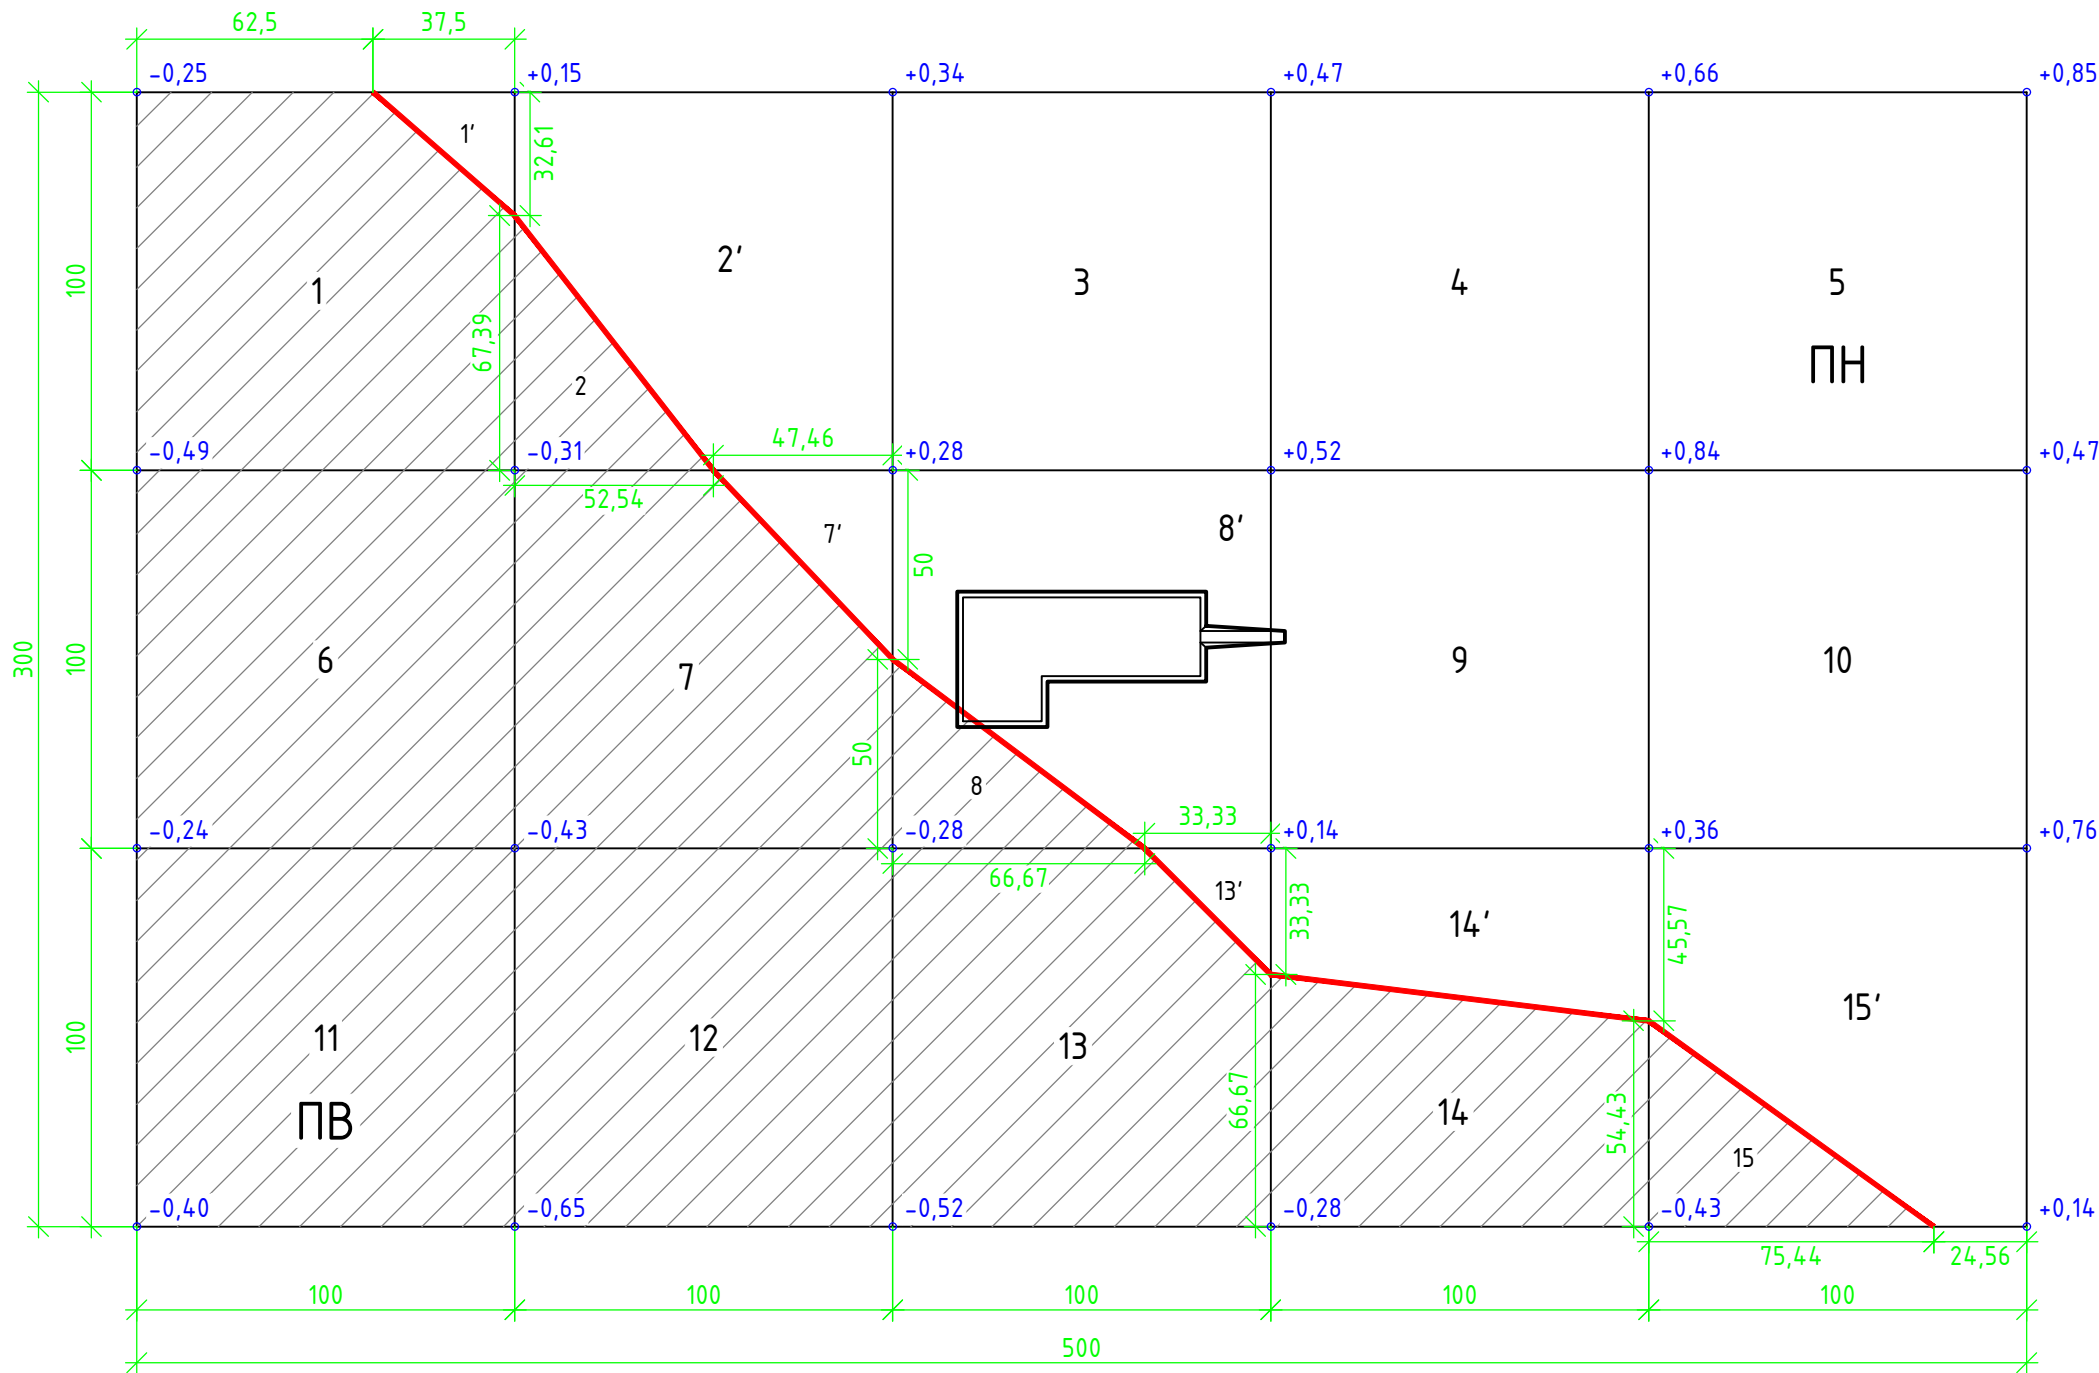

Условные обозначения


- линия нулевых работ (ЛНР)
- ▨ - ПВ - планировочная выемка
- - ПН - планировочная насыль
- +0,15 - рабочая отметка, м (+ насыль, - выемка)
- 7' - номер фигуры; со штрихом - насыпная часть квадрата
- 37,5 - расстояние до точки нулевых работ, м
- - контур котлована

Объемы планировочных работ


	Ф, м²	V, м³
Выемка ПВ	69 191,63	20 192,08
Насыль ПН	80 808,37	33 522,02
ПН / Кор, Кор = 1,04		32 232,71

						НИУ МГСУ 08.05.01 – КР – 2026			
						Разработка технологической карты на производство земляных работ. Вариант 2, грунт – супесь			
Изм.	Кол.уч.	Лист	№ док.	Подп.	Дата	Графическая часть курсовой работы	Стадия	Лист	Листов
Разработал	Бувв Д.Р.						У	1	2
Проверил	Забелина О.Б.								
Т. контр.						План строительной площадки с рабочими отметками и ЛНР М 1:2000	Кафедра технологий и организации строительного производства		
Н. контр.									
Утв.									

План котлована М 1:500

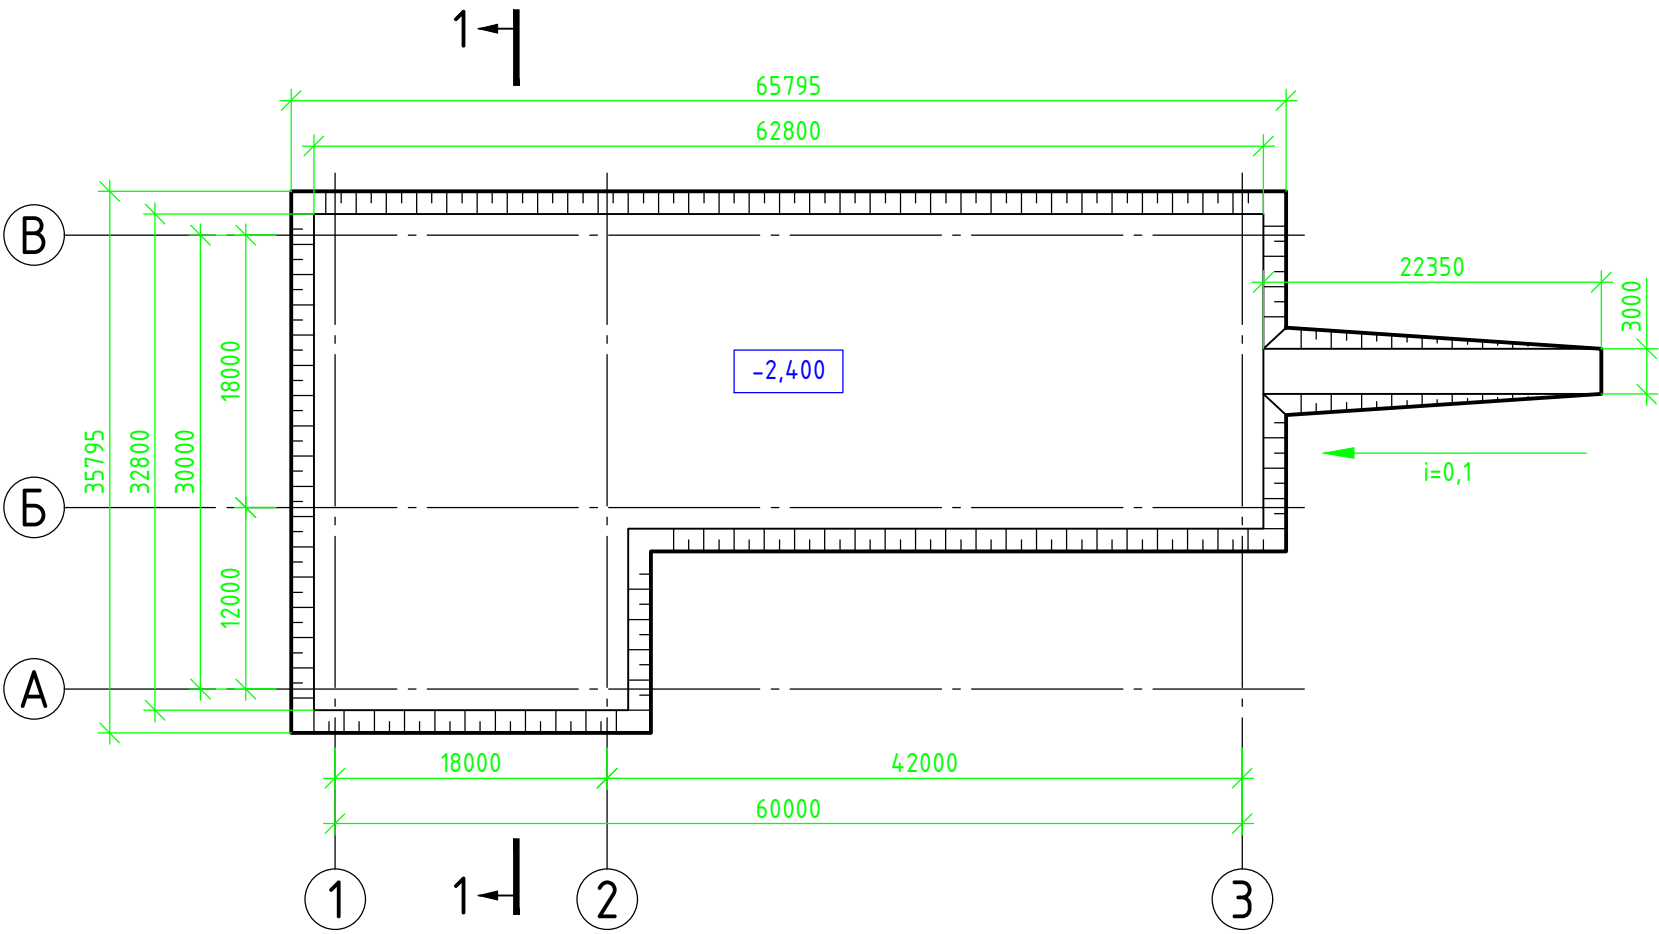

Разрез 1-1 М 1:50

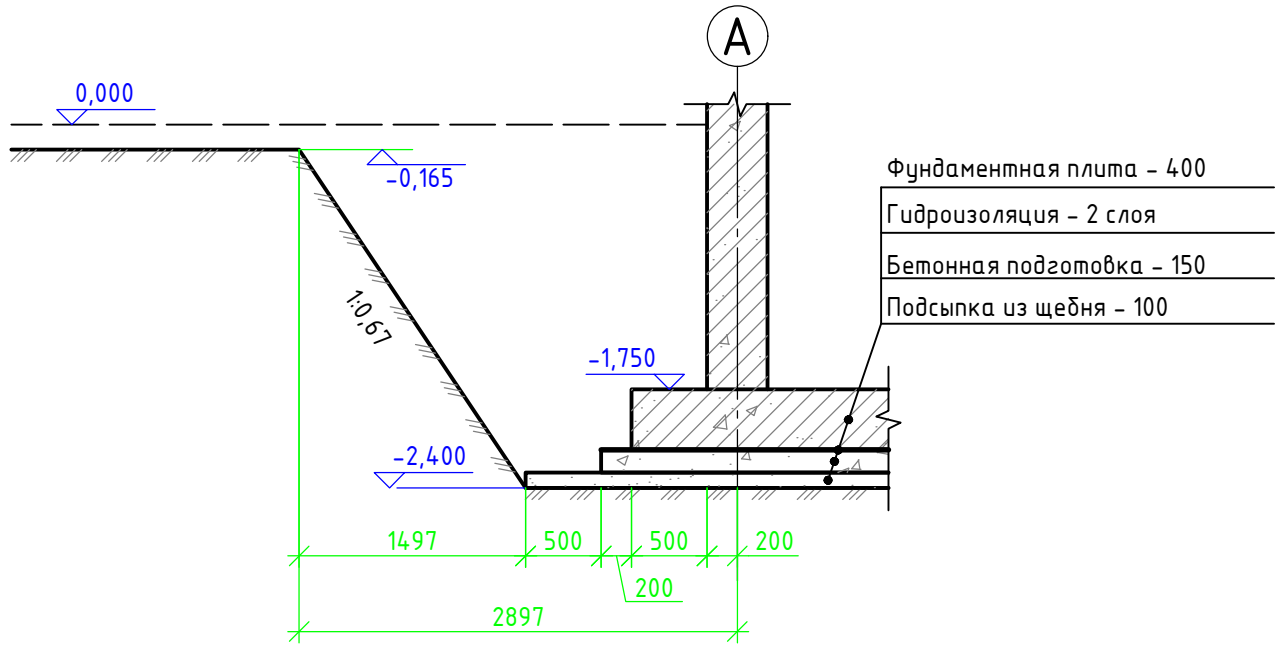

Объемы работ по котловану

Наименование работ	V, м³
Разработка грунта в котловане (с пандусом)	3 902,37
Устройство подсыпки из щебня	155,58
Устройство бетонной подготовки	219,19
Обратная засыпка пазух	846,54

1. Размеры даны в миллиметрах, отметки – в метрах.
2. За отметку 0,000 принята проектная отметка планировки площадки.

						НИУ МГСУ 08.05.01 – КР – 2026			
						Разработка технологической карты на производство земляных работ. Вариант 2, грунт – супесь			
Изм.	Кол.уч.	Лист	№ док.	Подп.	Дата	Графическая часть курсовой работы	Стадия	Лист	Листов
Разработал	Був Д.Р.						У	2	
Проверил	Забелина О.Б.								
Т. контр.									
						План котлована М 1:500. Разрез 1–1 М 1:50	Кафедра технологий и организации строительного производства		
Н. контр.									
Утв.									