# План подвала. Система К1 ( 1 : 100)

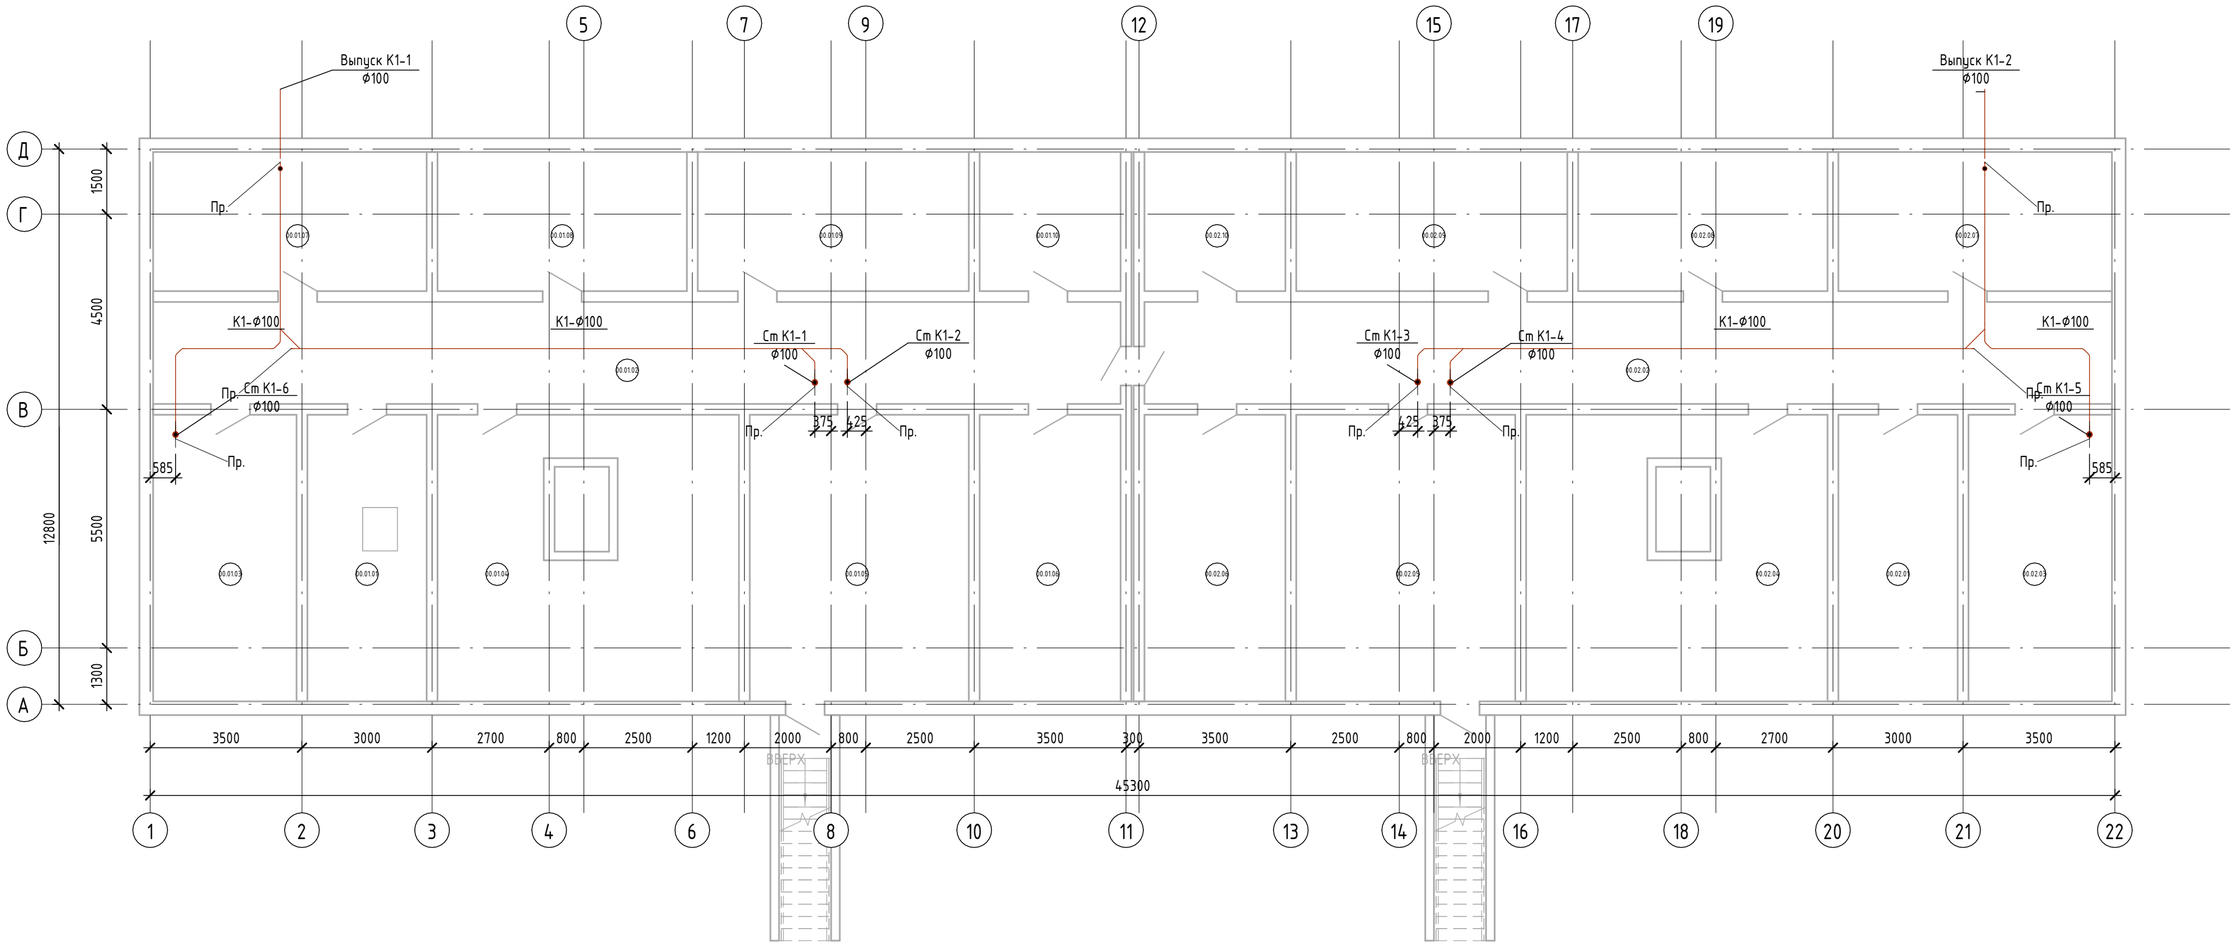


Примечания:
1. Планы и схемы систем рассматривать совместно.
2. Монтаж трубопроводов производить с учетом прокладки смежных систем.
3. Отметки трубопроводов даны по лотку трубы.
4. Отметки трубопроводов и оборудования даны относительно нуля здания.
5. Привязки и отметки трубопроводов уточнять по месту.
6. Напротив ревизий на стояках в коробах шахт предусмотреть люки не менее 0,3х0,4 м (СП 30.13330.2020, п. 18.9).
7. В местах пересечения стен и перегородок трубопроводы прокладывать в гильзах; в перекрытиях — противопожарные муфты.

| Изм. | Кол.уч. | Лист | №док. | Подп. | Дата | НИУ МГСУ 08.03.01*-КП-2026 - ВК | | | |
|---|---|---|---|---|---|---|---|---|---|
| | | | | | | Системы холодного водоснабжения и водоотведения здания | | | |
| Разраб. | | Буев | | | | Наименование здания. Жилой дом. Вариант 3 | Стадия | Лист | Листов |
| Пров. | | | | | | | У | 5 | 7 |
| | | | | | | План подвала. Система К1 | НИУ МГСУ ИИЭСМ Кафедра ½Водоснабжение и водоотведение ½ | | |

Согласовано

Взам. инв. №

Подп. и дата

Инв. № подл.

Формат А2 420 х 594