


План строительной площадки с рабочими отметками и линией нулевых работ М 1:2000

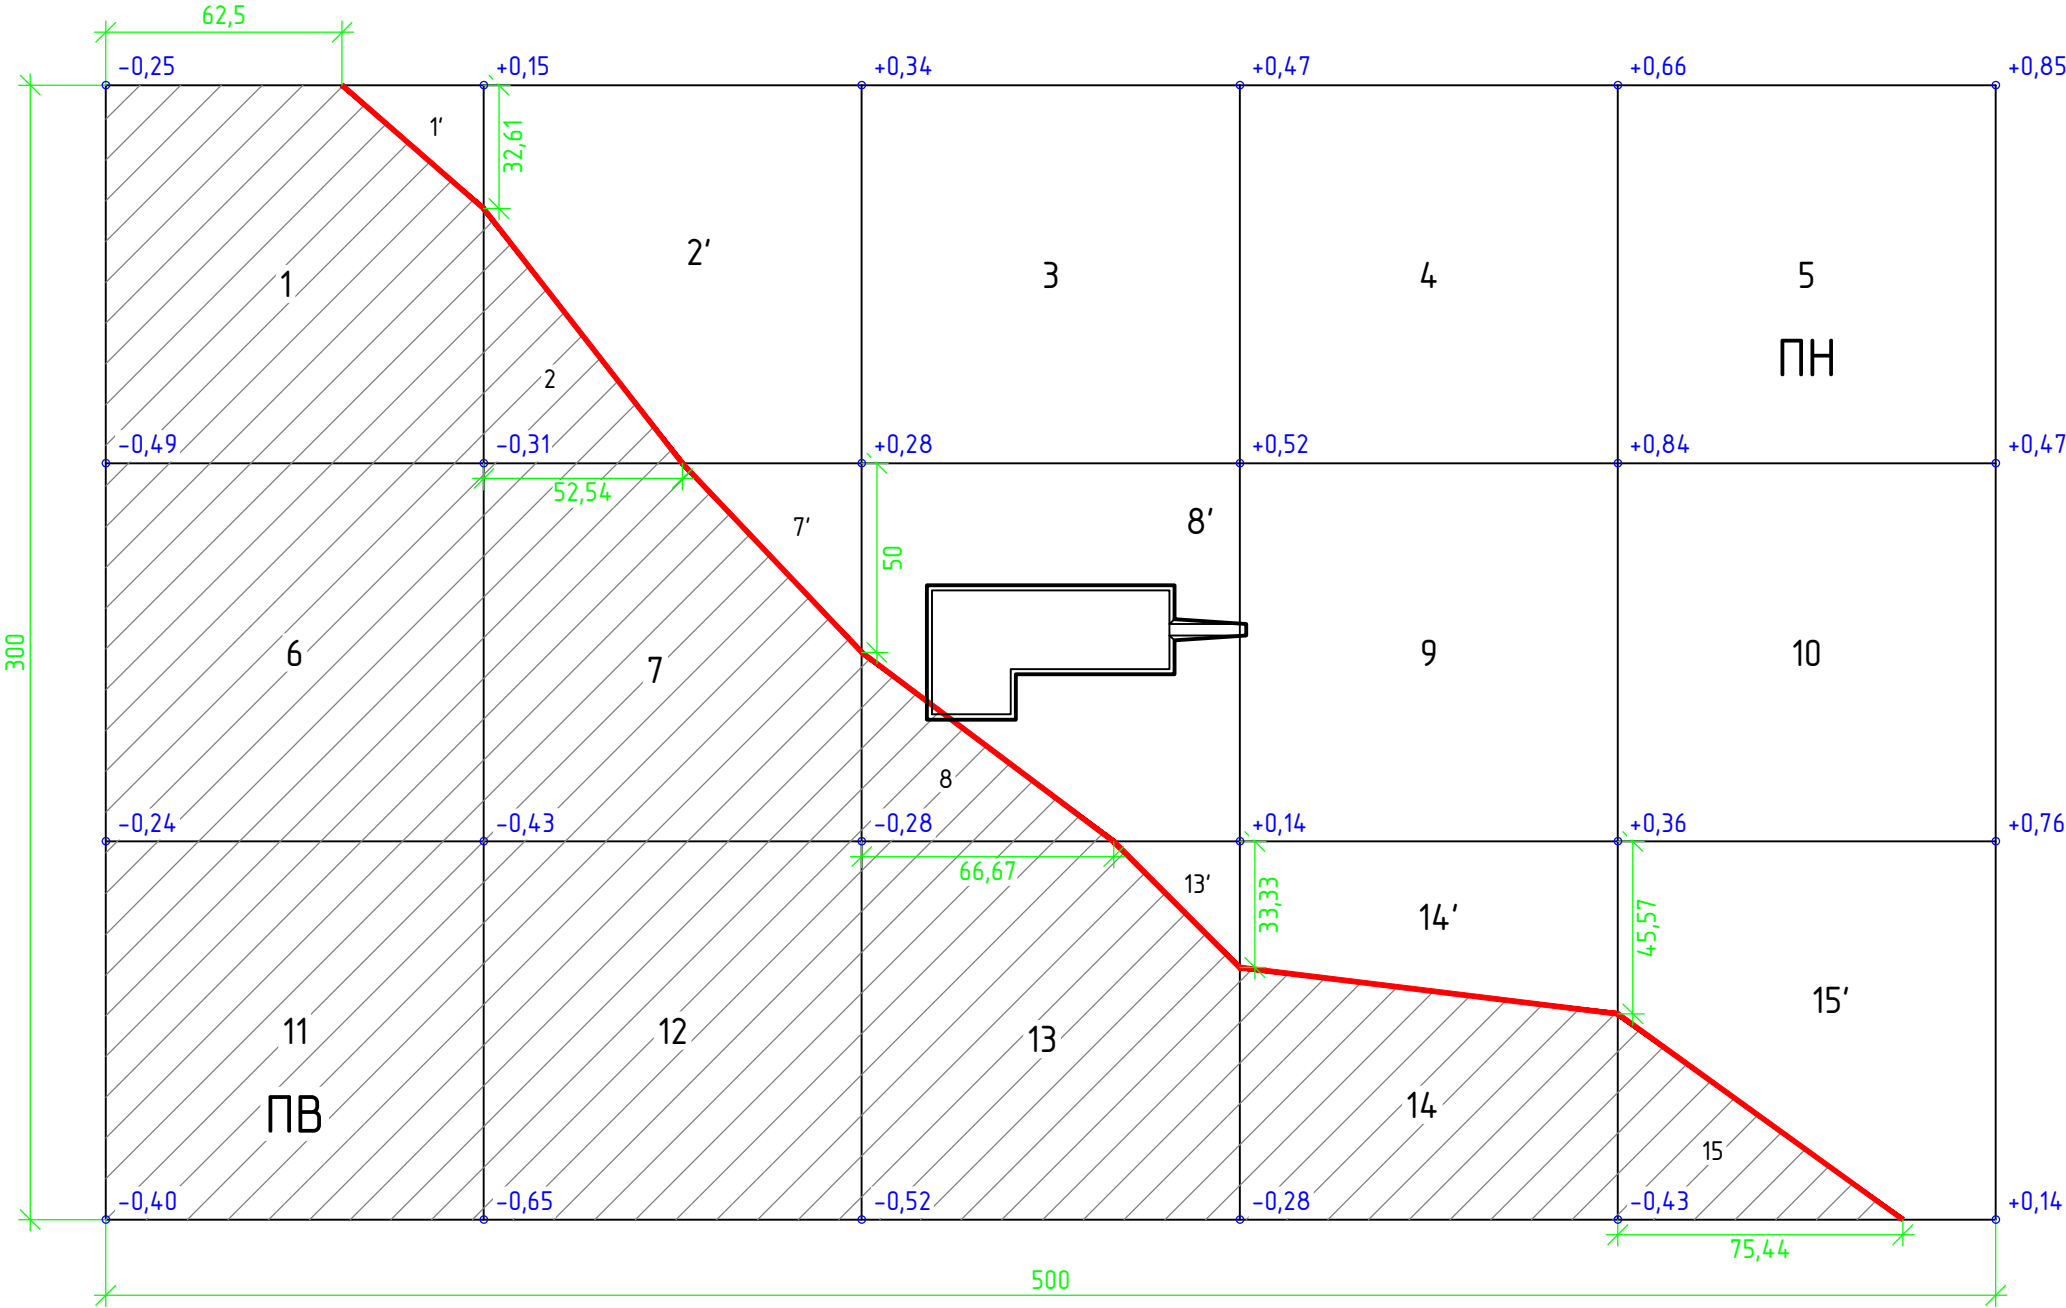

Условные обозначения

- линия нулевых работ (ЛНР)
- ▨ - ПВ - планировочная выемка
- - ПН - планировочная насыпь
- +0,15 - рабочая отметка, м (+ насыпь, - выемка)
- 7' - номер фигуры; со штрихом - насыпная часть квадрата
- 37,5 - расстояние до точки нулевых работ, м
- - контур котлована

Объемы планировочных работ

	Ф, м²	V, м³
Выемка ПВ	69 191,63	20 209,47
Насыпь ПН	80 808,37	33 543,96
ПН / Кор, Кор = 1,04		32 253,81

						НИУ МГСУ 08.05.01 – КР – 2026						
						Разработка технологической карты на производство земляных работ. Вариант 2, грунт – супесь						
Изм.	Кол.уч.	Лист	№док.	Подп.	Дата	Графическая часть курсовой работы		Стадия	Лист	Листов		
Разработал	Буев Д.Р.							У	1	4		
Проверил	Забелина О.Б.											
Т. контр.												
						План строительной площадки с рабочими отметками и ЛНР М 1:2000		Кафедра технологий и организации строительного производства				
Н. контр.												
Утв.												