


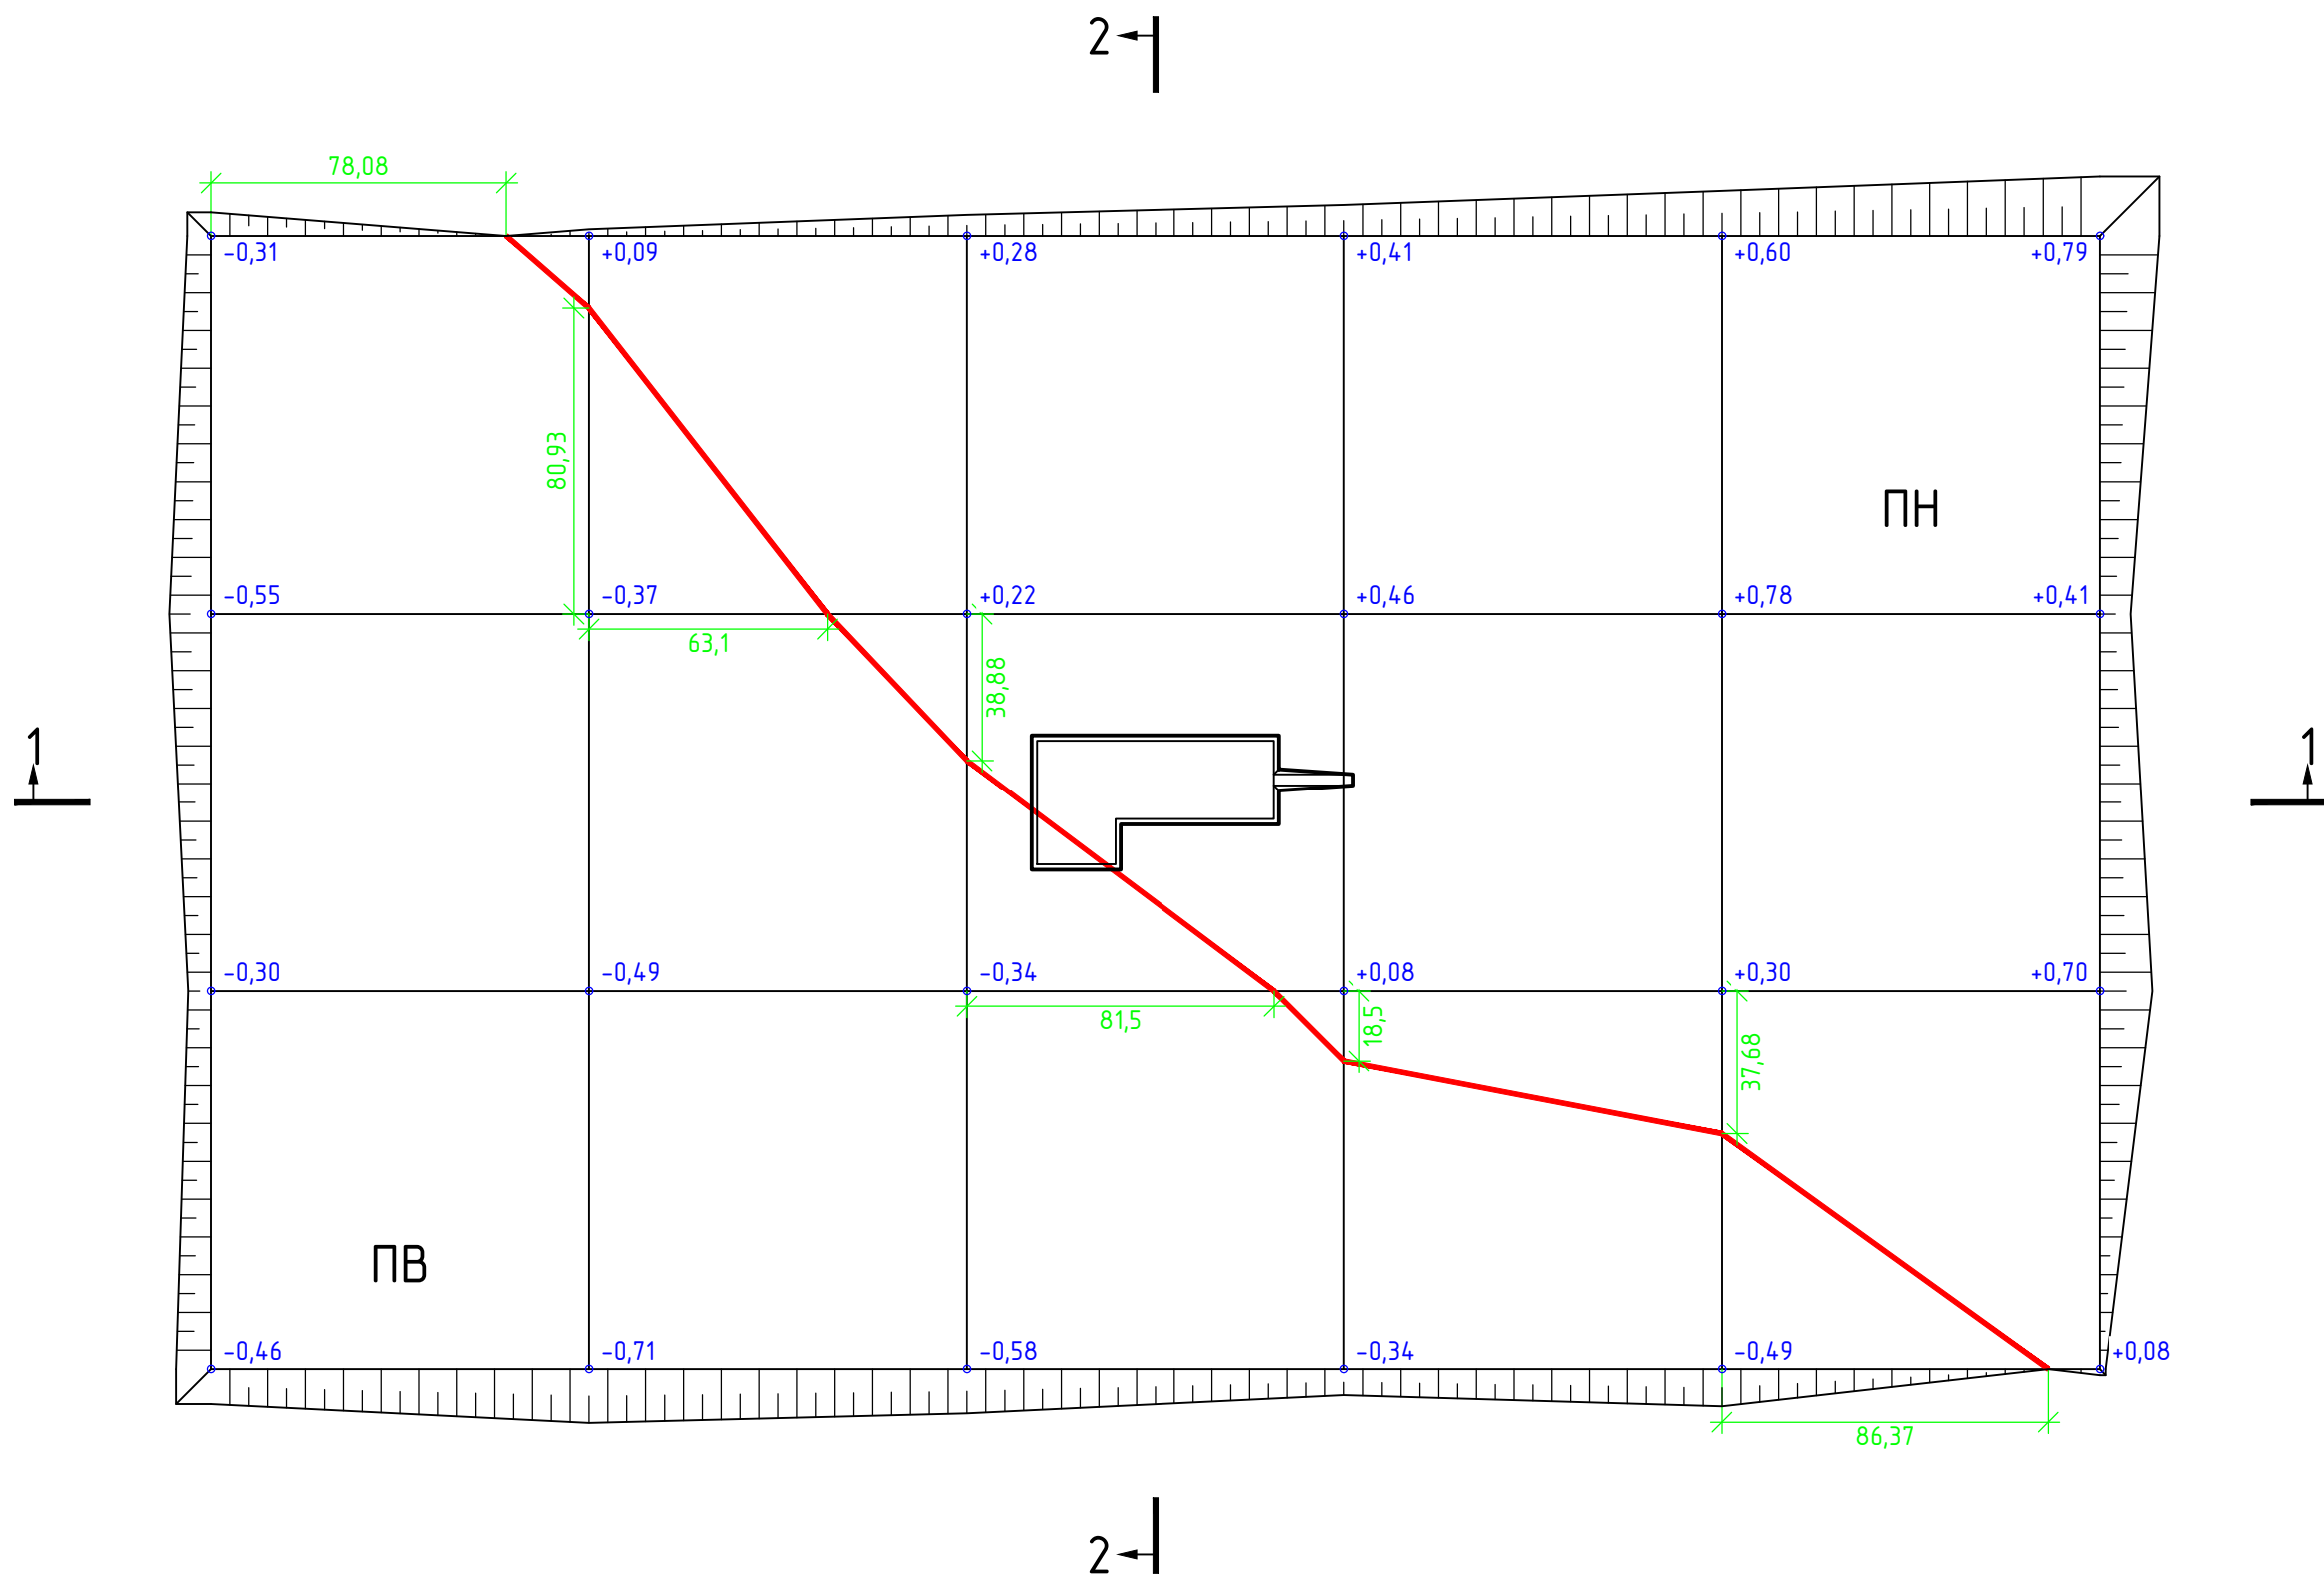

						НИУ МГСУ 08.05.01 – КР – 2026				
						Разработка технологической карты на производство земляных работ. Вариант 2, грунт – супесь				
Изм.	Кол.уч.	Лист	№ док.	Подп.	Дата	Графическая часть курсовой работы		Стадия	Лист	Листов
Разработал	Буев Д.Р.							У	2	
Проверил	Забелина О.Б.					План площадки с окончательными рабочими отметками и обводами Мз 1:2000, Мб 1:100		Кафедра технологий и организации строительного производства		
Т. контр.										
Н. контр.										
Утв.										