Генеральный план. Системы В1, К1 (1 : 500)

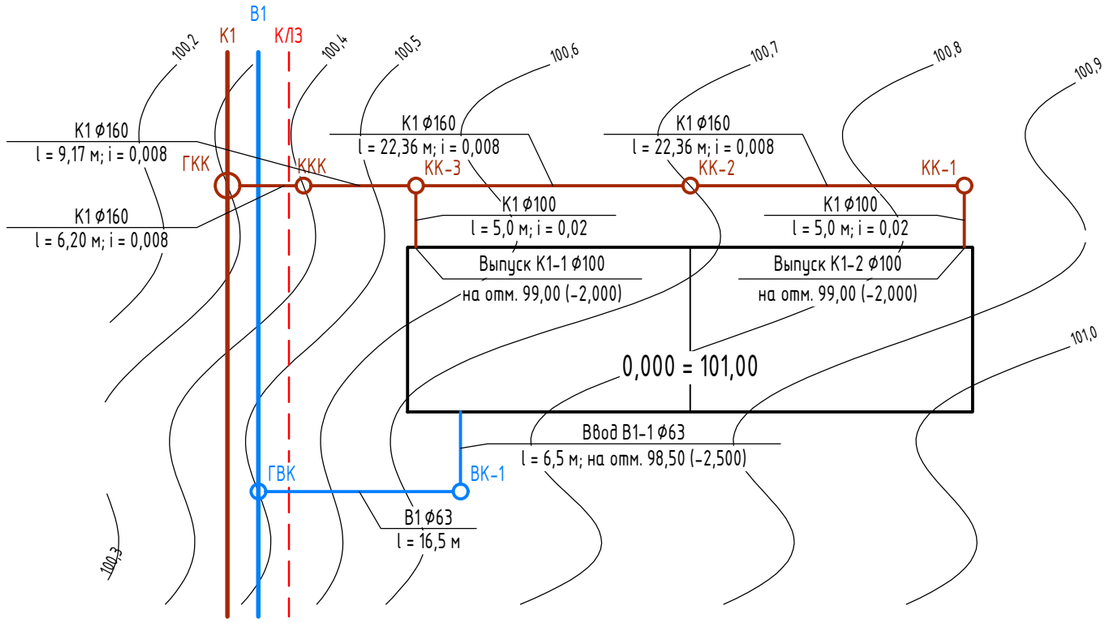

Согласовано

Взам. инв. №

Подп. и дата

Инв. № подл.

Изм.	Кол.уч.	Лист	№док.	Подп.	Дата	НИУ МГСУ 08.03.01*-КП-2026 - ВК		
						Системы холодного водоснабжения и водоотведения здания		
Разраб.						Наименование здания. Жилой дом. Вариант 3	Стадия: У	Лист: 8 / Листов: 8
Пров.								
						Генеральный план. Системы В1, К1	НИУ МГСУ ИИЗСМ Кафедра «Водоснабжение и водоотведение»	

Формат А3 297 x 420