Генеральный план. Системы В1, К1 (1 : 500)

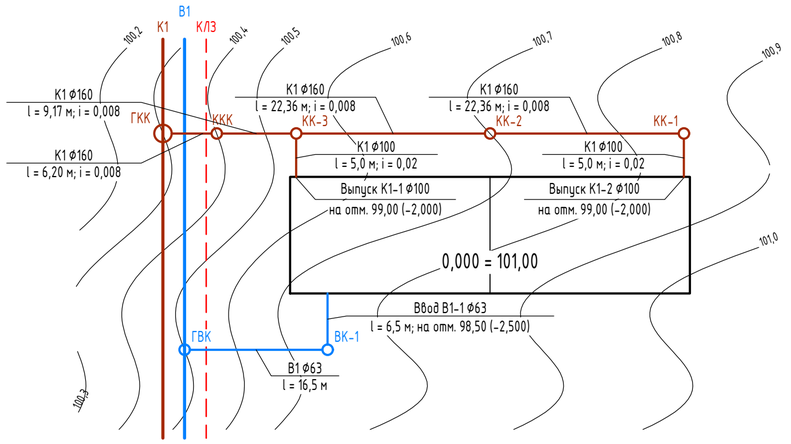

Согласовано

Взам. инв. №

Подп. и дата

Инв. № подл.

						НИУ МГСУ 08.03.01*-КП-2026 - ВК	
						Системы холодного водоснабжения и водоотведения здания	
Изм.	Кол.уч.	Лист	№док.	Подп.	Дата		
Разраб.						Наименование здания. Жилой дом. Вариант 3	Стадия: У; Лист: 7; Листов: 7
Пров.							
						Генеральный план. Системы В1, К1	НИУ МГСУ ИИЭСМ Кафедра «Водоснабжение и водоотведение»

Формат А2 420 x 594