
Аксонометрическая схема. Система К1

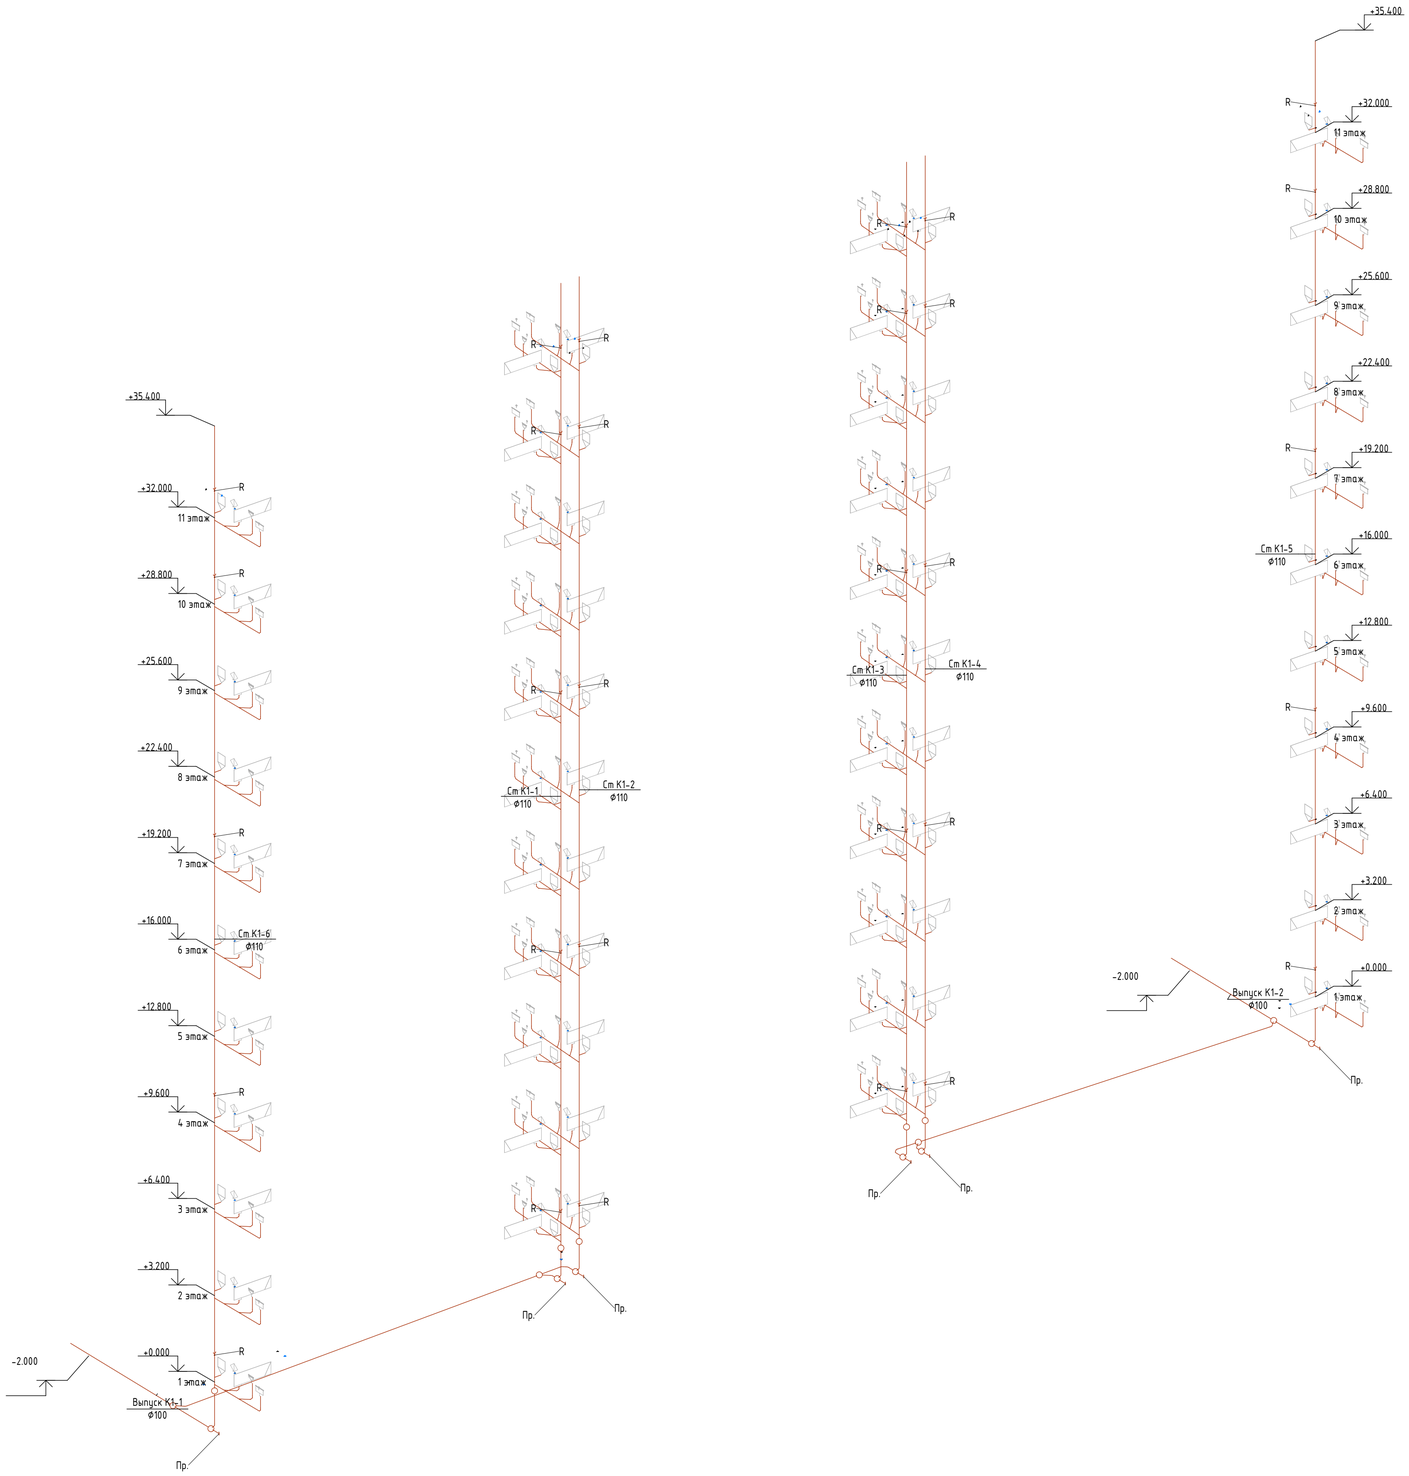

Примечания:
1. Планы и схемы систем рассматривать совместно.
2. Монтаж трубопроводов производить с учетом прокладки смежных систем.
3. Отметки трубопроводов даны по лотку трубы.
4. Отметки трубопроводов и оборудования даны относительно нуля здания.
5. Привязки и отметки трубопроводов уточнять по месту.

Изм.	Кол.уч.	Лист	№док.	Подп.	Дата	НИУ МГСУ 08.03.01*-КП-2026 - ВК		
						Системы холодного водоснабжения и водоотведения здания		
Разраб.						Наименование здания. Жилой дом. Вариант 3	Стадия	Лист	Листов
Пров.							У	6	7
						Аксонометрическая схема. Система К1	НИУ МГСУ ИИЭСМ Кафедра "Водоснабжение и водоотведение"	

Согласовано

Взам. инв. №

Подп. и дата

Инв. № подл.

Формат А1 594 x 841