
# План типового этажа. Система К1 ( 1 : 100)

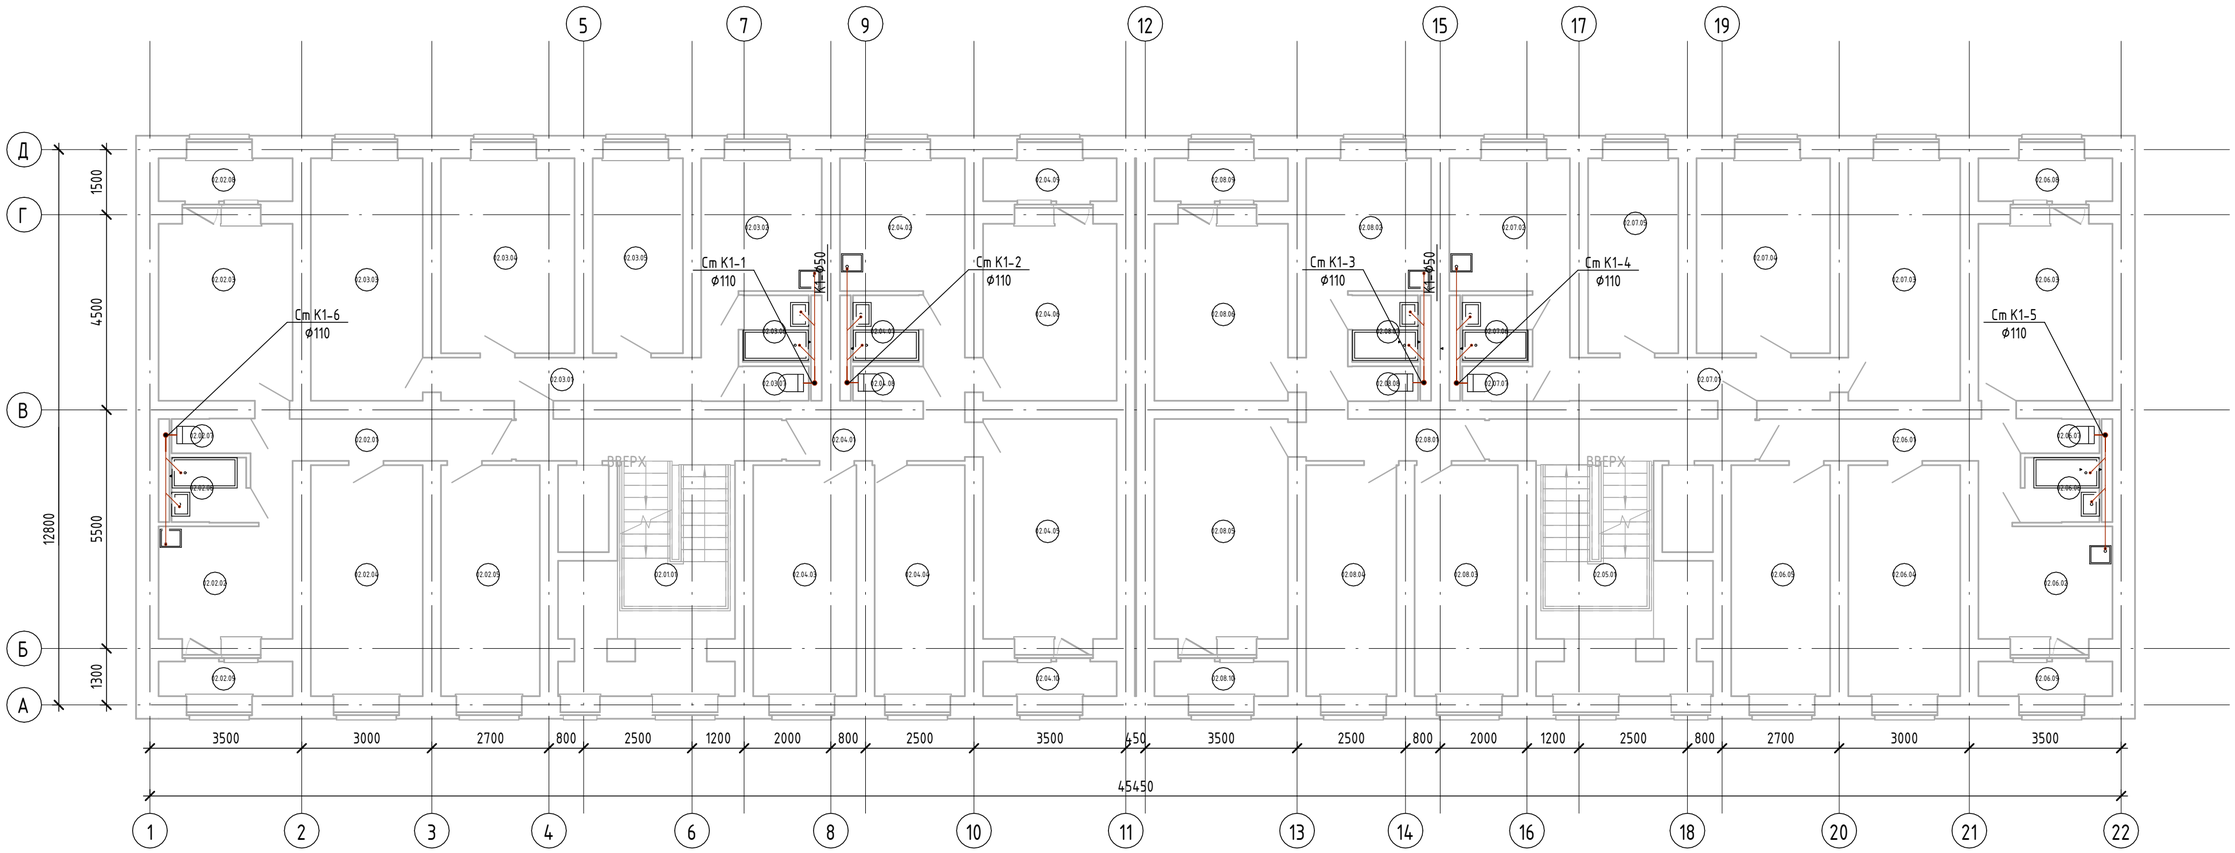


Примечания:
1. Планы и схемы систем рассматривать совместно.
2. Монтаж трубопроводов производить с учетом прокладки смежных систем.
3. Отметки трубопроводов даны по лотку трубы.
4. Отметки трубопроводов и оборудования даны относительно нуля здания.
5. Привязки и отметки трубопроводов уточнять по месту.

Согласовано

Взам. инв. №

Подп. и дата

Инв. № подл.

| Изм. | Кол.уч. | Лист | №док. | Подп. | Дата |
|---|---|---|---|---|---|
| Разраб. | | Буев | | | |
| Пров. | | | | | |

НИУ МГСУ 08.03.01*-КП-2026 - ВК

Системы холодного водоснабжения и водоотведения здания

| Наименование здания. Жилой дом. Вариант 3 | Стадия | Лист | Листов |
|---|---|---|---|
| | У | 4 | 7 |
| План типового этажа. Система К1 | НИУ МГСУ ИИЭСМ Кафедра ½Водоснабжение и водоотведение½ | | |

Формат А2 420 x 594